




1 EXISTING NORTH ELEVATION




2 EXISTING EAST ELEVATION


25 PARNASSUS AVENUE SAN FRANCISCO, CA 94117		
THIS DRAWING IS A RECORD OF REAL PROPERTY THAT IS GENERALLY ACCEPTED TO BE SUITABLE FOR USE IN PLANNING, DESIGN, LEASE, AND GENERAL ASSET MANAGEMENT. IT SHOULD NOT BE USED TO DETERMINE EXACT MEASUREMENTS OF SPACES OR ARTIFACTS FOUND HEREIN FOR ANY PURPOSE.		
EXTERIOR ELEMENTS HAVE BEEN MEASURED AND DRAFTED FOR REFERENCE ONLY - THIS IS NOT A SURVEY.		
 RED BRIDGE DESIGN SAN FRANCISCO REDBRIDGEDESIGN.COM		
EXISTING EXTERIOR ELEVATIONS		
REF: 25sf-7_City_SFD REV: 0 DRAWN BY: MV AUDITED BY: TL	SHEET SIZE: 24x36 SCALE: 1/4"=1'-0" FIELD MEASURE: 10/10/22	AX-201 5 OF 7

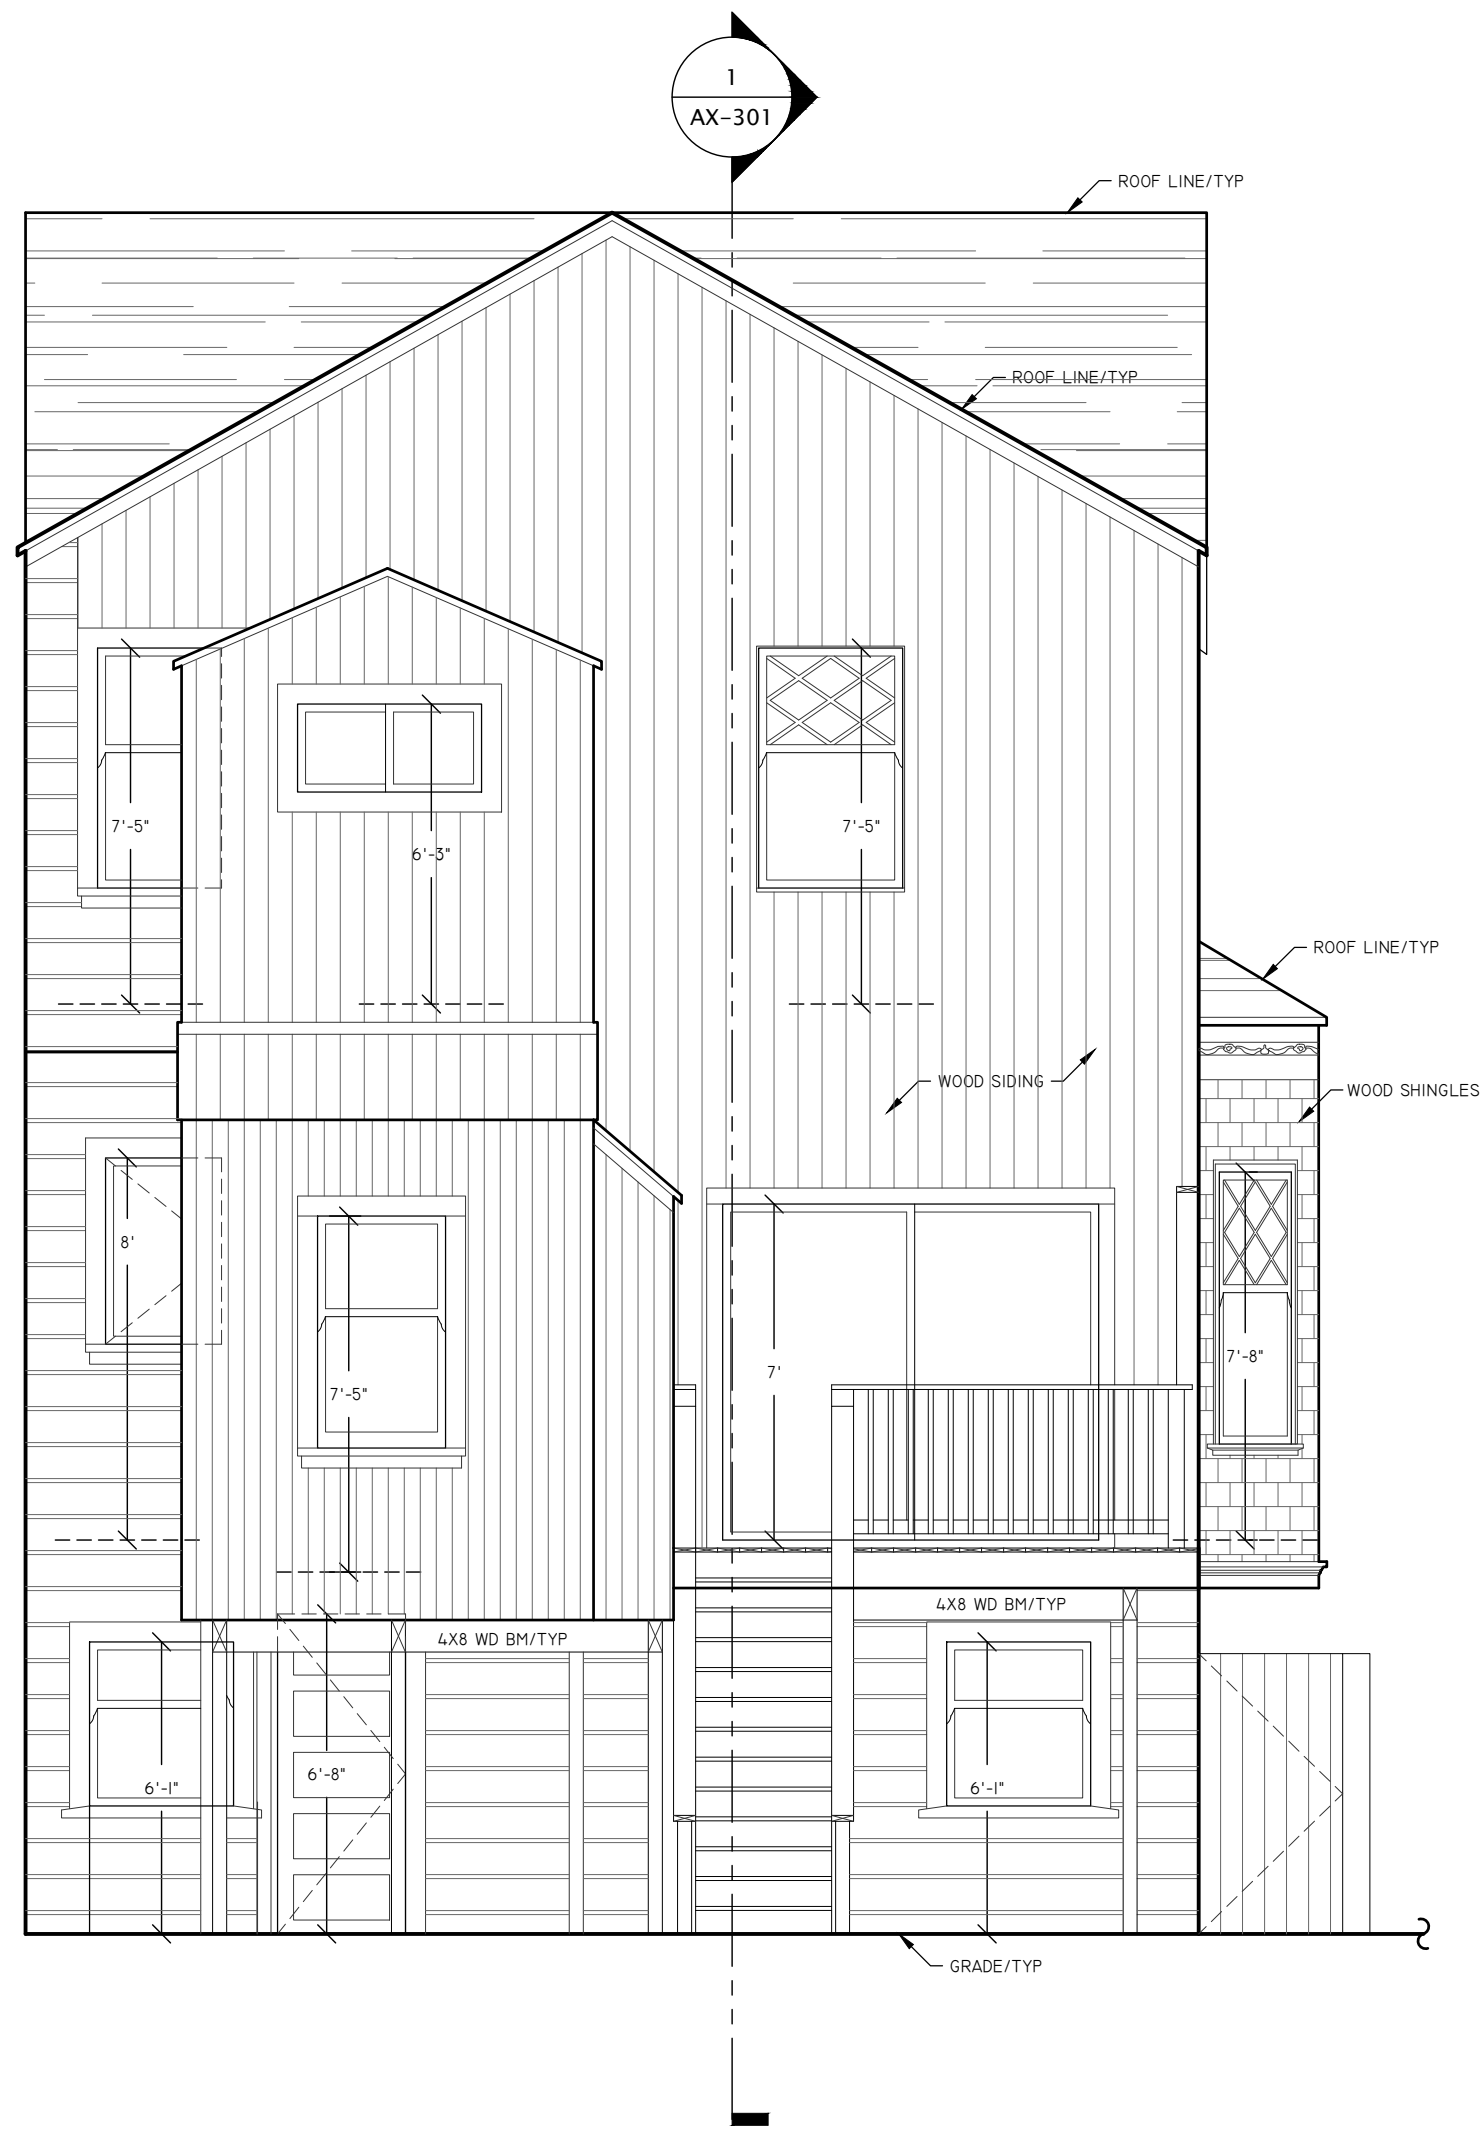

1 EXISTING SOUTH ELEVATION

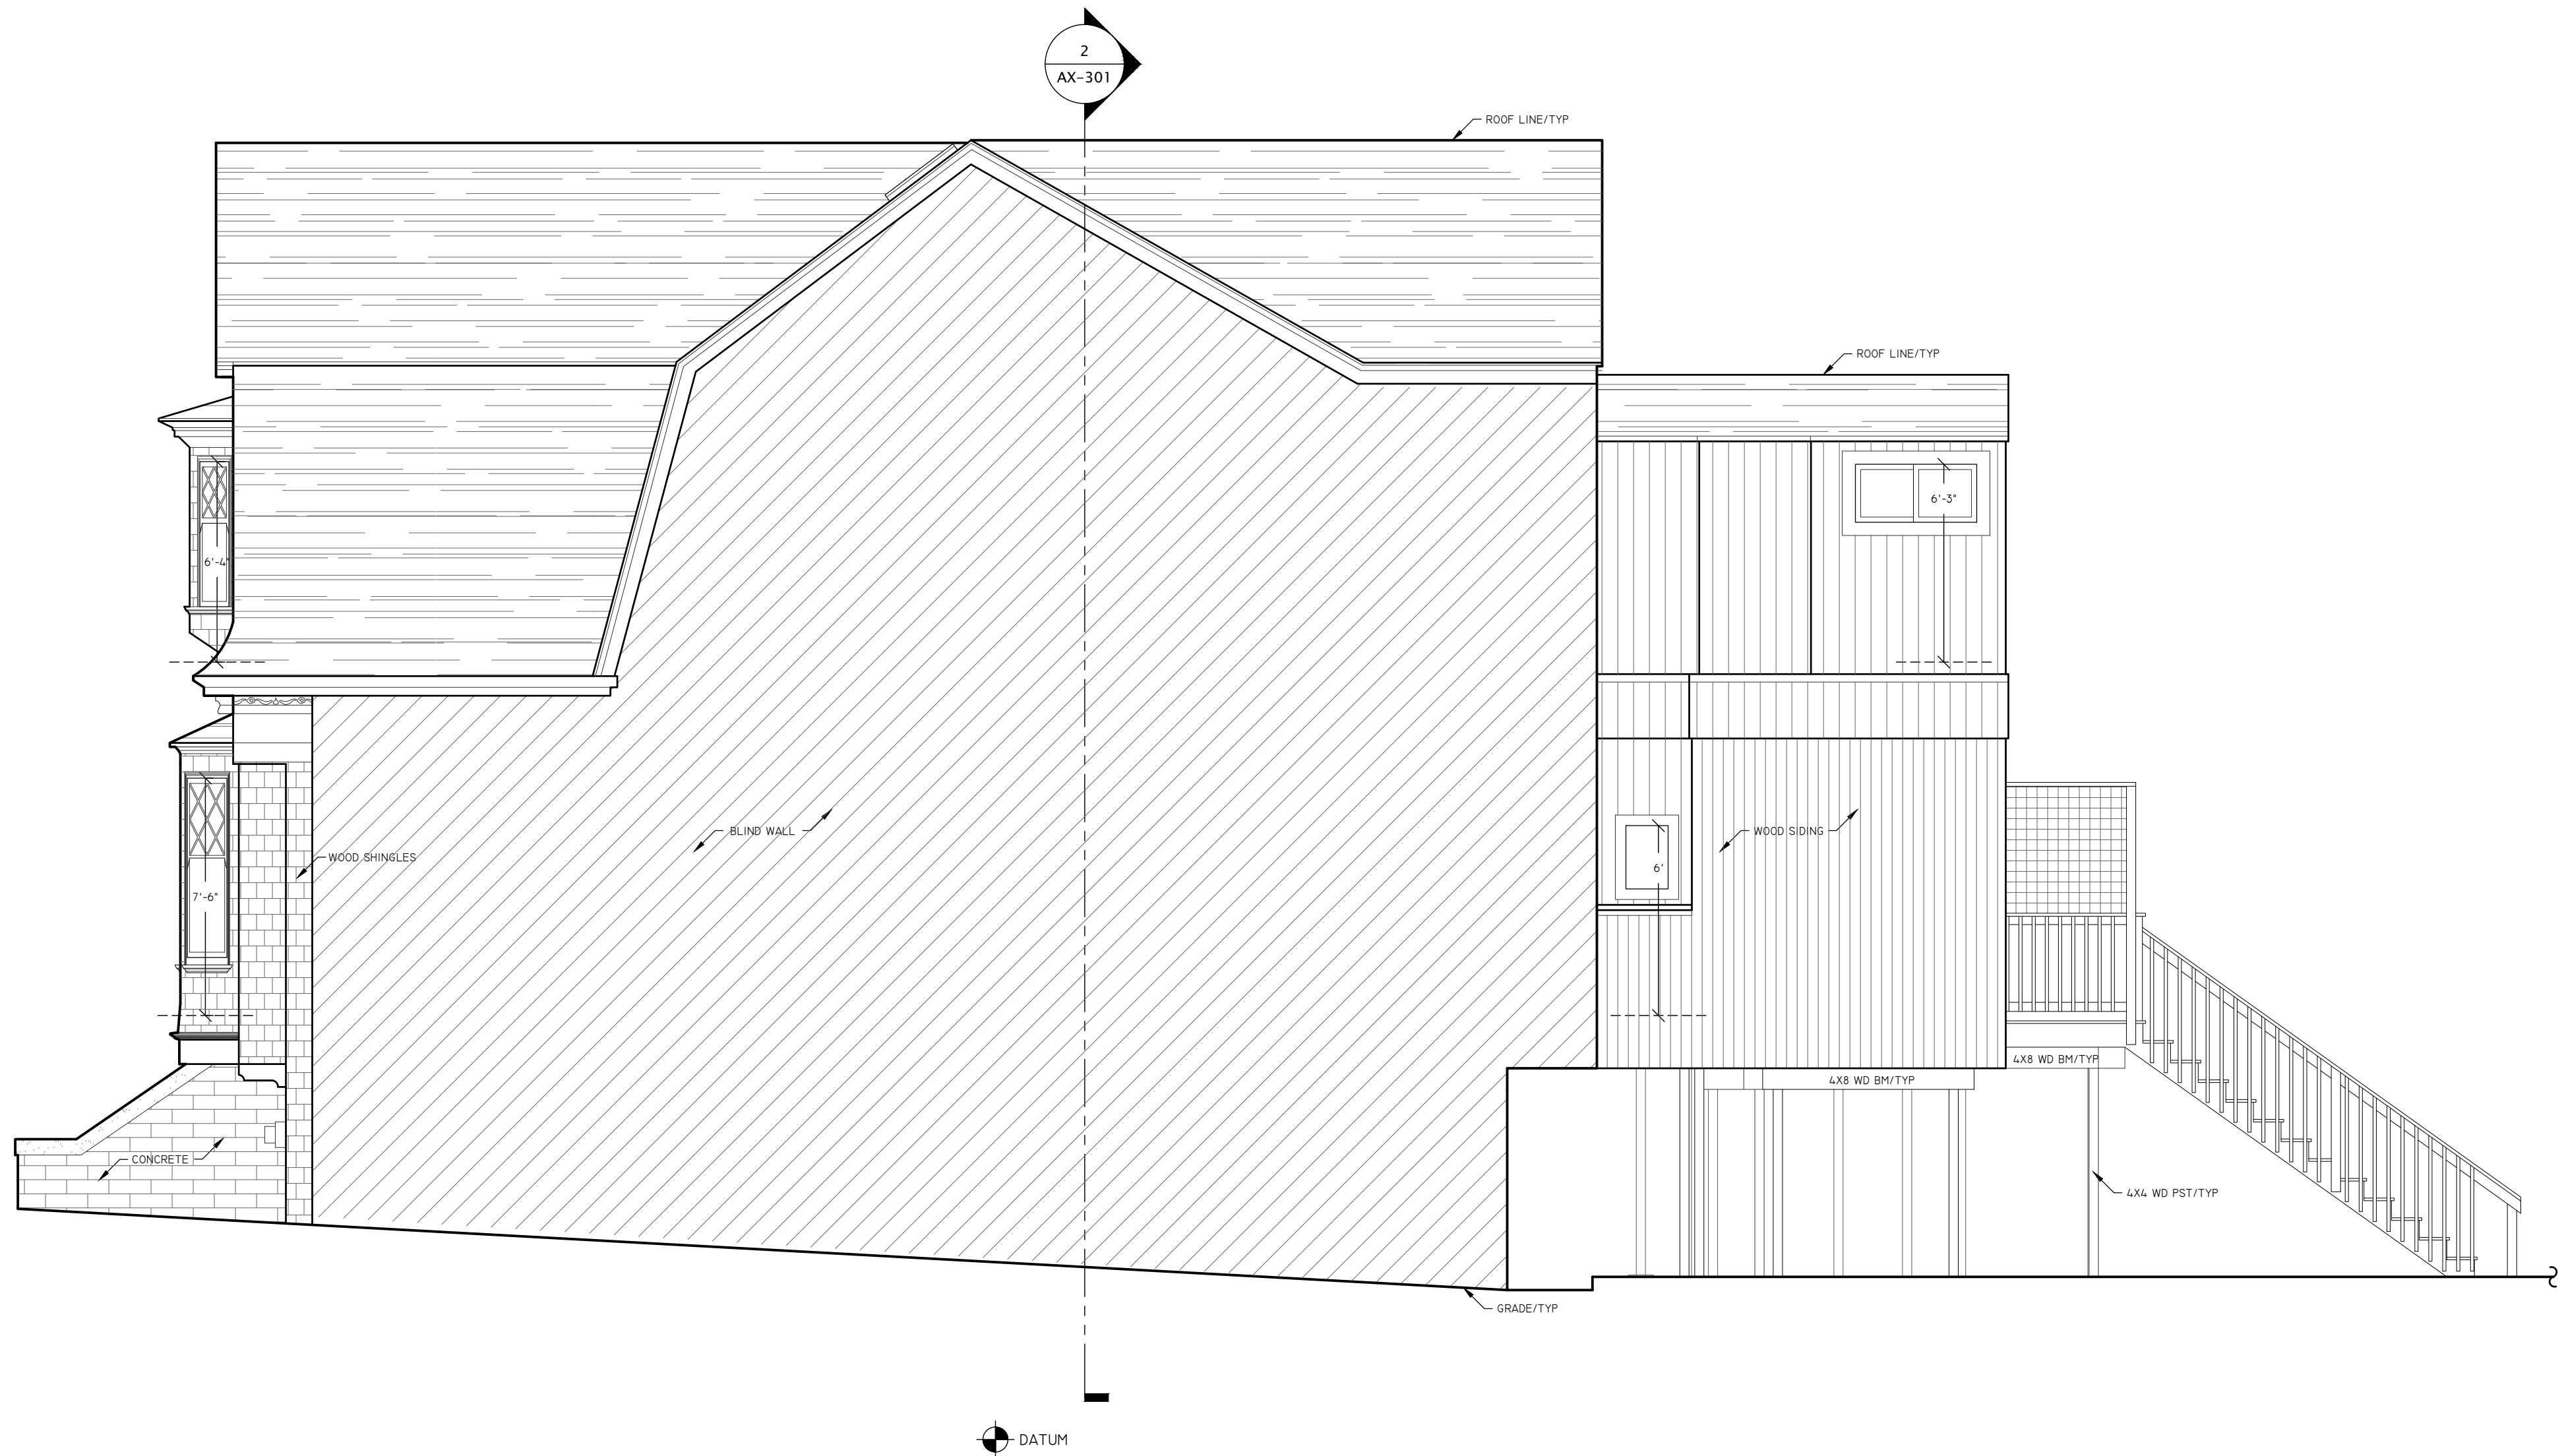

2 EXISTING WEST ELEVATION

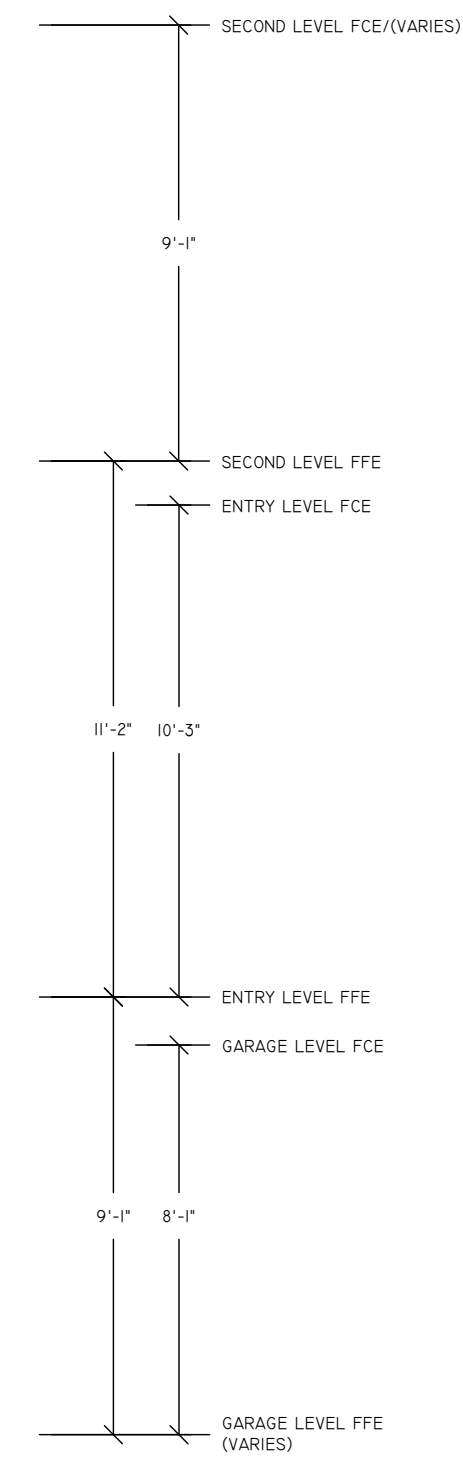

25 PARNASSUS AVENUE
SAN FRANCISCO, CA 94117

THIS DRAWING IS A RECORD OF REAL PROPERTY
THAT IS GENERALLY ACCEPTED TO BE SUITABLE
FOR USE IN PLANNING, DESIGN, LEASE, AND
GENERAL ASSET MANAGEMENT. IT SHOULD NOT BE
USED TO DETERMINE EXACT MEASUREMENTS OF
SPACES OR ARTIFACTS FOUND HEREIN FOR ANY
PURPOSE.
EXTERIOR ELEMENTS HAVE BEEN MEASURED AND
DRAFTED FOR REFERENCE ONLY - THIS IS NOT A
SURVEY.




EXISTING EXTERIOR ELEVATIONS


REF: 25sf-7_City_SFD
REV: 0
DRAWN BY: MV
AUDITED BY: TL

SHEET SIZE: 24x36
SCALE: 1/4"=1'-0"
FIELD MEASURE:
10/10/22

AX-202
6 OF 7

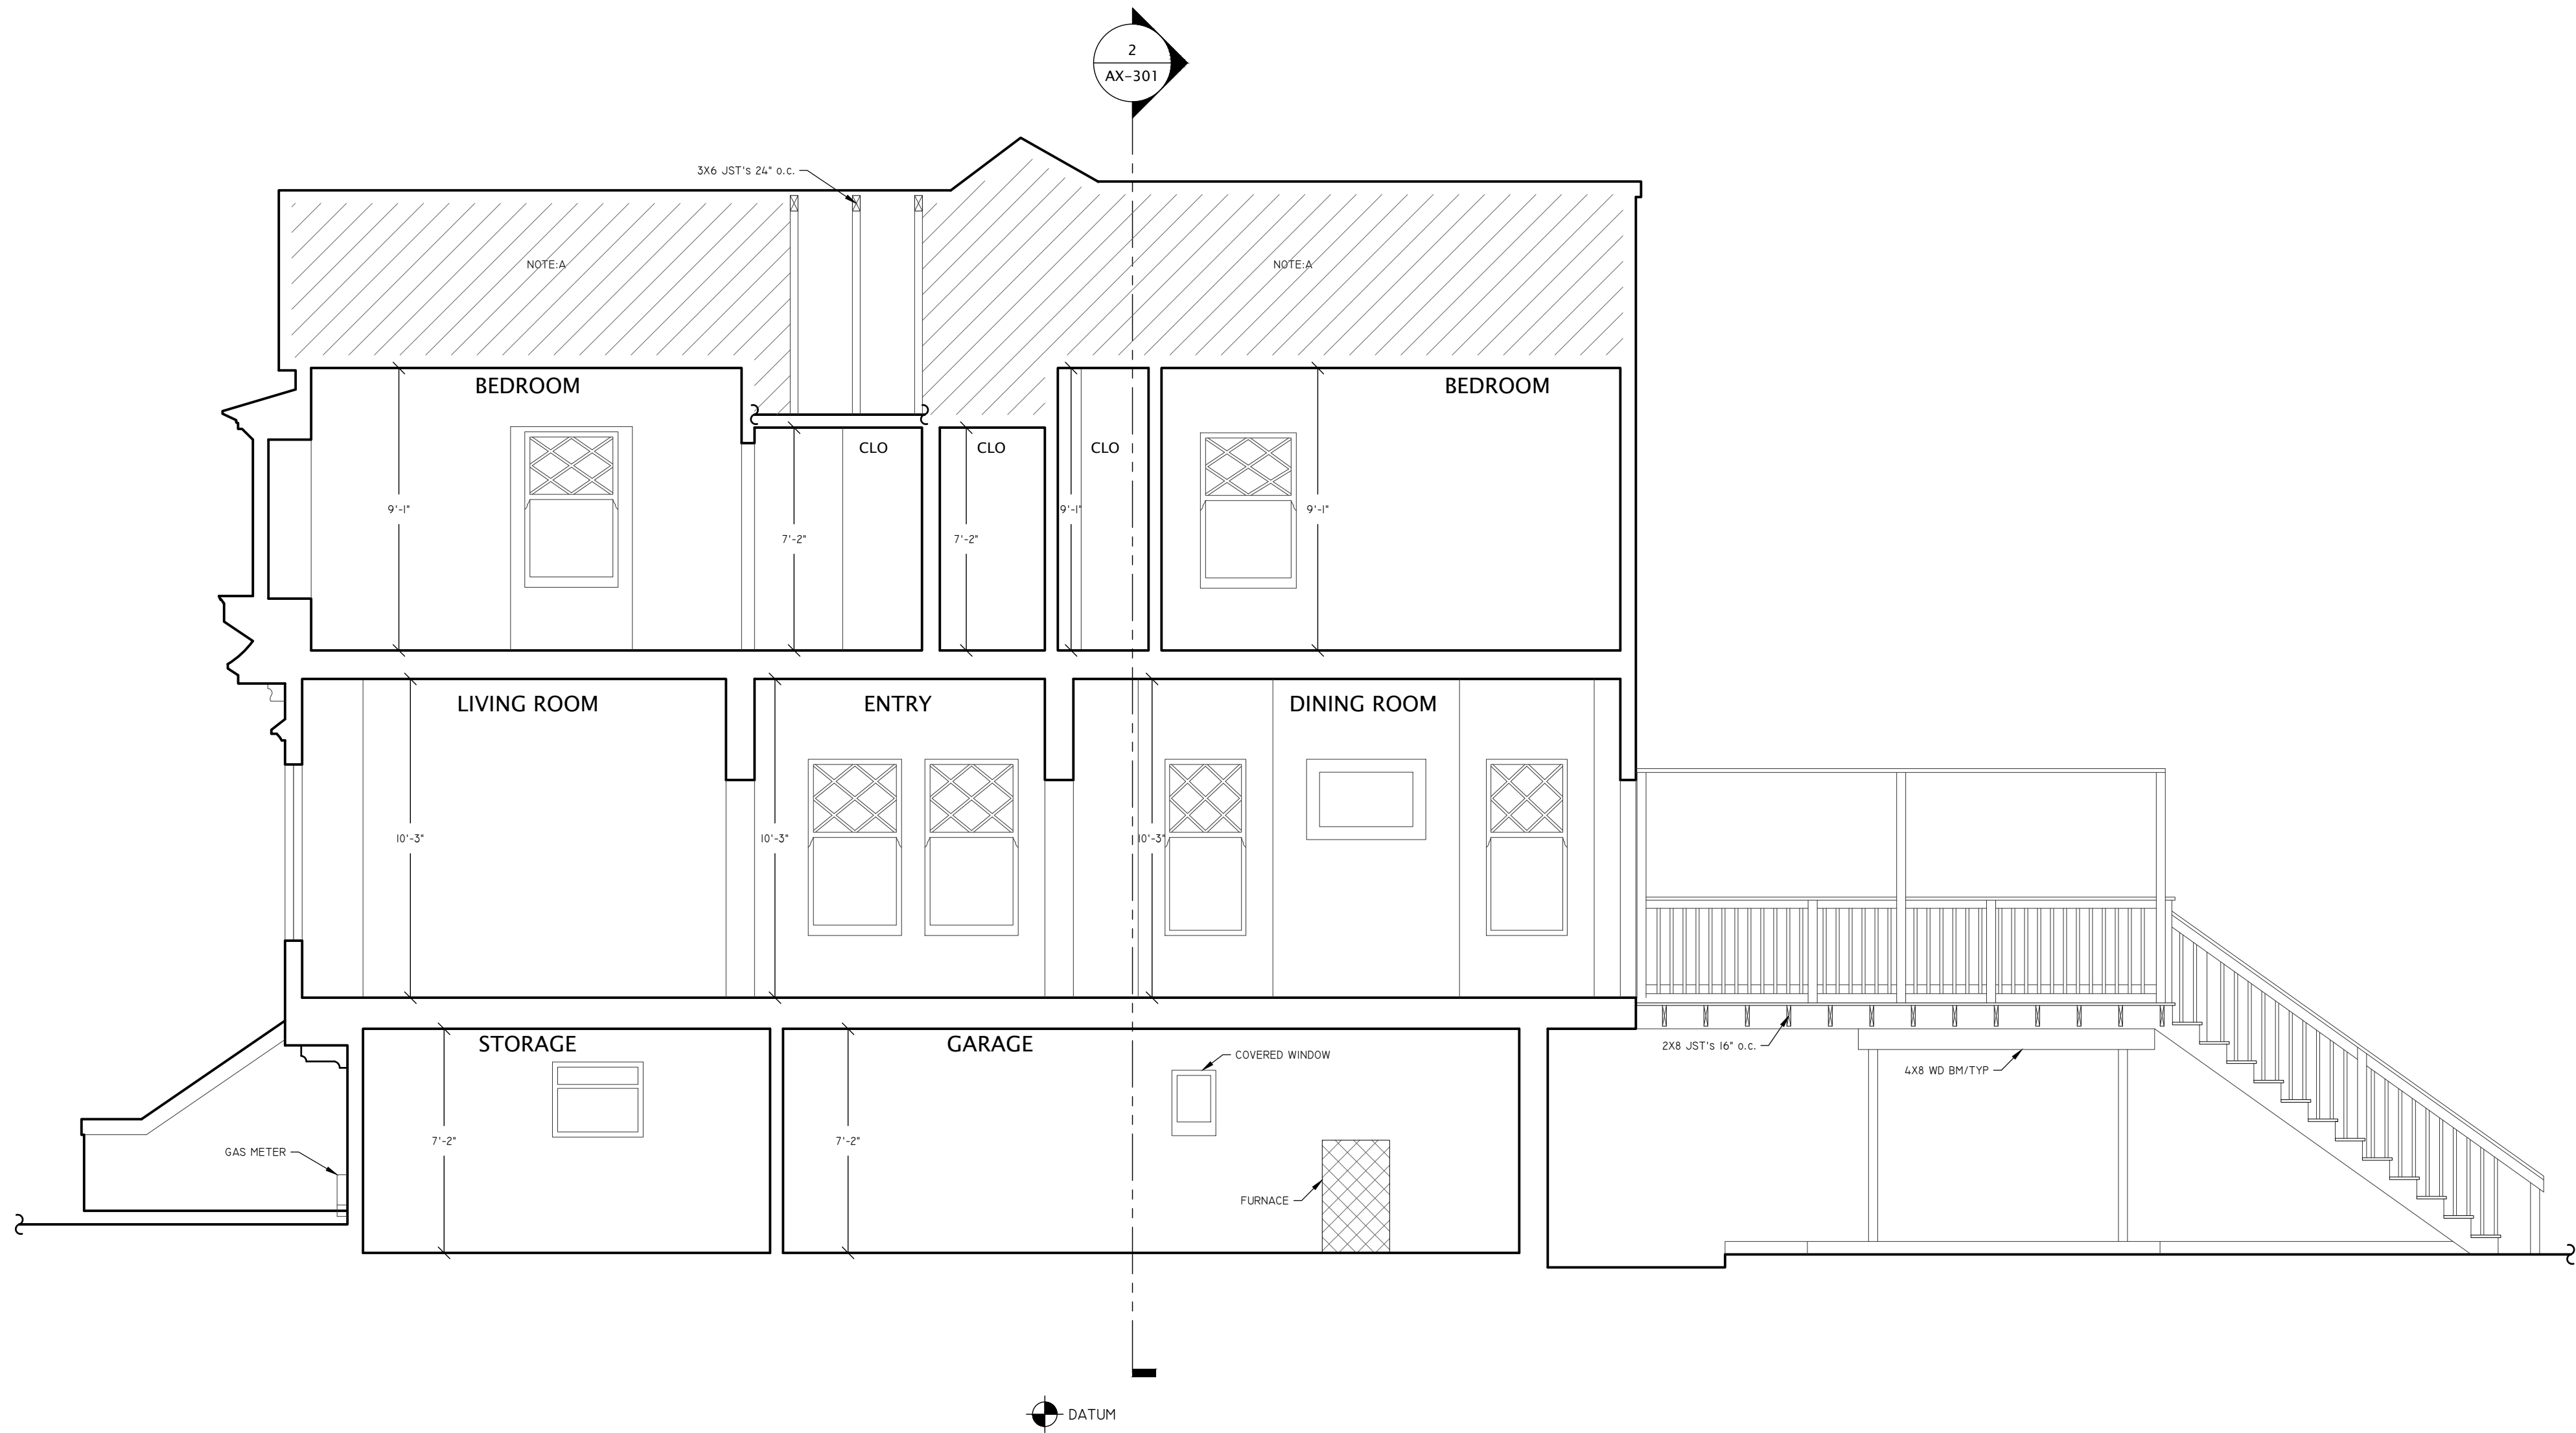


1 EXISTING LONGITUDINAL SECTION

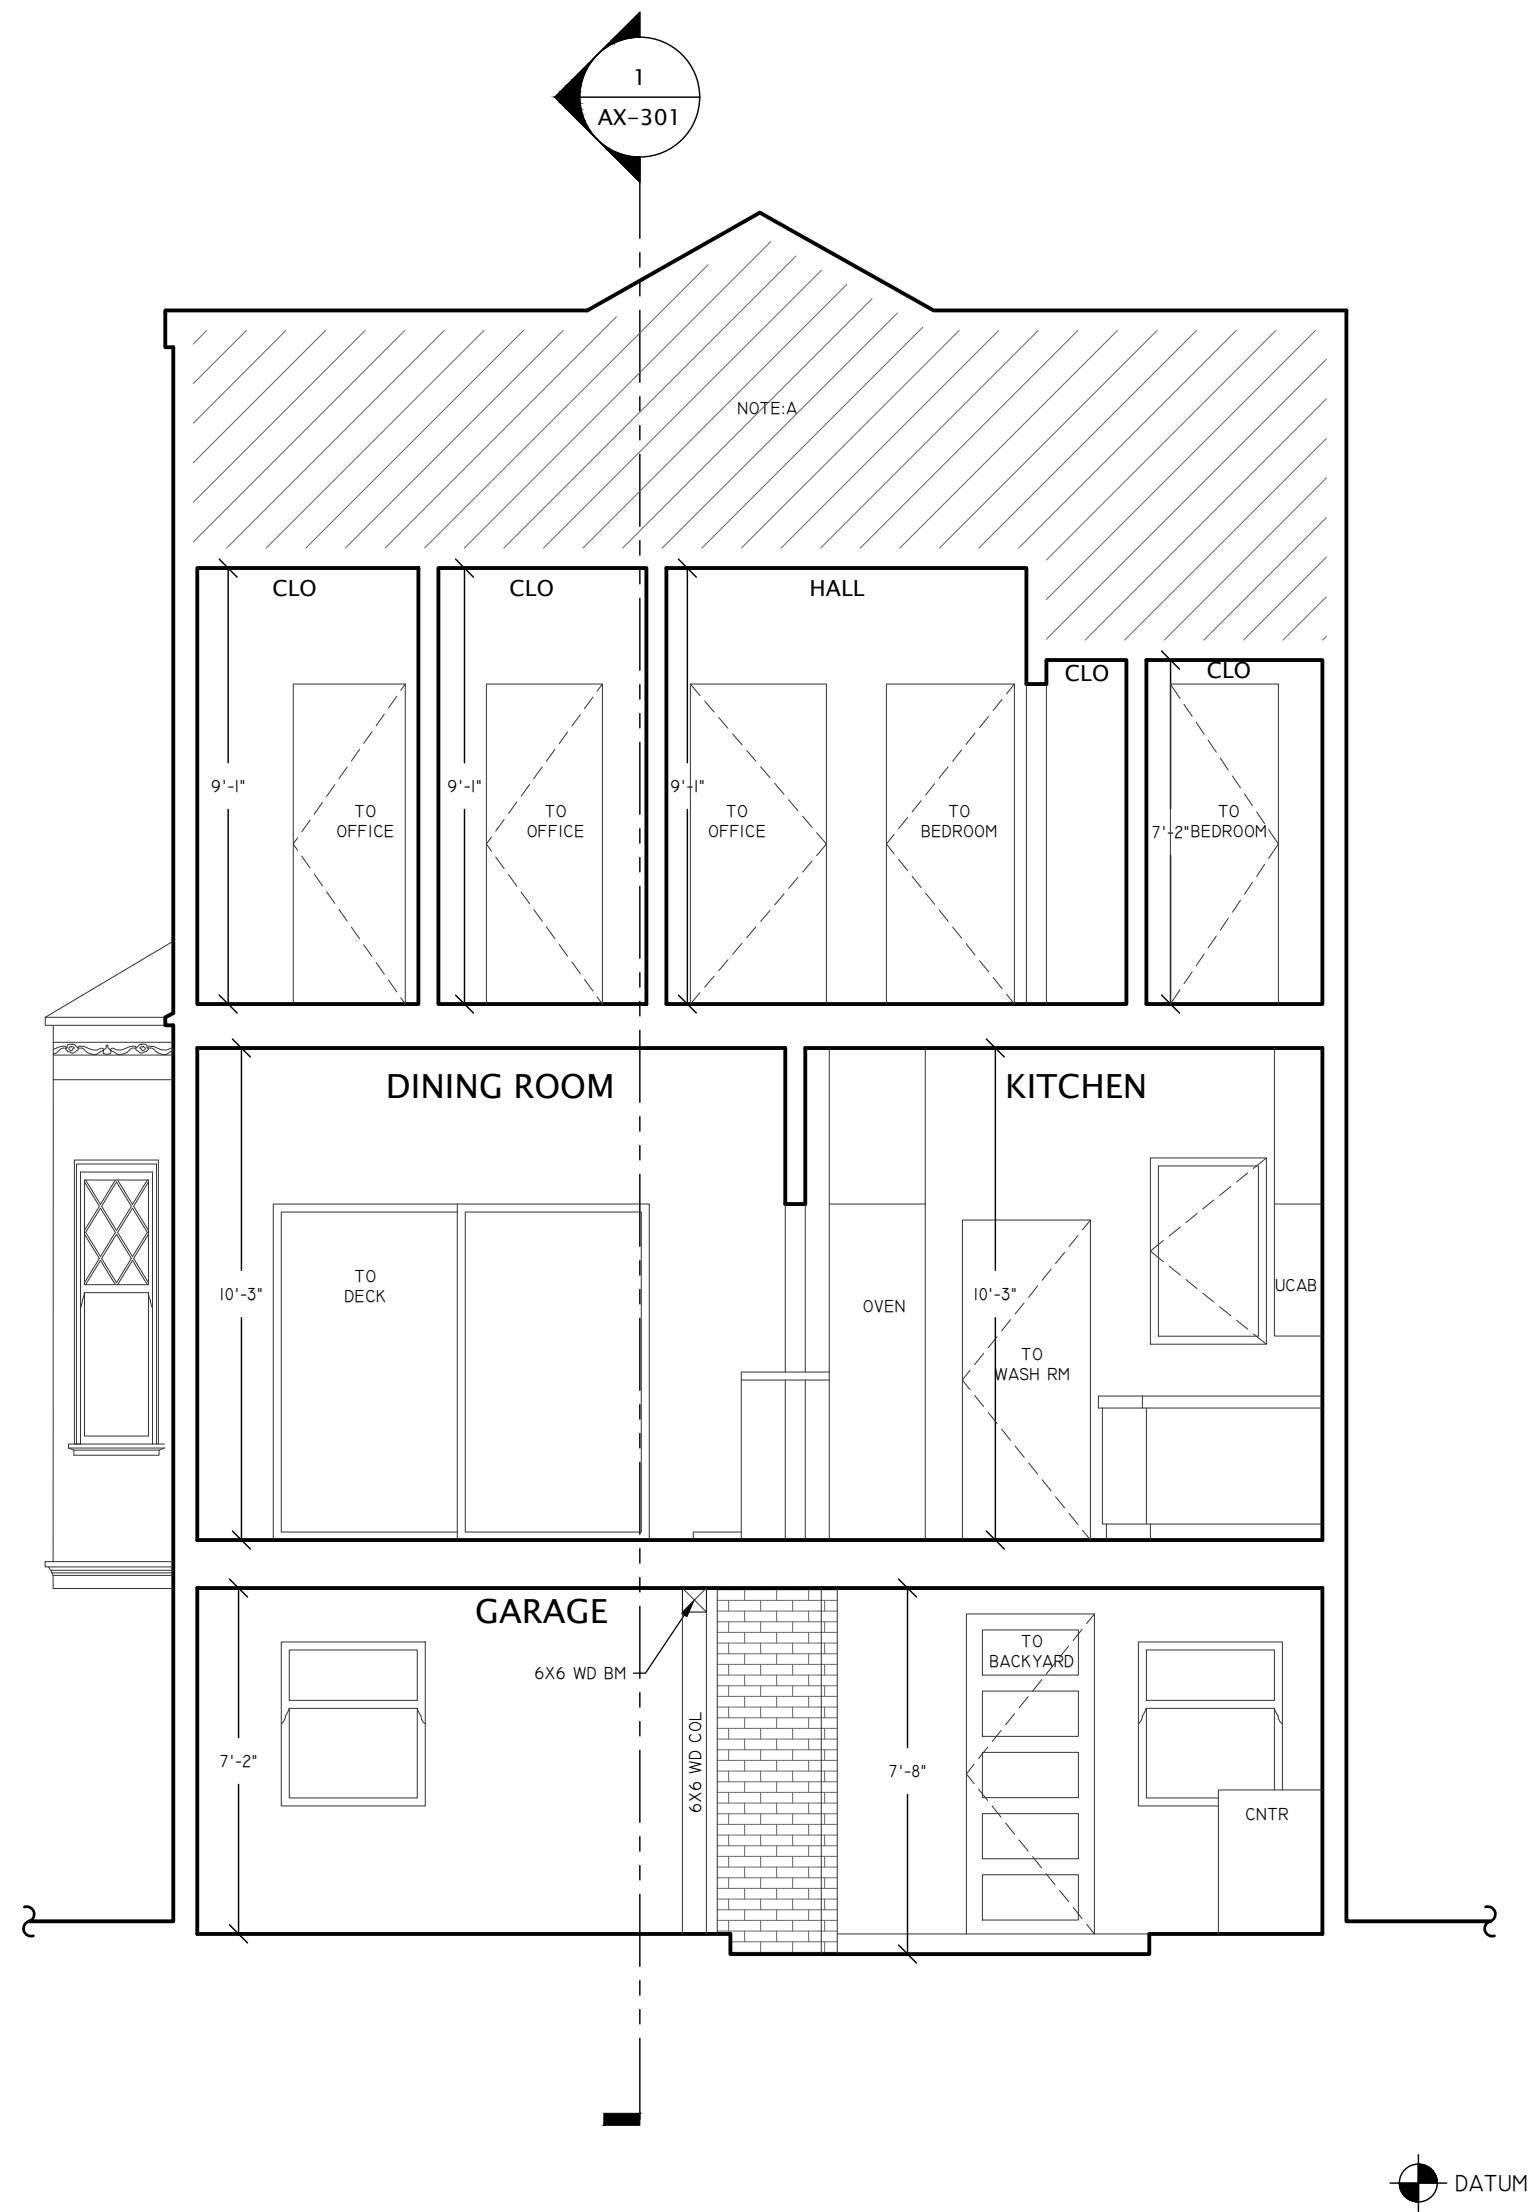


2 EXISTING CROSS SECTION

NOTE A:
THIS AREA NOT ACCESSIBLE AT TIME OF DATA ACQUISITION,
AREA NOT MEASURED.

25 PARNASSUS AVENUE SAN FRANCISCO, CA 94117		
THIS DRAWING IS A RECORD OF REAL PROPERTY THAT IS GENERALLY ACCEPTED TO BE SUITABLE FOR USE IN PLANNING, DESIGN, LEASE, AND GENERAL ASSET MANAGEMENT. IT SHOULD NOT BE USED TO DETERMINE EXACT MEASUREMENTS OF SPACES OR ARTIFACTS FOUND HEREIN FOR ANY PURPOSE.	 RED BRIDGE DESIGN SAN FRANCISCO REDBRIDGEDESIGN.COM	
EXISTING BUILDING SECTIONS		
REF: 25sf-7_City_SFD REV: 0 DRAWN BY: MV AUDITED BY: TL	SHEET SIZE: 24x36 SCALE: 1/5"=1'-0" FIELD MEASURE: 10/10/22	AX-301 7 OF ##

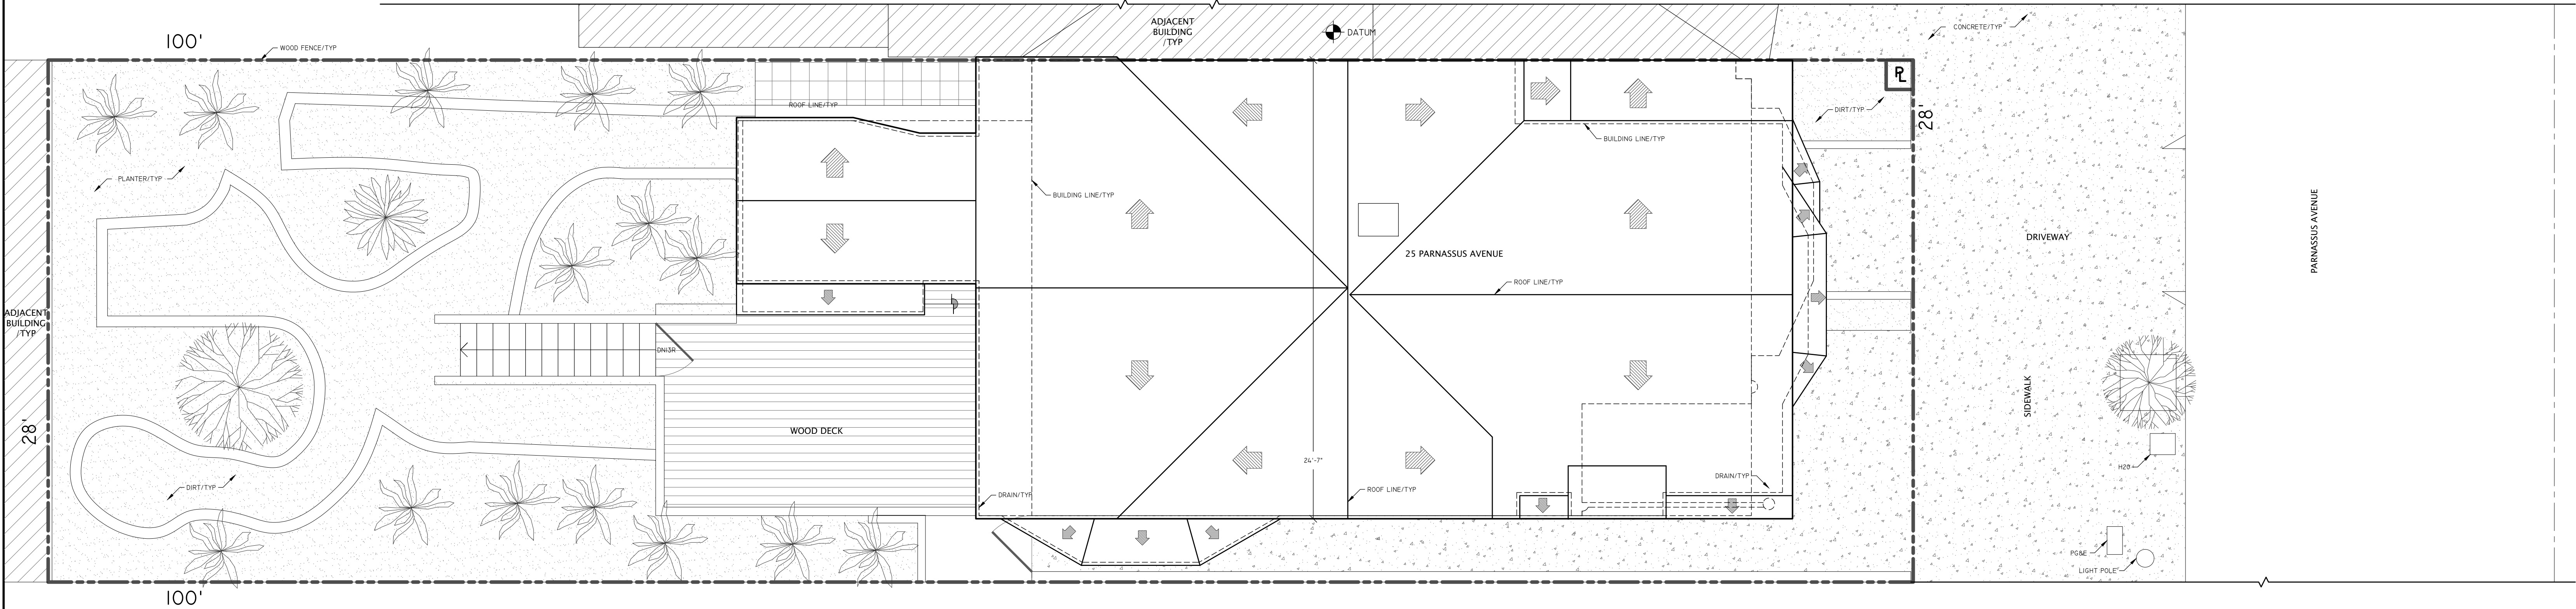

1 EXISTING LANDSCAPE SURVEY
2,800 SQFT (0.064 ACRE) SITE PLAN

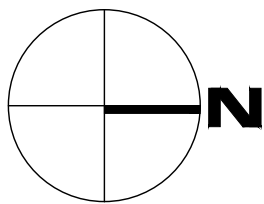

1.) THIS IS NOT A LAND SURVEY, PROPERTY LINES ARE NOT DETERMINED.
2.) PROPERTY LINES ARE COPIED FROM TAX ASSESSOR'S MAP. PLACEMENT ASSUMED.

25 PARNASSUS AVENUE
SAN FRANCISCO, CA 94117

THIS DRAWING IS A RECORD OF REAL PROPERTY THAT IS GENERALLY ACCEPTED TO BE SUITABLE FOR USE IN PLANNING, DESIGN, LEASE, AND GENERAL ASSET MANAGEMENT. IT SHOULD NOT BE USED TO DETERMINE EXACT MEASUREMENTS OF SPACES OR ARTIFACTS FOUND HEREIN FOR ANY PURPOSE.
EXTERIOR ELEMENTS HAVE BEEN MEASURED AND DRAFTED FOR REFERENCE ONLY - THIS IS NOT A SURVEY.



EXISTING LANDSCAPE SURVEY

REF: 25sf-7_City_SFD
REV: 0
DRAWN BY: MV
AUDITED BY: TL

SHEET SIZE: 24x36
SCALE: 1/4"=1'-0"
FIELD MEASURE:
10/10/22

AX-101
1 OF 7



OF 7