



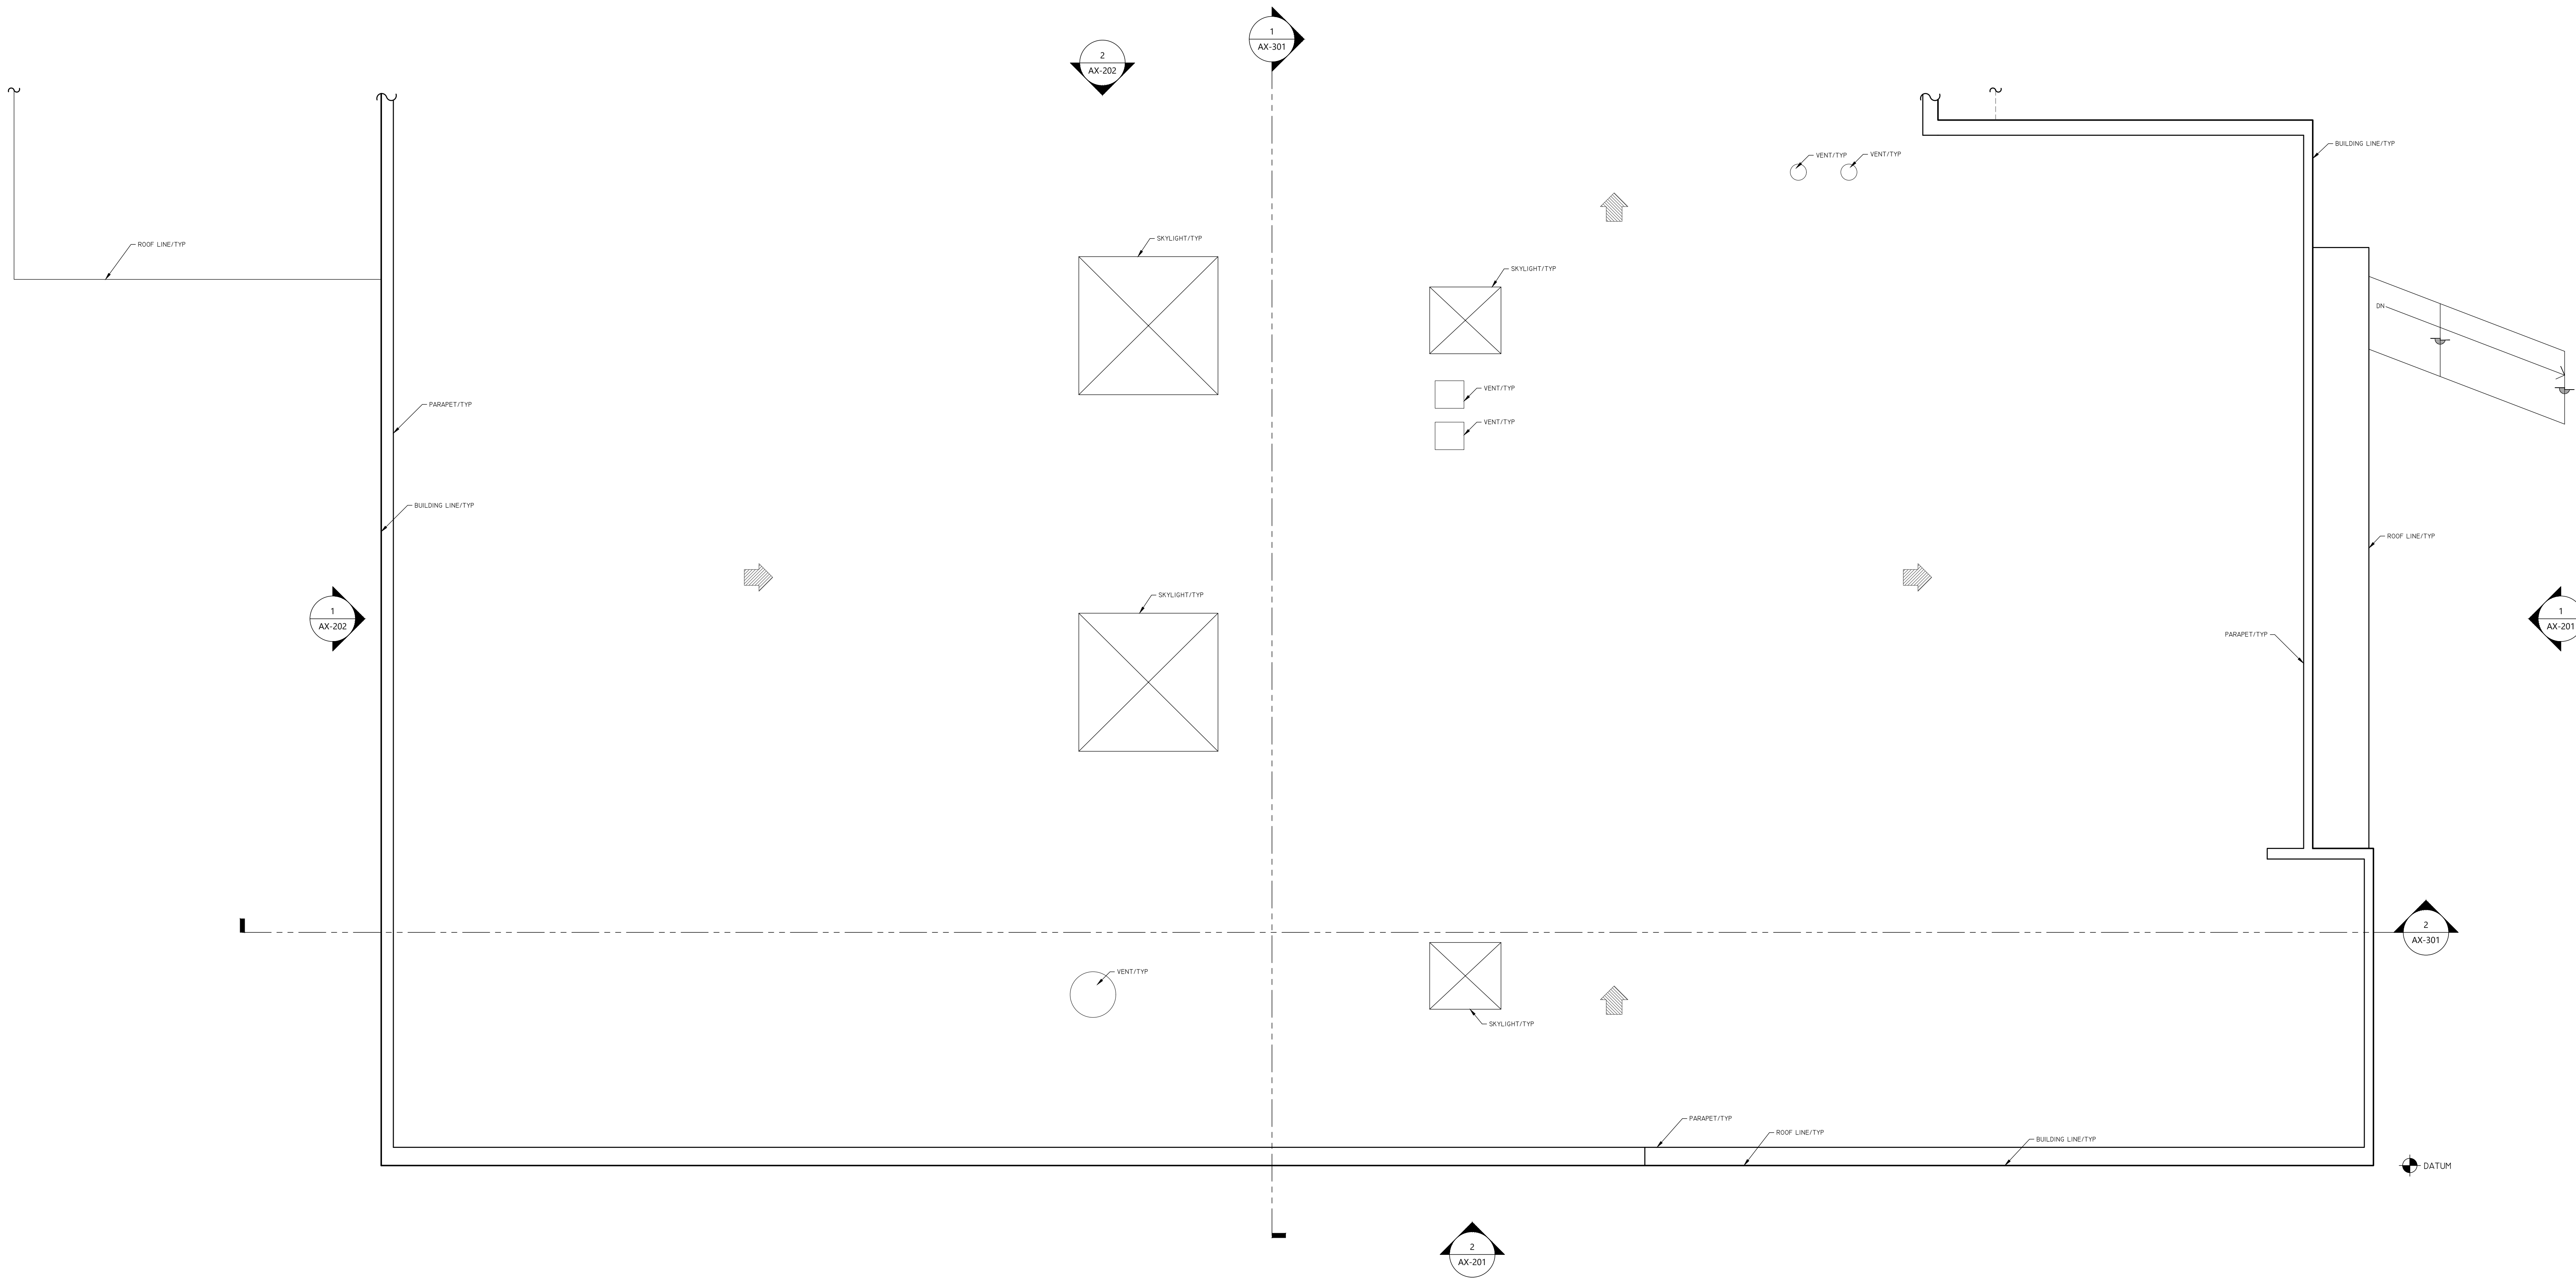

1 EXISTING ROOF PLAN
6,602 SQFT ROOF PLAN

DUE TO SAFETY CONCERNS, ROOF MEASUREMENTS TAKEN FROM STRUCTURE AND GRADE. DIMENSIONS TYPICAL.
GUTTERS AND DOWNSPOUTS NOT SHOWN, UNLESS NOTED OTHERWISE.

1500 BURKE AVENUE, UNIT C SAN FRANCISCO, CA 94124		
THIS DRAWING IS A RECORD OF REAL PROPERTY THAT IS GENERALLY ACCEPTED TO BE SUITABLE FOR USE IN PLANNING, DESIGN, LEASE, AND GENERAL ASSET MANAGEMENT. IT SHOULD NOT BE USED TO DETERMINE EXACT MEASUREMENTS OF SPACES OR ARTIFACTS FOUND HEREIN FOR ANY PURPOSE. EXTERIOR ELEMENTS HAVE BEEN MEASURED AND DRAFTED FOR REFERENCE ONLY - THIS IS NOT A SURVEY.		
 RED BRIDGE DESIGN SAN FRANCISCO REDBRIDGEDESIGN.COM		
EXISTING ROOF PLAN		
REF: 1500sf_City.COM REV: 0 DRAWN BY: MV AUDITED BY: JK	SHEET SIZE: 30x42 SCALE: 1/4"=1'-0" FIELD MEASURE: 11/13/20	AX-101 1 OF 6

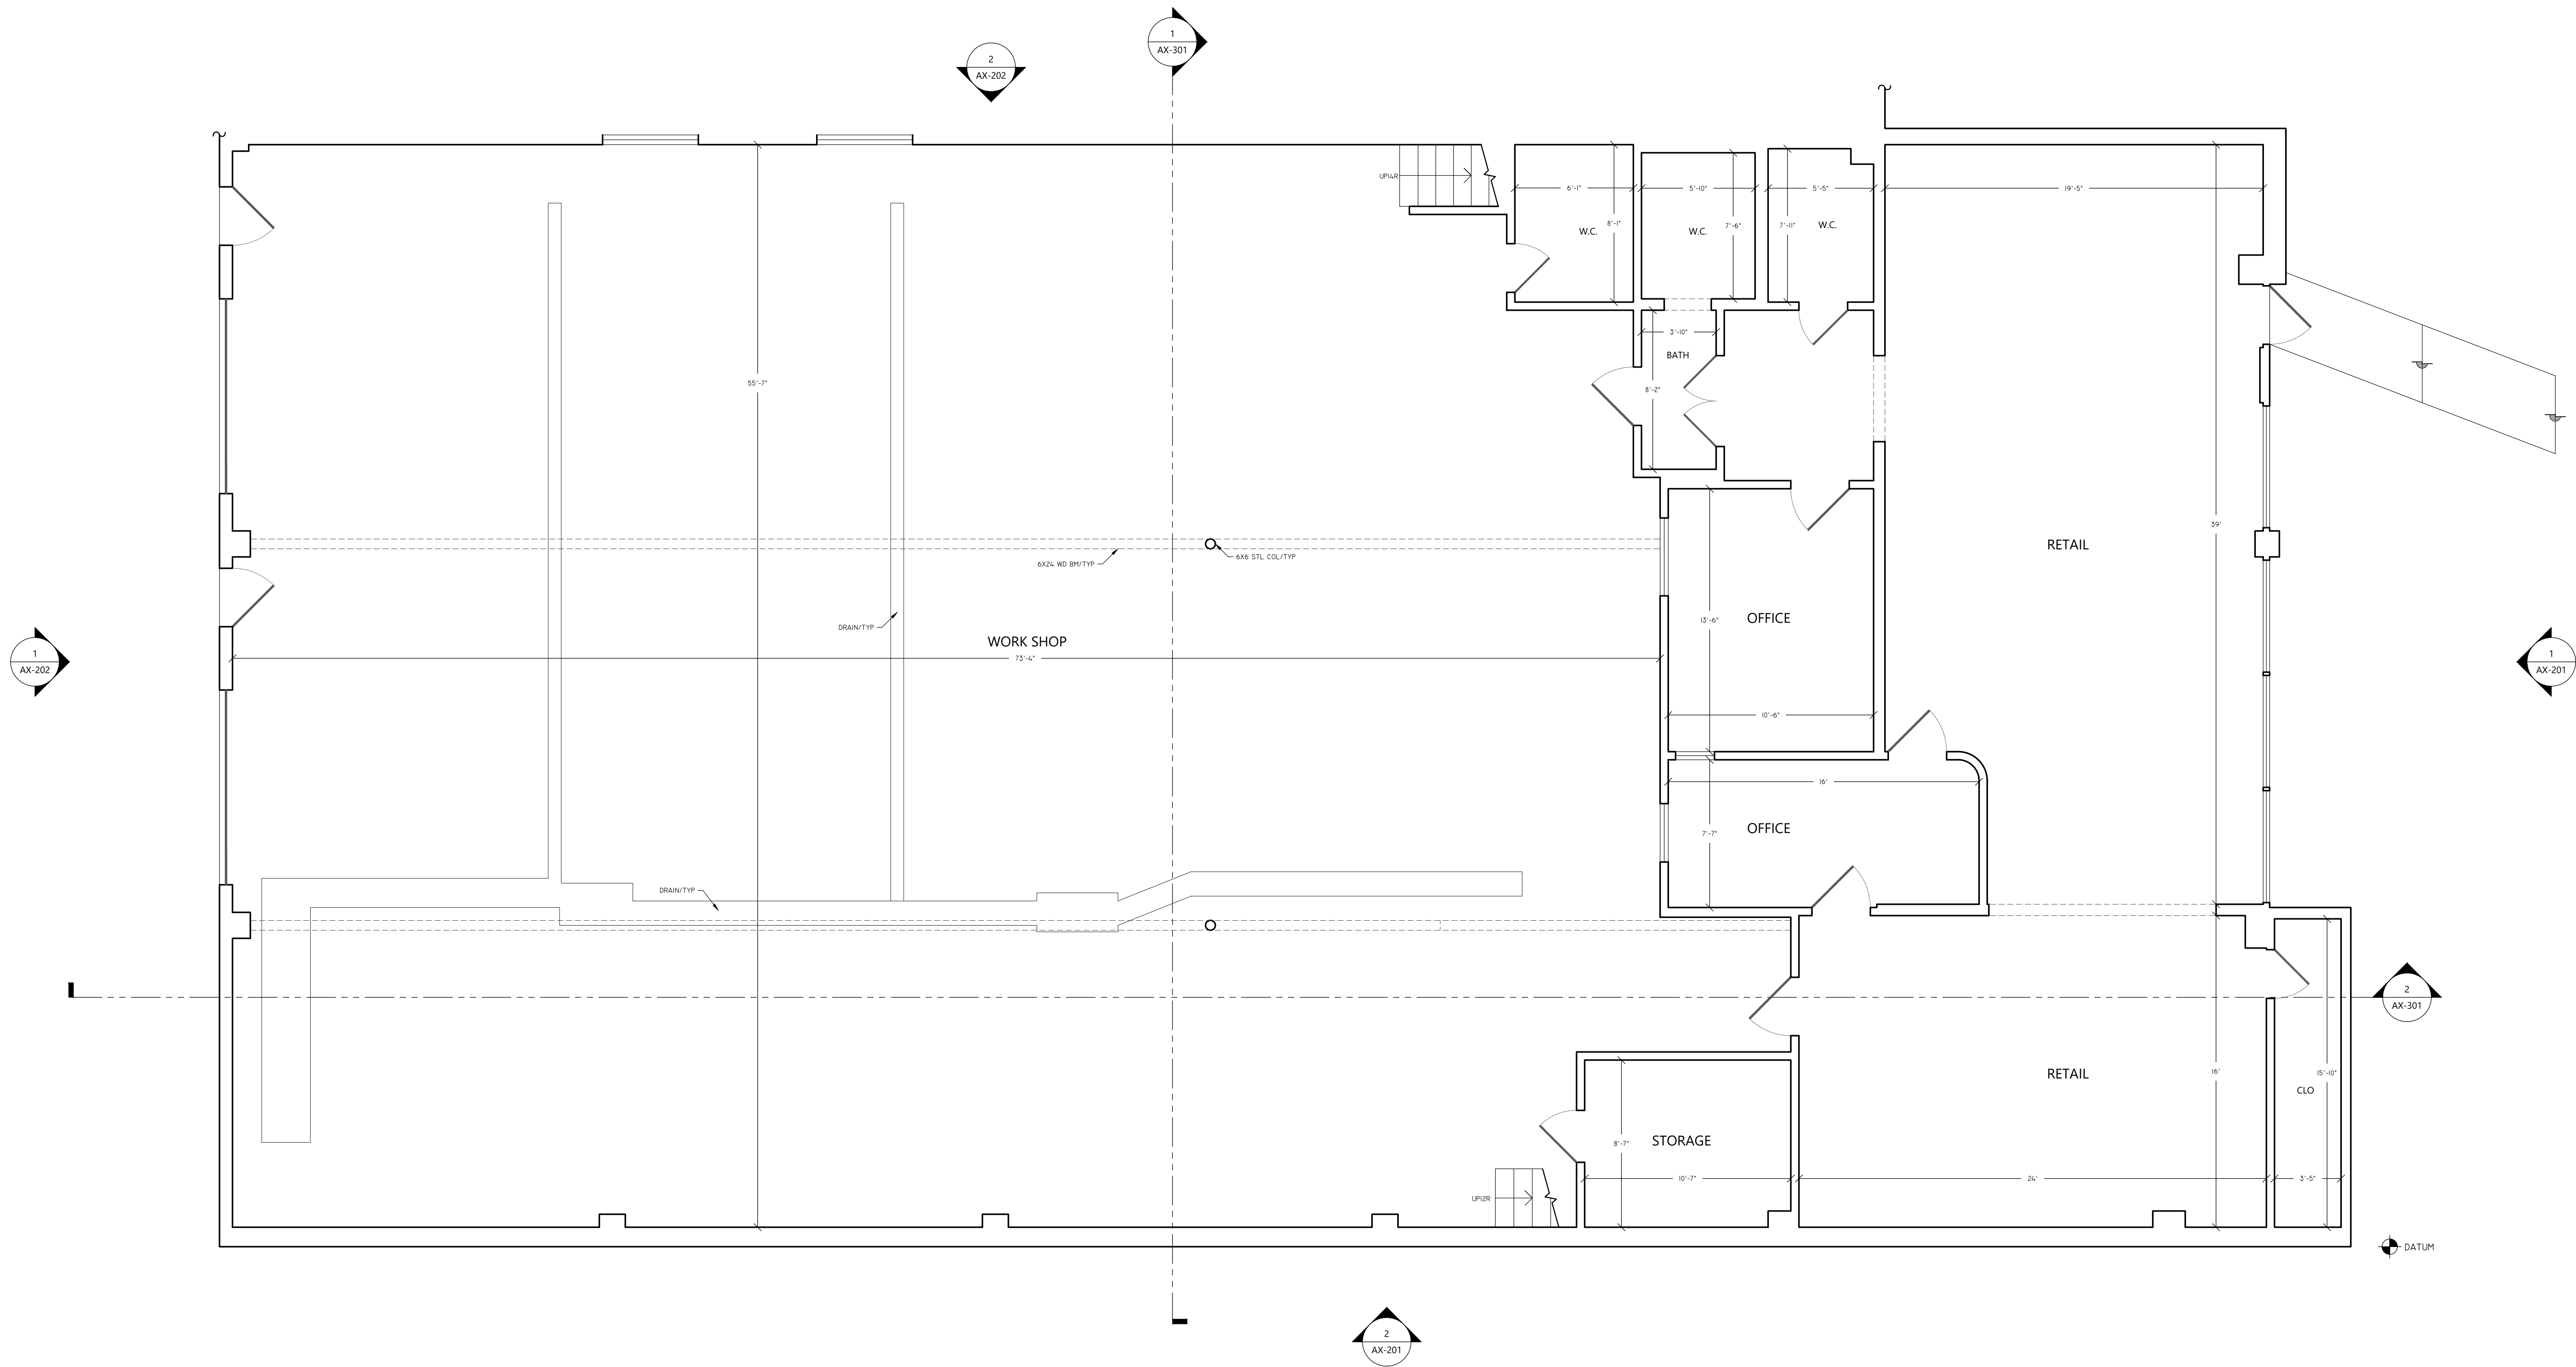

1 EXISTING ENTRY LEVEL FLOOR PLAN
6,095 SQFT GROSS MEASURED AREA
58 SQFT MEASURED EXTERIOR SURFACES

THESE ARE BASIC FLOOR PLANS. NO INTERIOR ELEMENTS SHOWN,
UNLESS NOTED OTHERWISE.

1500 BURKE AVENUE, UNIT C
SAN FRANCISCO, CA 94124

THIS DRAWING IS A RECORD OF REAL PROPERTY THAT
IS GENERALLY ACCEPTED TO BE SUITABLE FOR USE IN
PLANNING, DESIGN, LEASE, AND GENERAL ASSET
MANAGEMENT. IT SHOULD NOT BE USED TO
DETERMINE EXACT MEASUREMENTS OF SPACES OR
ARTIFACTS FOUND HEREIN FOR ANY PURPOSE.
EXTERIOR ELEMENTS HAVE BEEN MEASURED AND
DRAFTED FOR REFERENCE ONLY - THIS IS NOT A
SURVEY.




EXISTING FLOOR PLAN

REF: 1500sf_City.COM
REV: 0
DRAWN BY: MV
AUDITED BY: JK

SHEET SIZE: 30x42
SCALE: 1/4"=1'-0"
FIELD MEASURE:
11/13/20

AX-102
2 OF 6

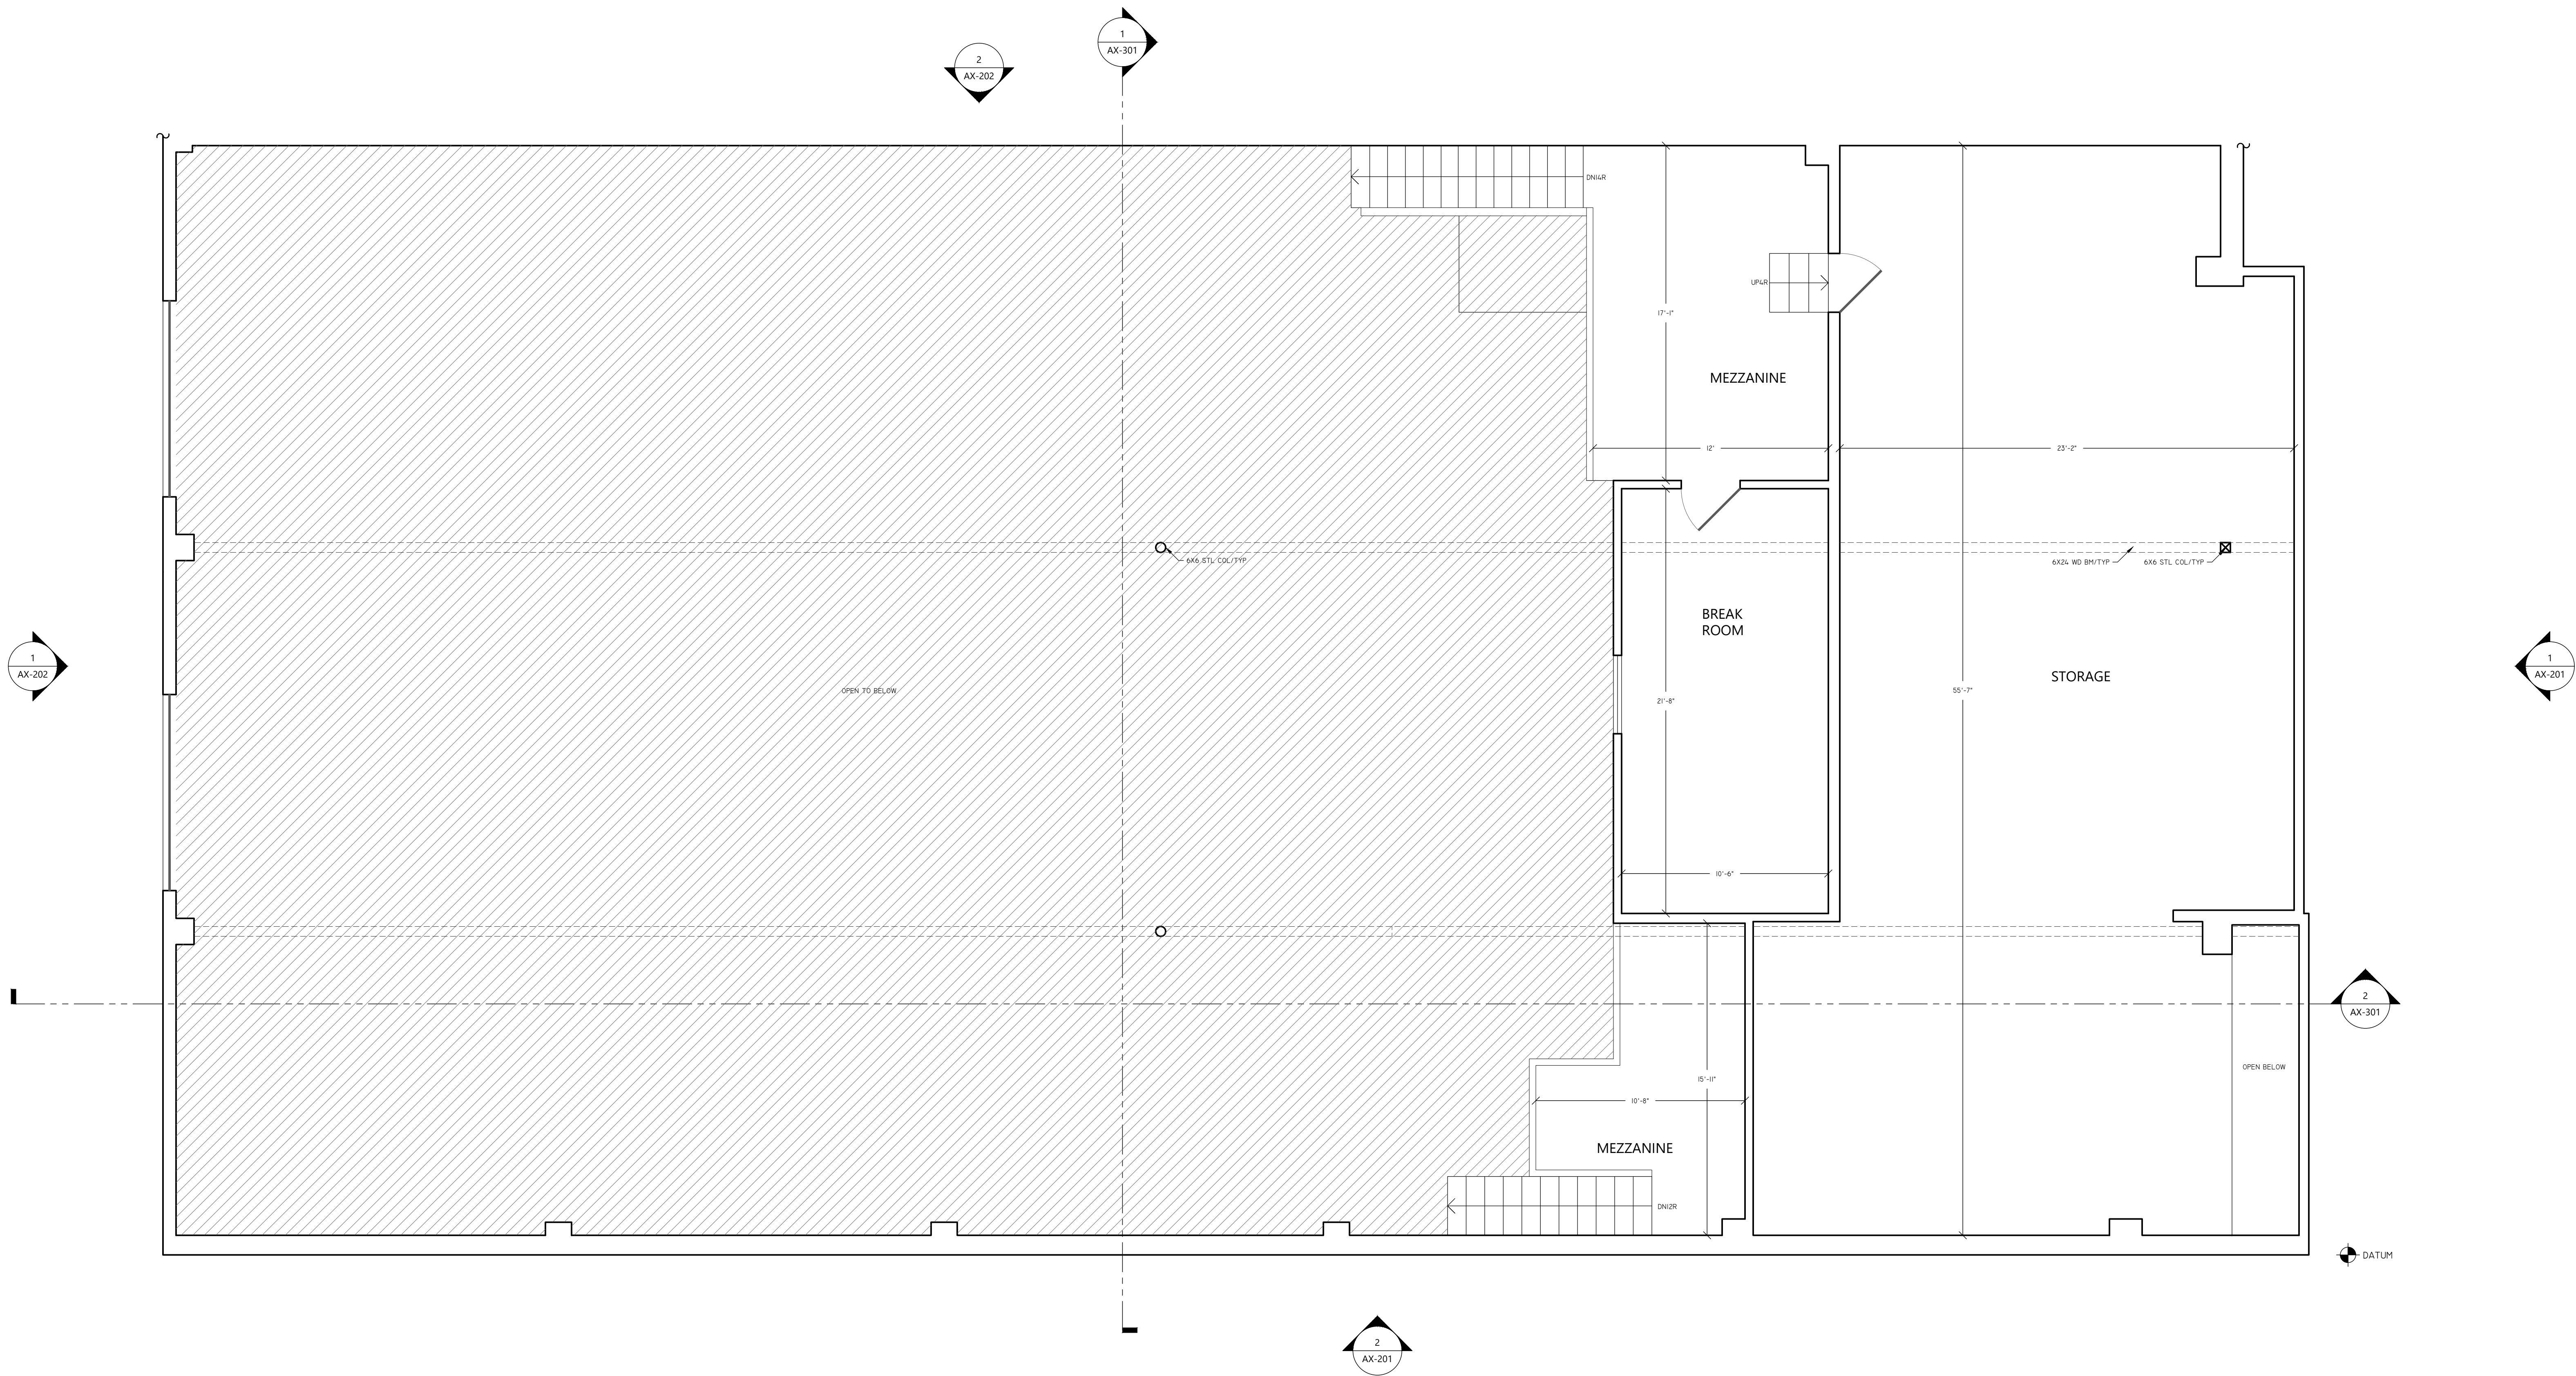

1 EXISTING SECOND LEVEL FLOOR PLAN
2,103 SQFT GROSS MEASURED AREA

THESE ARE BASIC FLOOR PLANS. NO INTERIOR ELEMENTS SHOWN,
UNLESS NOTED OTHERWISE.

1500 BURKE AVENUE, UNIT C
SAN FRANCISCO, CA 94124

THIS DRAWING IS A RECORD OF REAL PROPERTY THAT
IS GENERALLY ACCEPTED TO BE SUITABLE FOR USE IN
PLANNING, DESIGN, LEASE, AND GENERAL ASSET
MANAGEMENT. IT SHOULD NOT BE USED TO
DETERMINE EXACT MEASUREMENTS OF SPACES OR
ARTIFACTS FOUND HEREIN FOR ANY PURPOSE.




EXTERIOR ELEMENTS HAVE BEEN MEASURED AND
DRAFTED FOR REFERENCE ONLY - THIS IS NOT A
SURVEY.

EXISTING FLOOR PLAN


REF: 1500sf_City.COM
REV: 0
DRAWN BY: MV
AUDITED BY: JK

SHEET SIZE: 30x42
SCALE: 1/4"=1'-0"
FIELD MEASURE:
11/13/20

AX-103
3 OF 6

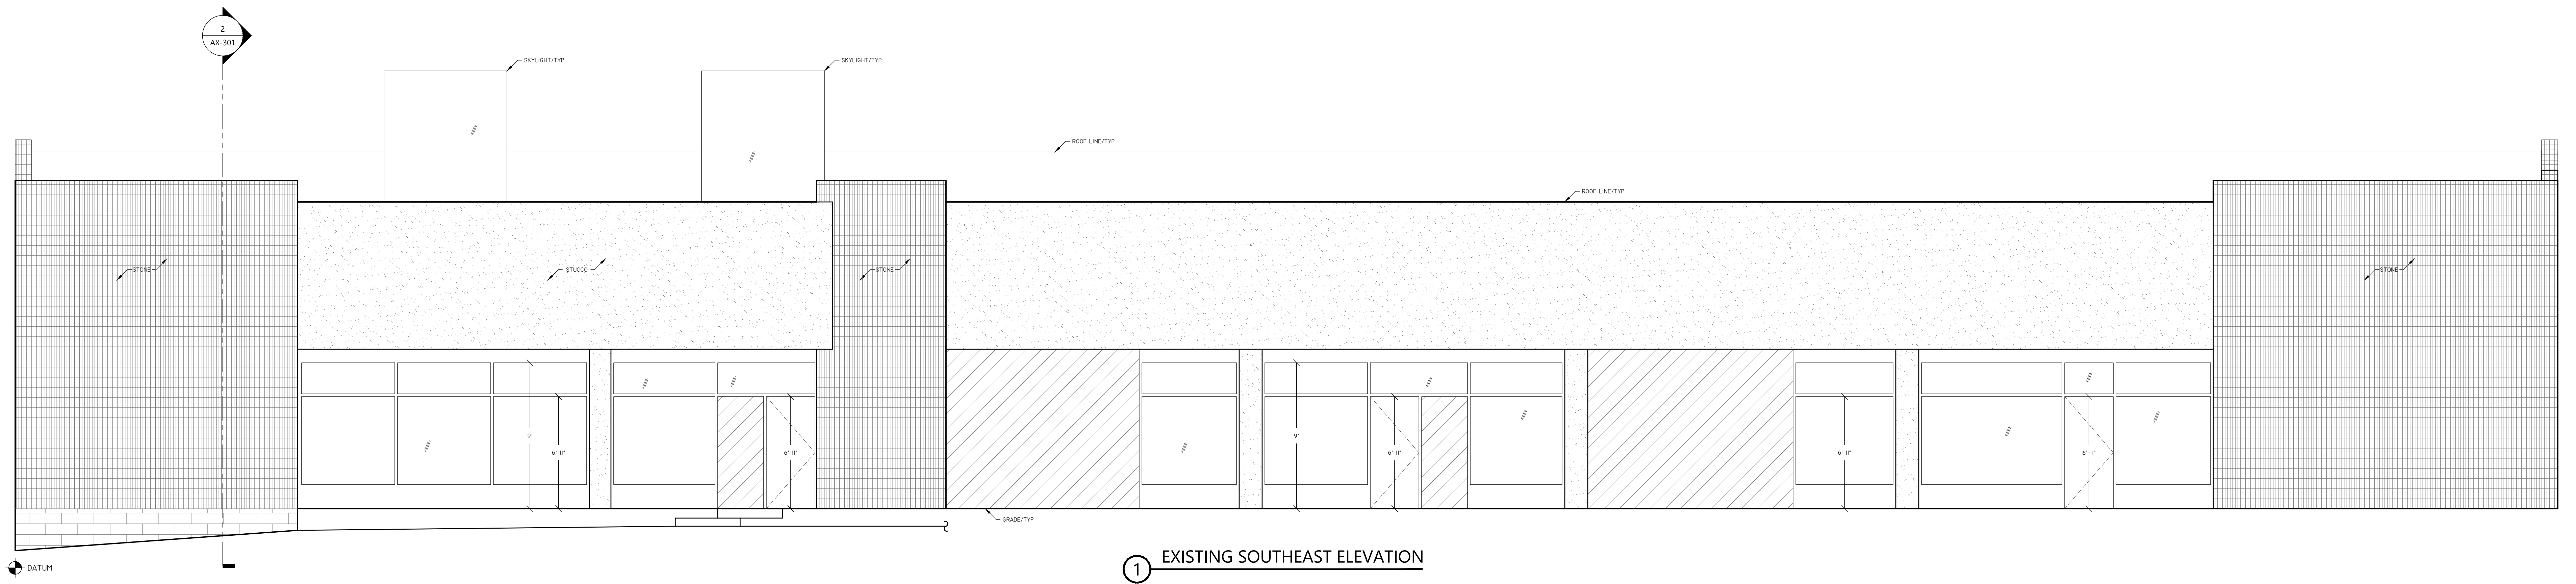

1 EXISTING SOUTHEAST ELEVATION

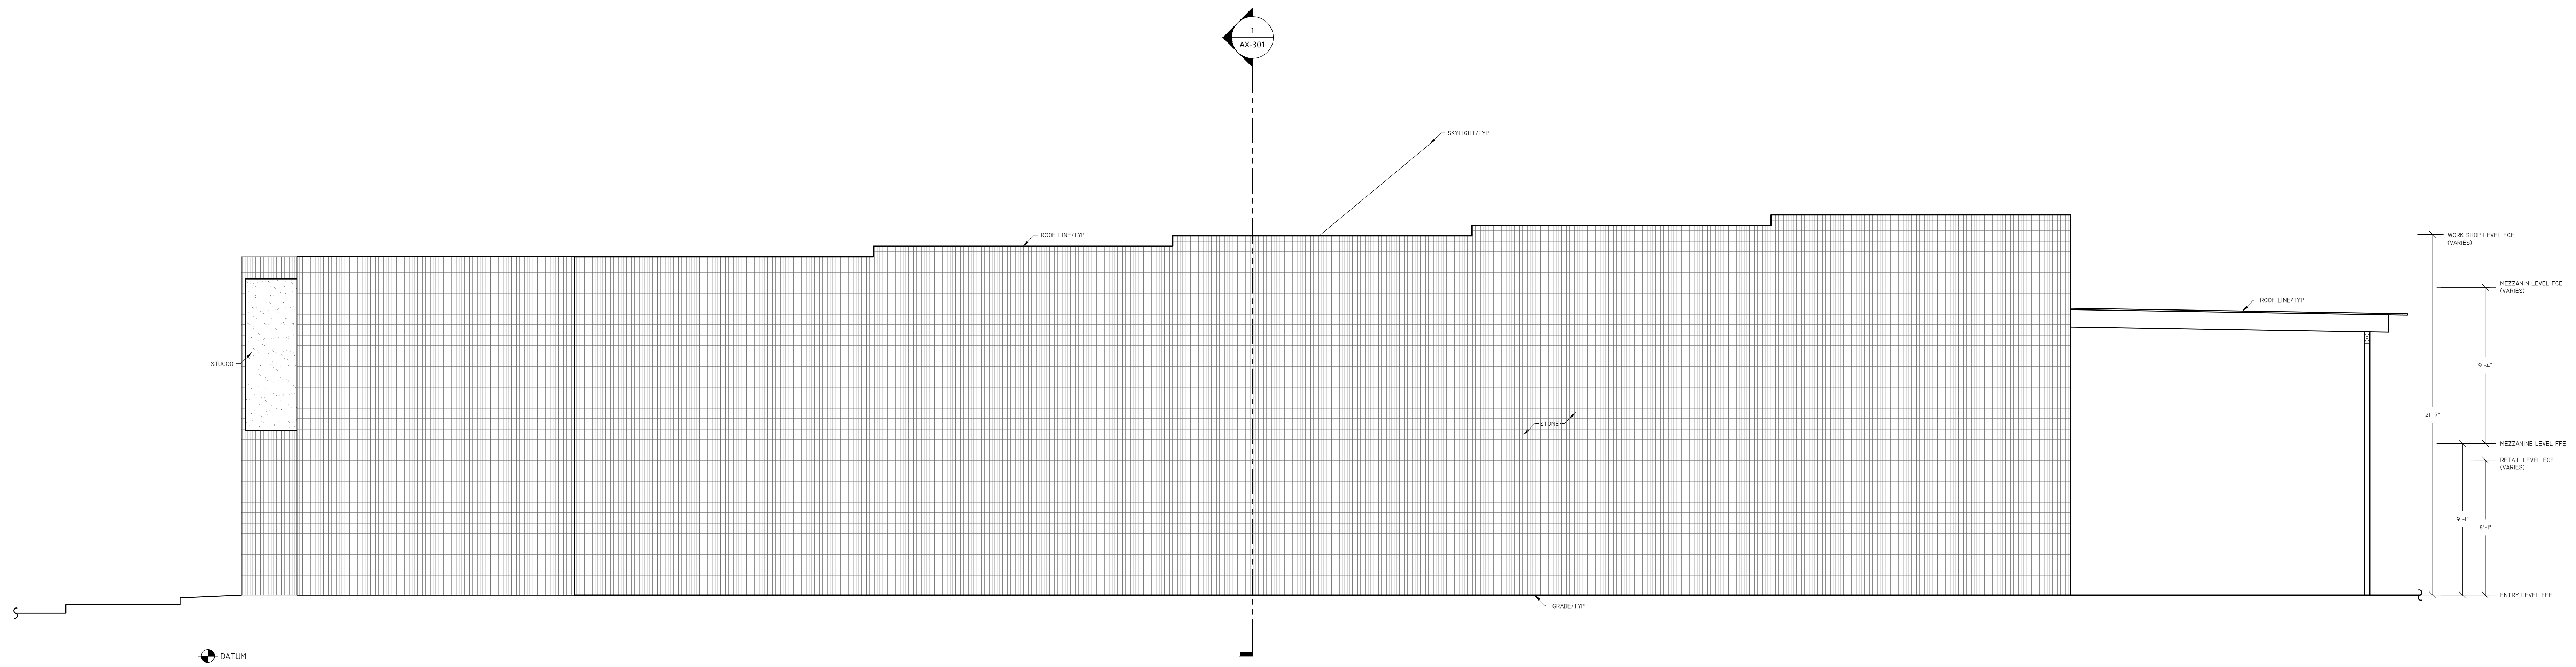

2 EXISTING SOUTHWEST ELEVATION

THESE ARE BASIC ELEVATIONS.
NO BUILDING ORNAMENTATION SHOWN.

1500 BURKE AVENUE, UNIT C
SAN FRANCISCO, CA 94124

THIS DRAWING IS A RECORD OF REAL PROPERTY THAT IS GENERALLY ACCEPTED TO BE SUITABLE FOR USE IN PLANNING, DESIGN, LEASE AND GENERAL ASSET MANAGEMENT. IT SHOULD NOT BE USED TO DETERMINE EXACT MEASUREMENTS OF SPACES OR ARCHITECTS' RECORD HEREIN FOR ANY PURPOSES. EXTERIOR ELEMENTS HAVE BEEN MEASURED AND DRAFTED FOR REFERENCE ONLY - THIS IS NOT A SURVEY.




EXISTING EXTERIOR ELEVATIONS

REF: 1500d_City.COM
REV: 0
DRAWN BY: MV
AUDITED BY: JK

SHEET SIZE: 30x42
SCALE: 1/4"=1'-0"
FIELD MEASURE:
11/13/20

AX-201
4 OF 6

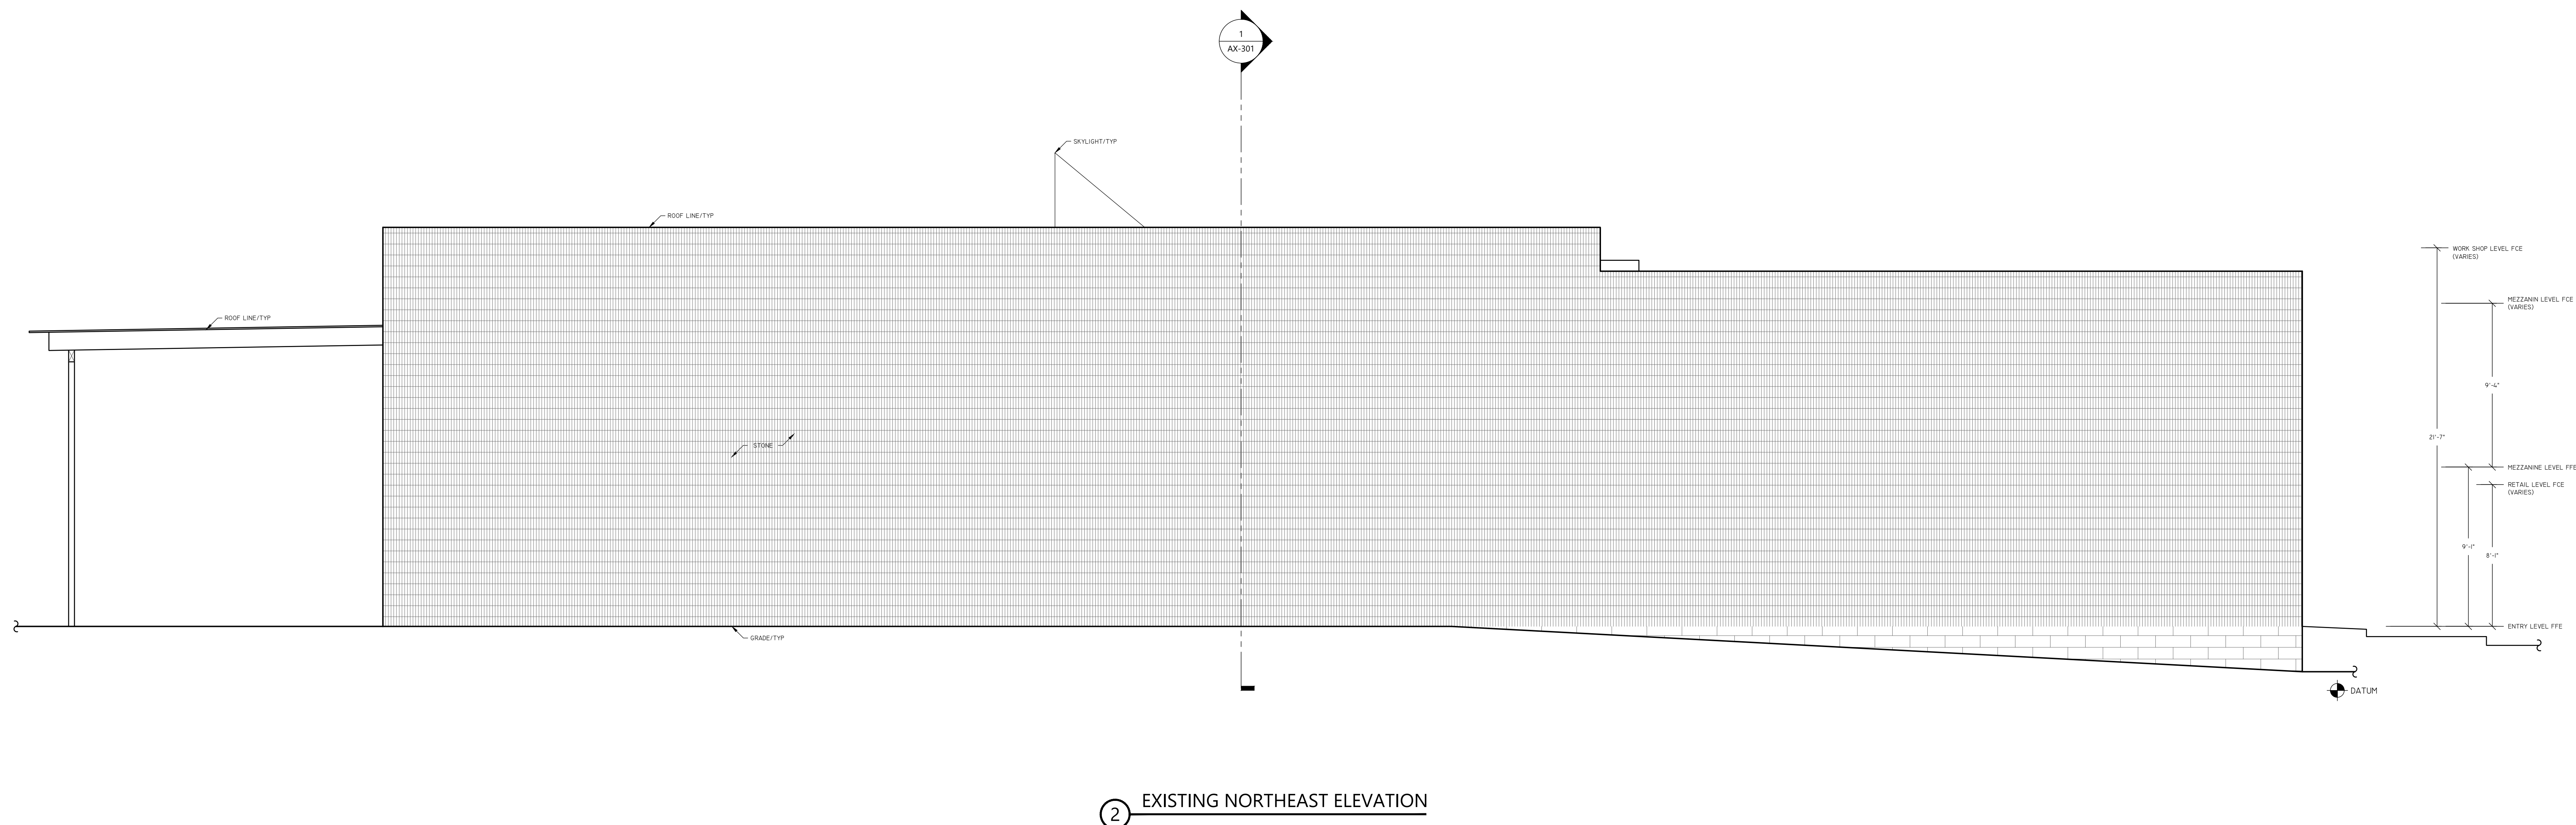

THESE ARE BASIC ELEVATIONS.
NO BUILDING ORNAMENTATION SHOWN.

1500 BURKE AVENUE, UNIT C
SAN FRANCISCO, CA 94124

THIS DRAWING IS A RECORD OF REAL PROPERTY THAT IS GENERALLY ACCEPTED TO BE SUITABLE FOR USE IN PLANNING, DESIGN, LEASE AND GENERAL ASSET MANAGEMENT. IT SHOULD NOT BE USED TO DETERMINE EXACT MEASUREMENTS OF SPACES OR ARTIFACTS FOUND HEREIN FOR ANY PURPOSES.




EXISTING EXTERIOR ELEVATIONS


REF: 1500d_City.COM
REV: 0
DRAWN BY: MV
AUDITED BY: JK

SHEET SIZE: 30x42
SCALE: 1/4"=1'-0"
FIELD MEASURE:
11/13/20

AX-201
5 OF 6

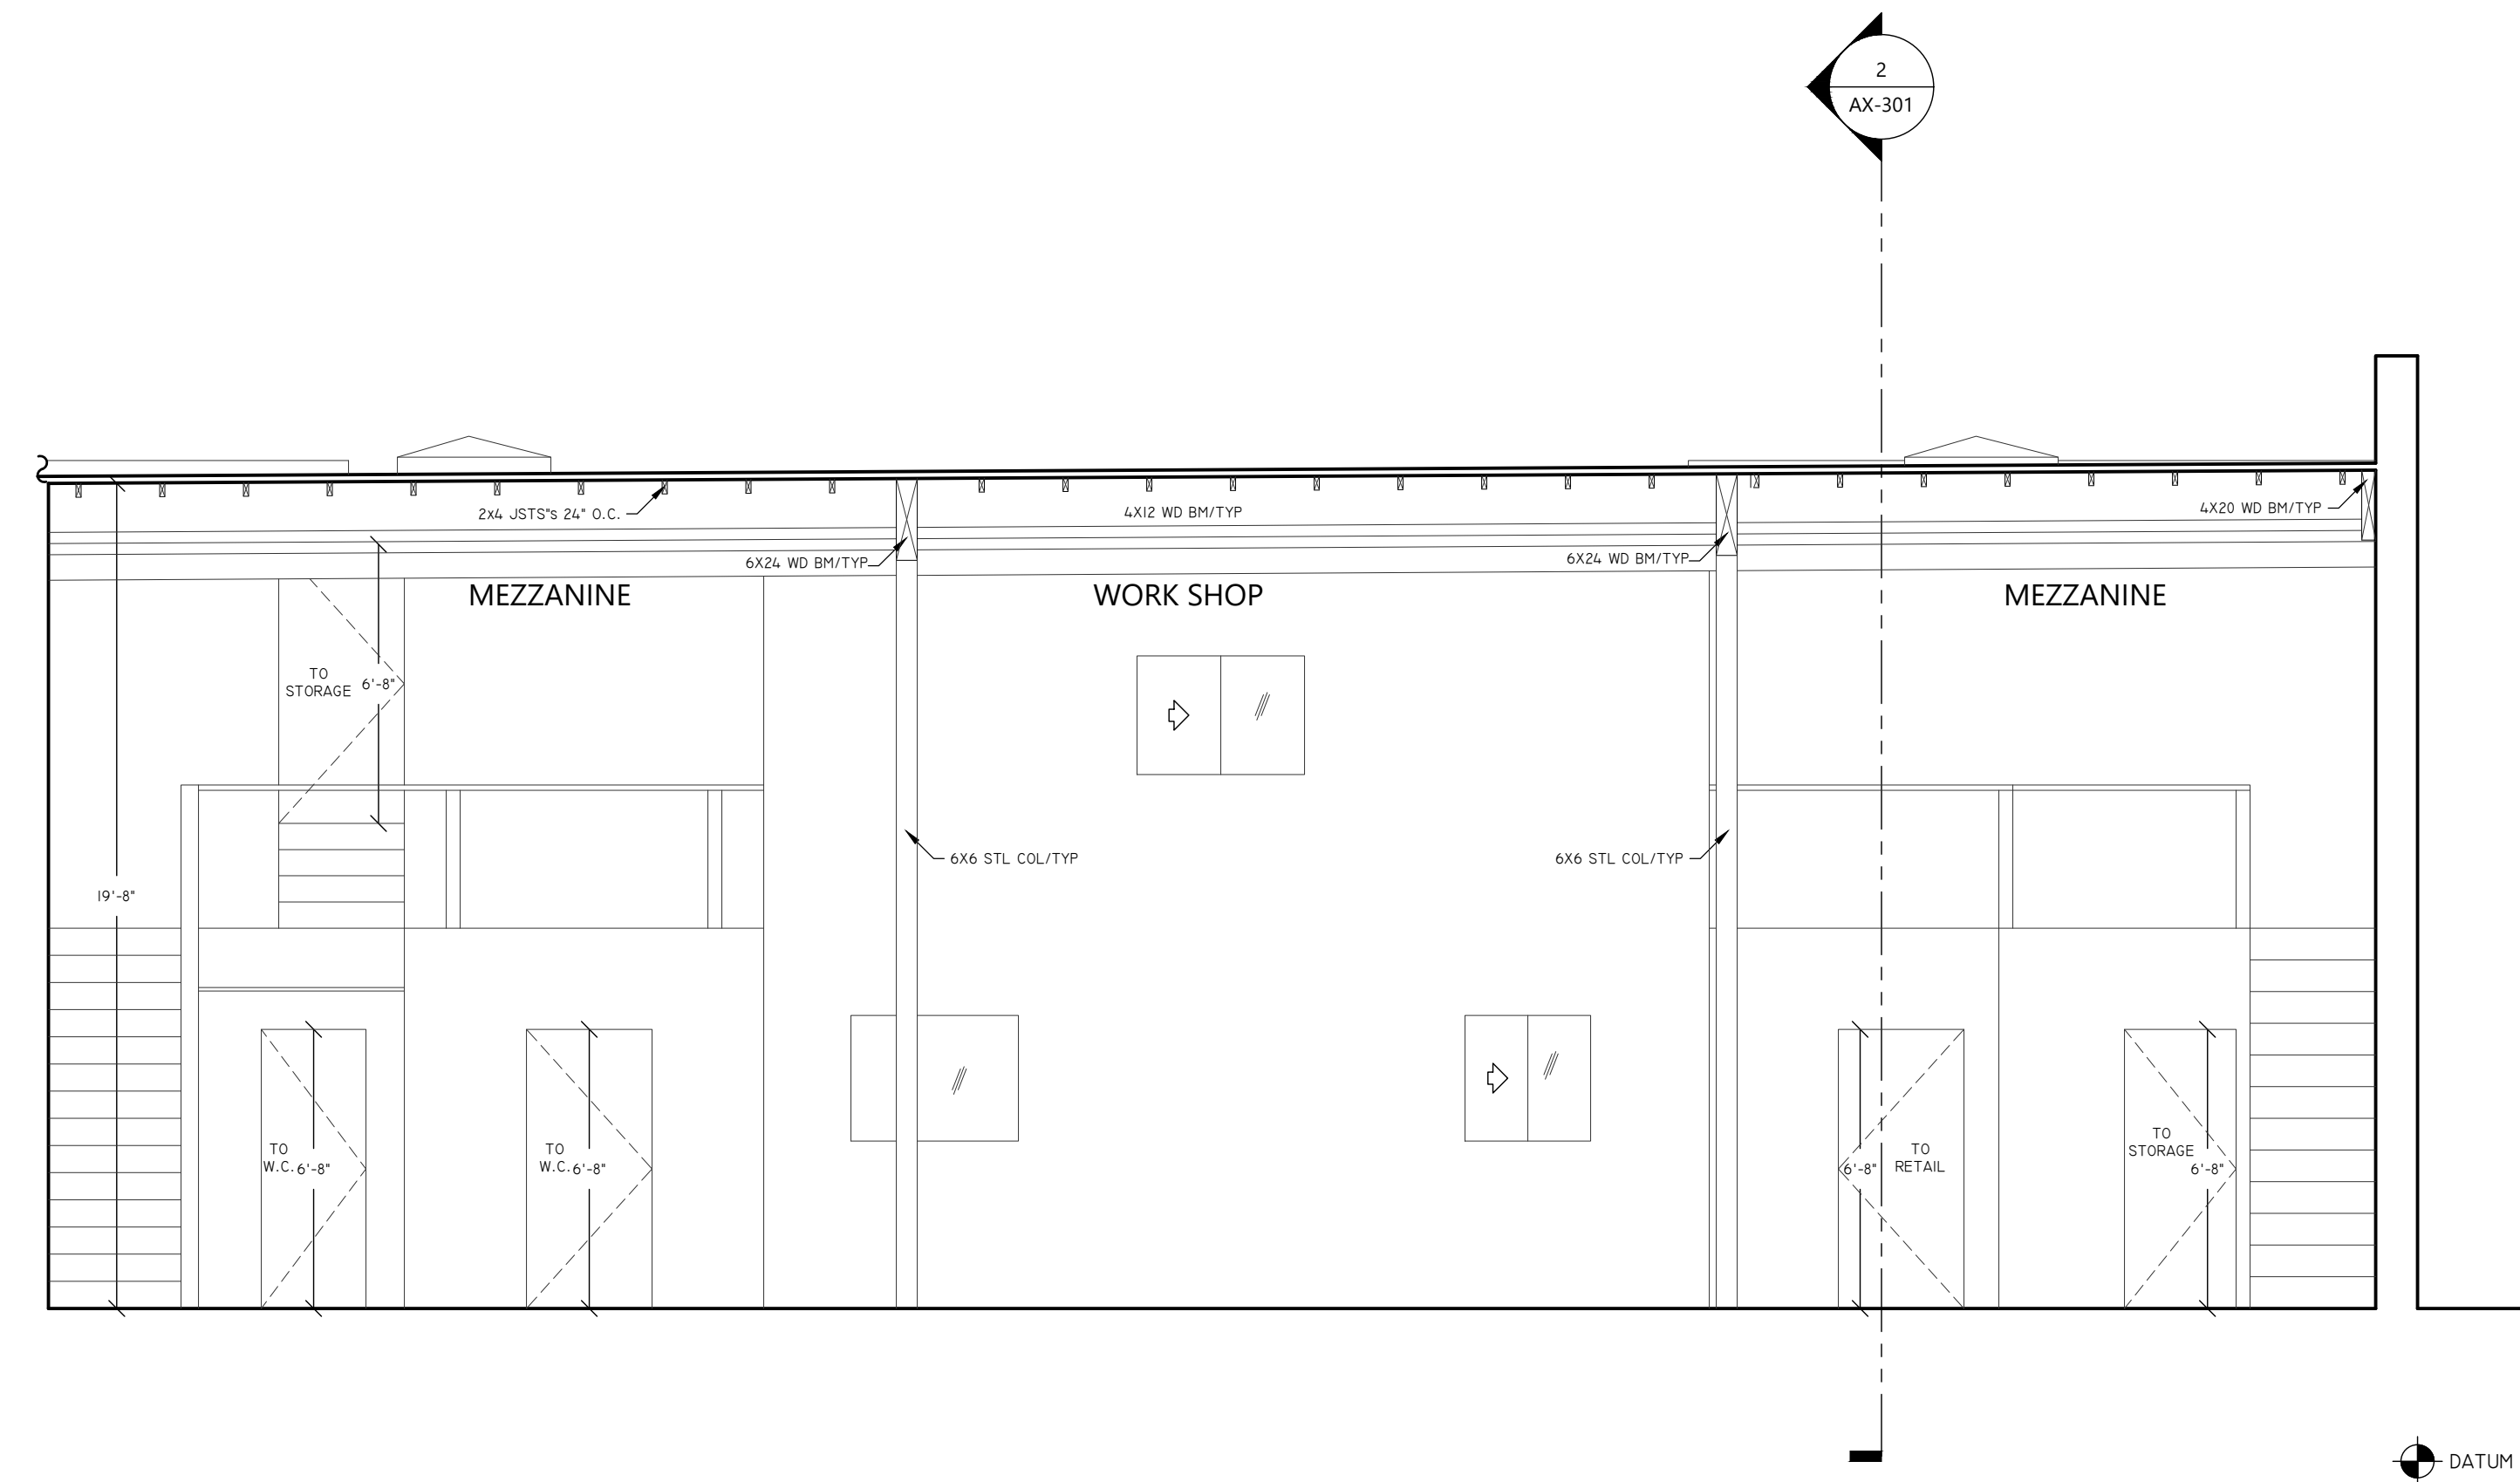

1 EXISTING CROSS SECTION

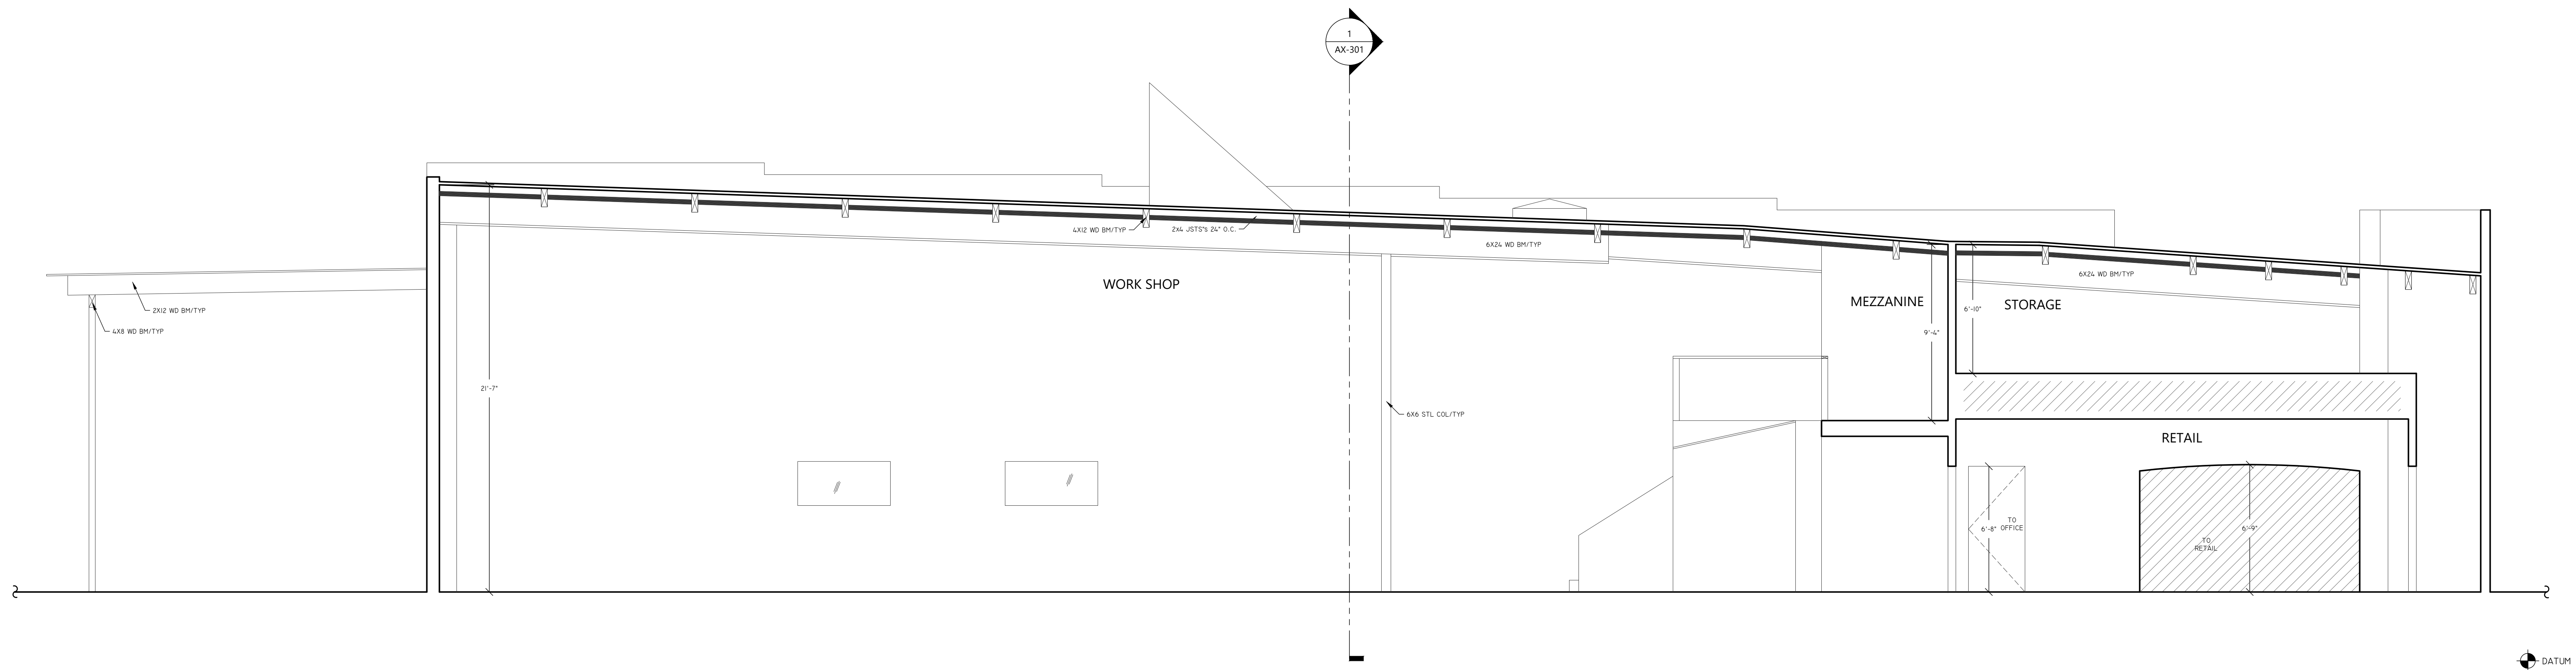

1 EXISTING LONGITUDINAL SECTION

1500 BURKE AVENUE, UNIT C
SAN FRANCISCO, CA 94124

THIS DRAWING IS A RECORD OF REAL PROPERTY THAT
IS GENERALLY ACCEPTED TO BE SUITABLE FOR USE IN
PLANNING, DESIGN, LEASE AND GENERAL ASSET
MANAGEMENT. IT SHOULD NOT BE USED TO
DETERMINE EXACT MEASUREMENTS OF SPACES OR
ARTIFACTS FOUND HEREIN FOR ANY PURPOSE.



EXISTING BUILDING SECTIONS

REF: 1500sf_City.COM
REV: 0
DRAWN BY: MV
AUDITED BY: JK

SHEET SIZE: 30x42
SCALE: 1/4"=1'-0"
FIELD MEASURE:
11/13/20

AX-301
6 OF 6