


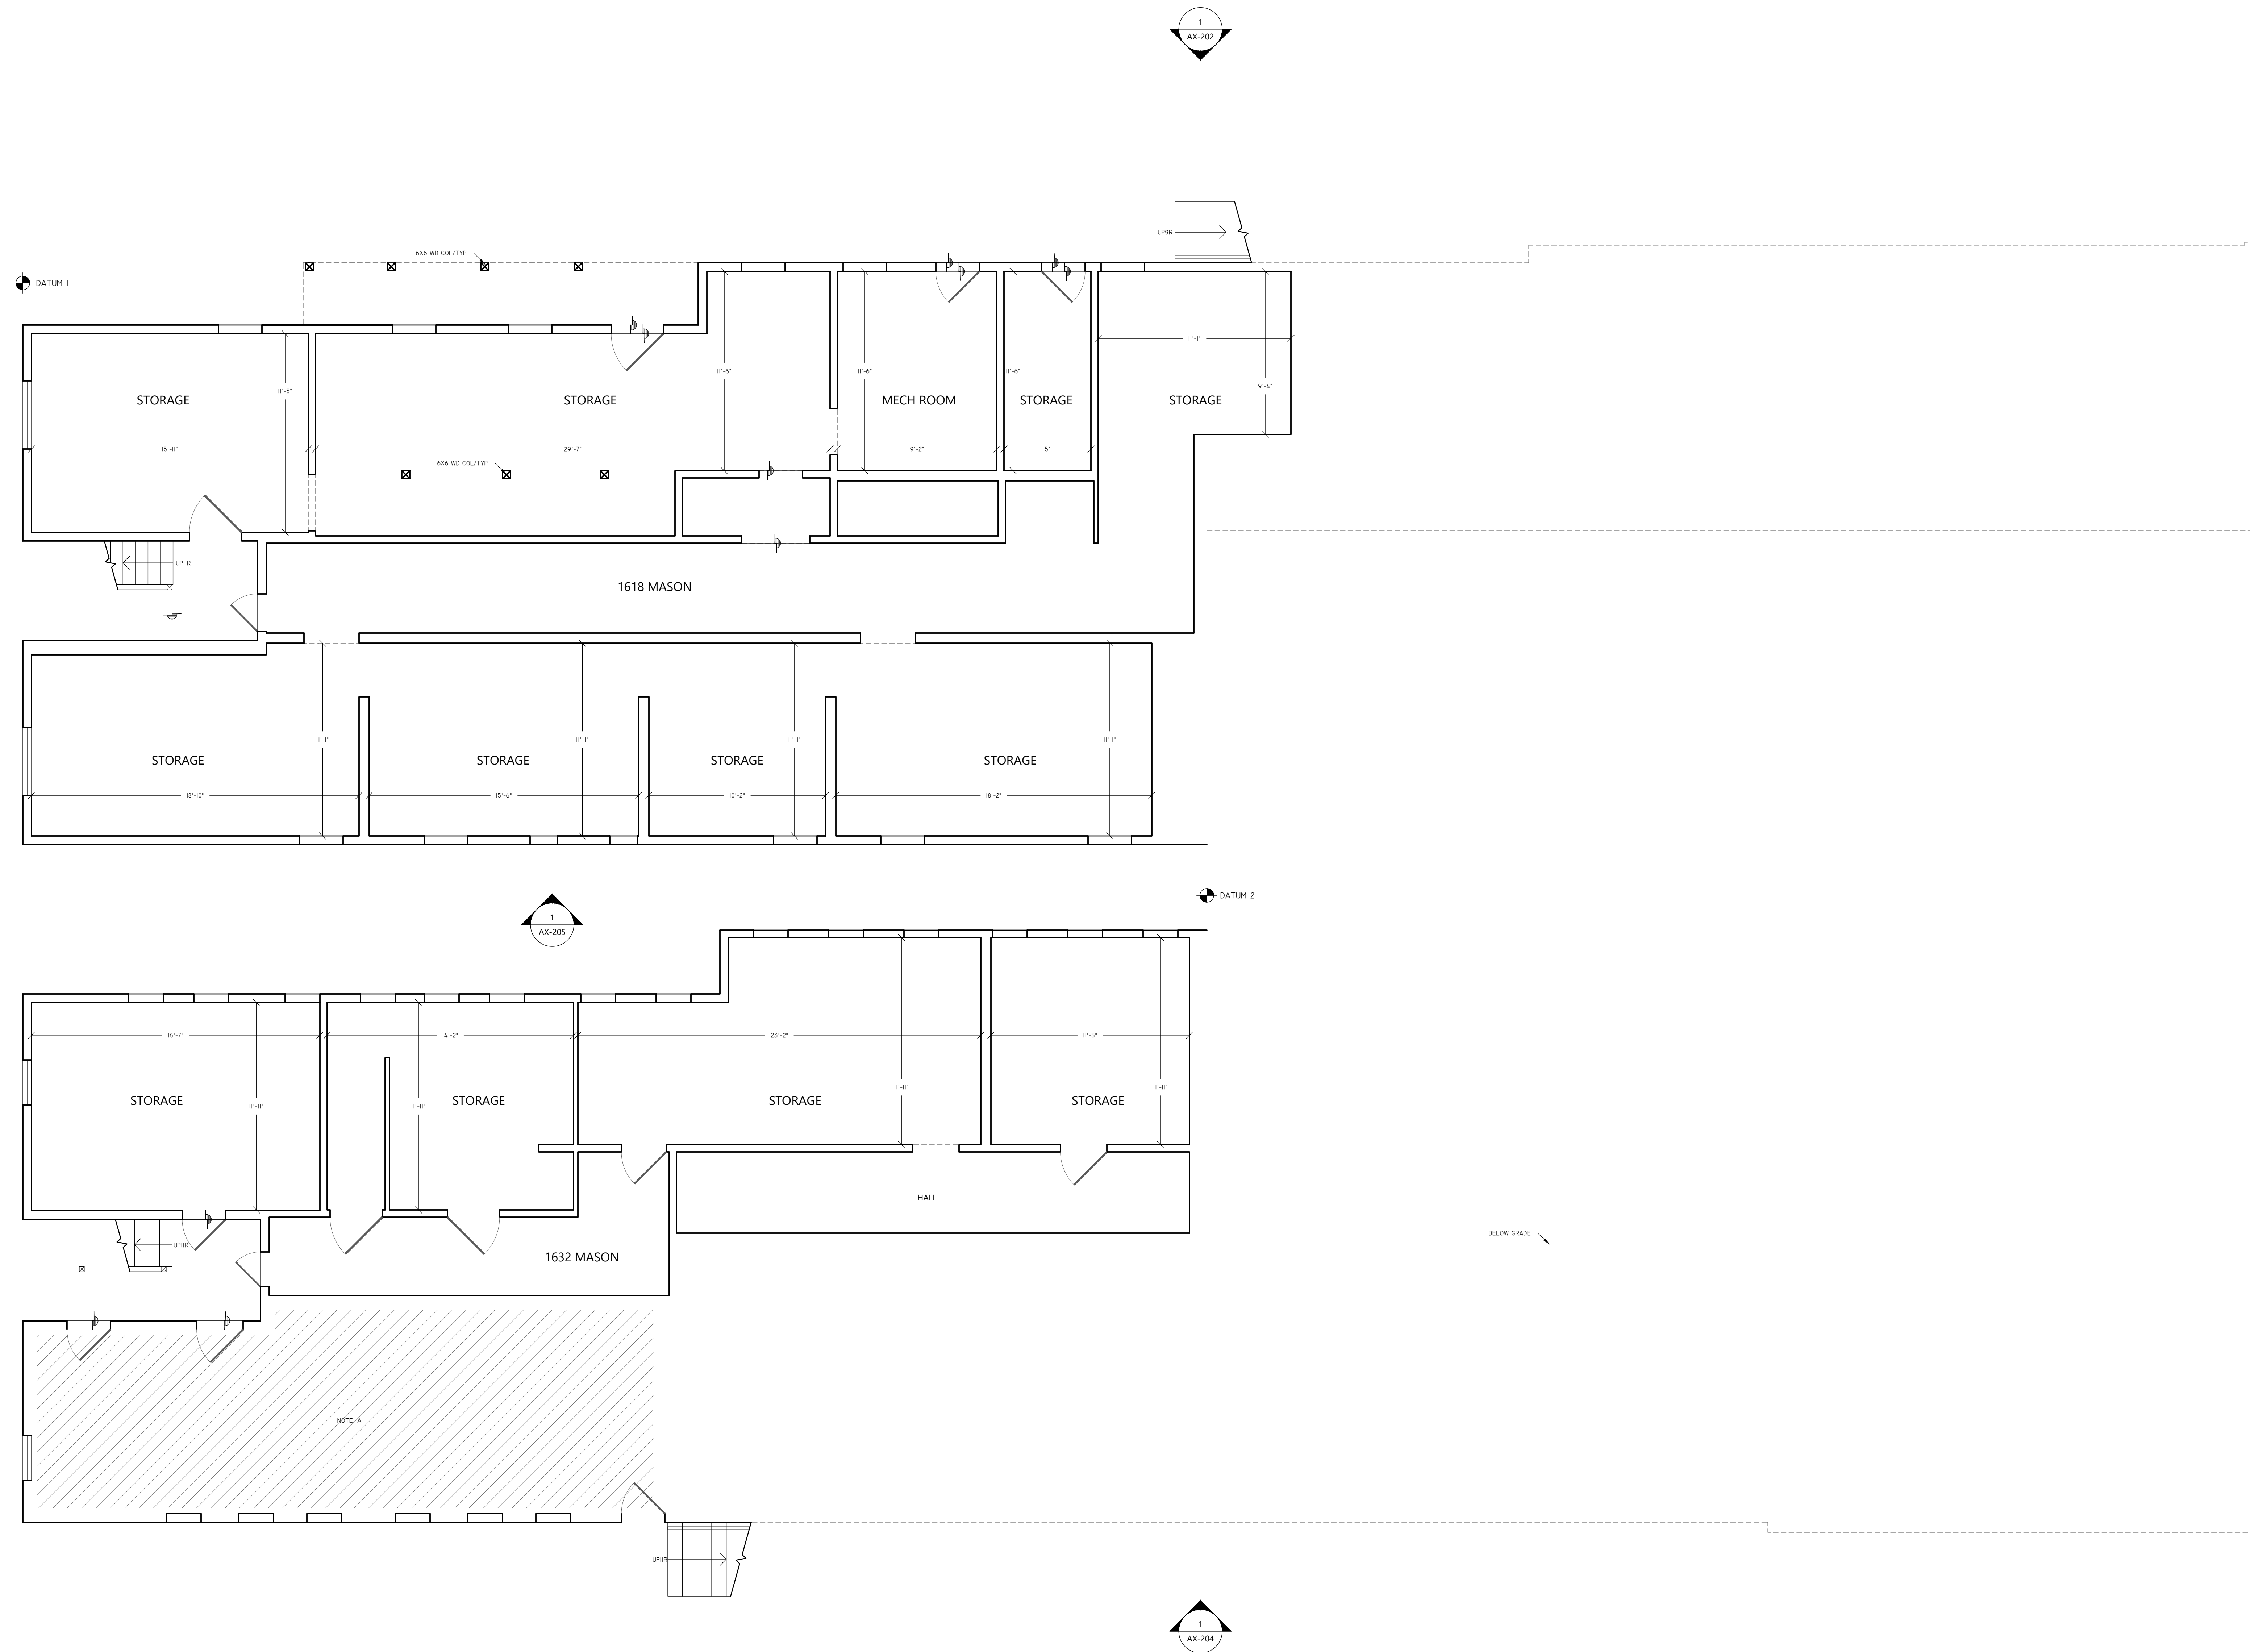


1 EXISTING BASEMENT LEVEL FLOOR PLAN  
3,221 SQFT GROSS MEASURED AREA

THESE ARE BASIC FLOOR PLANS. NO INTERIOR ELEMENTS SHOWN, UNLESS NOTED OTHERWISE.

NOTE A:  
THIS AREA NOT ACCESSIBLE AT TIME OF DATA ACQUISITION, AREA NOT MEASURED.

|   |                                                                       |
|---|-----------------------------------------------------------------------|
| 1618-1632 MASON STREET<br>SAN FRANCISCO, CA 94133   |                                                                       |
| <small>THIS DRAWING IS A RECORD OF REAL PROPERTY THAT IS GENERALLY ACCEPTED TO BE SUITABLE FOR USE IN PLANNING, DESIGN, LEASE AND GENERAL ASSET MANAGEMENT. IT SHOULD NOT BE USED TO DETERMINE EXACT MEASUREMENTS OF SPACES OR ARTIFACTS FOUND HEREIN FOR ANY PURPOSE.</small> |                                                                       |
| <small>EXTERIOR ELEMENTS HAVE BEEN MEASURED AND DRAFTED FOR REFERENCE ONLY - THIS IS NOT A SURVEY.</small>   |                                                                       |
| RED BRIDGE DESIGN<br>SAN FRANCISCO<br>REDBRIDGEDESIGN.COM   |                                                                       |
| EXISTING FLOOR PLAN   |                                                                       |
| REF: 1618-1632sf_City_MFD<br>REV: 0<br>DRAWN BY: MM<br>AUDITED BY: JK   | SHEET SIZE: 30x42<br>SCALE: 1/4"=1'-0"<br>FIELD MEASURE:<br>7/24/2023 |
| AX-101<br>1 OF 9   |                                                                       |



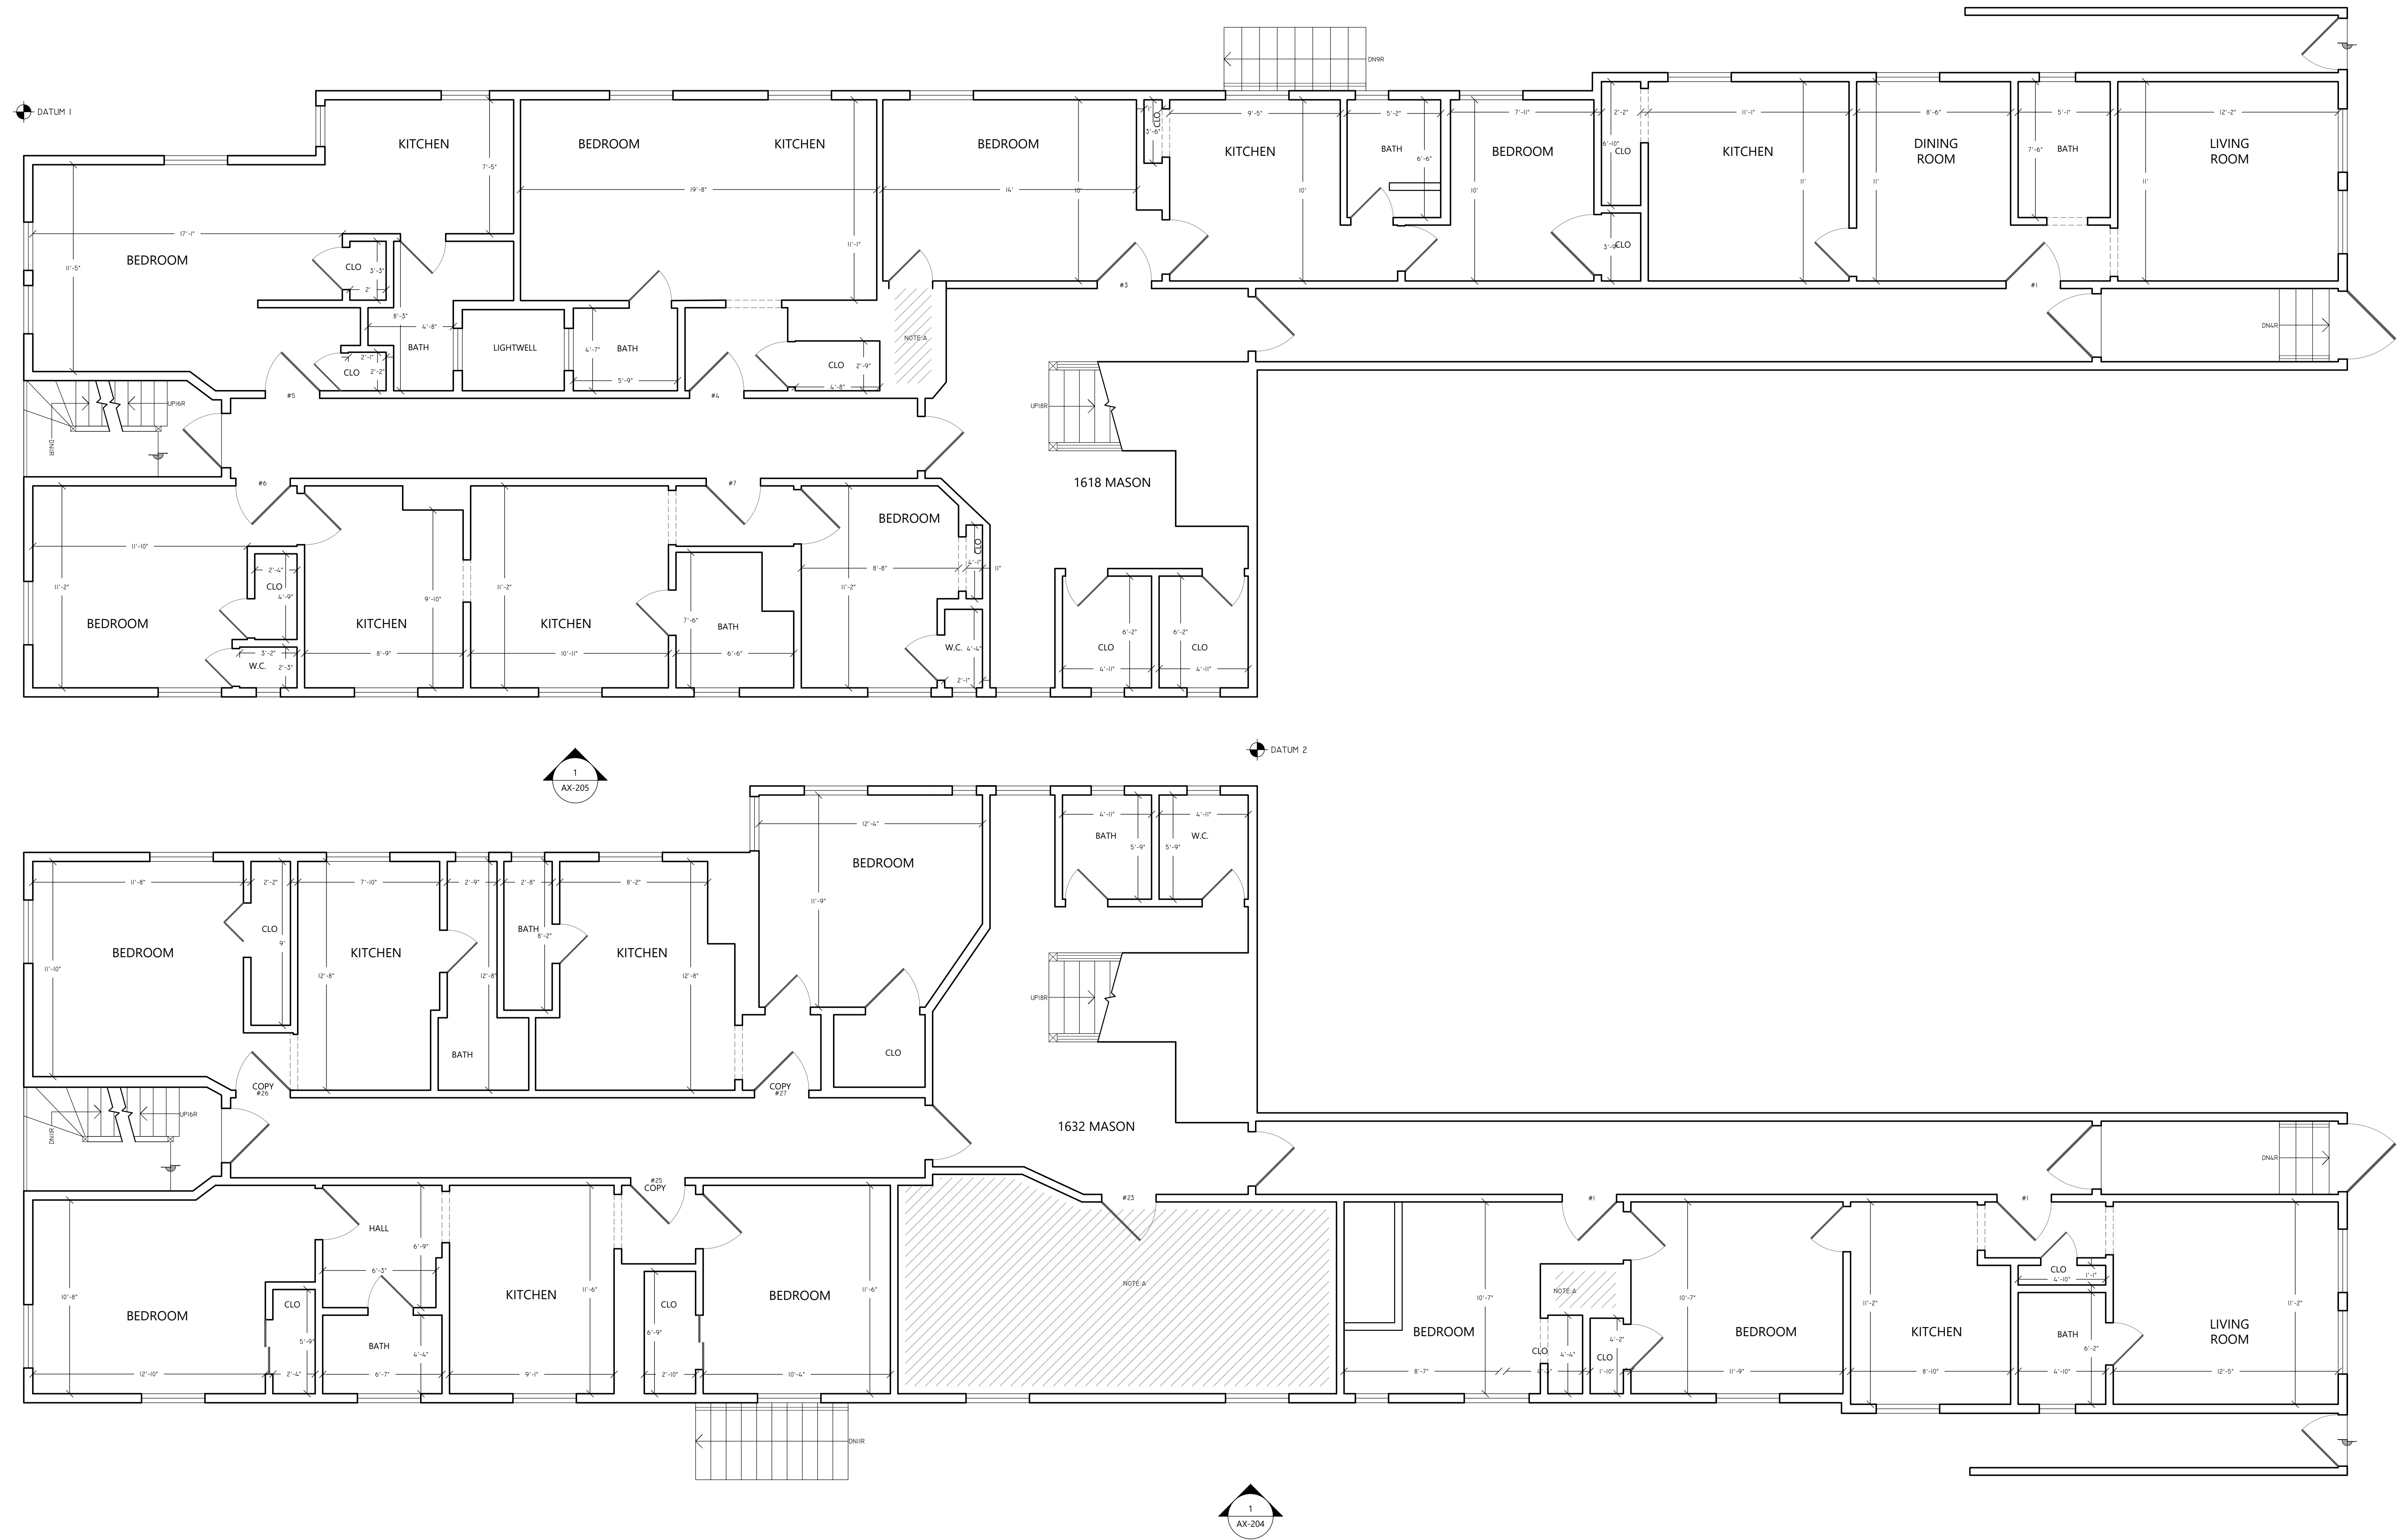


1 EXISTING ENTRY LEVEL FLOOR PLAN  
6,111 SQFT GROSS MEASURED AREA  
439 SQFT MEASURED EXTERIOR SURFACES

THESE ARE BASIC FLOOR PLANS. NO INTERIOR ELEMENTS SHOWN, UNLESS NOTED OTHERWISE.

NOTE A:  
THIS AREA NOT ACCESSIBLE AT TIME OF DATA ACQUISITION, AREA NOT MEASURED.

|   |                                                                       |
|---|-----------------------------------------------------------------------|
| 1618-1632 MASON STREET<br>SAN FRANCISCO, CA 94133   |                                                                       |
| THIS DRAWING IS A RECORD OF REAL PROPERTY THAT IS GENERALLY ACCEPTED TO BE SUITABLE FOR USE IN PLANNING, DESIGN, LEASE AND GENERAL ASSET MANAGEMENT. IT SHOULD NOT BE USED TO DETERMINE EXACT MEASUREMENTS OF SPACES OR ARTIFACTS FOUND HEREIN FOR ANY PURPOSE. | RED BRIDGE DESIGN<br>SAN FRANCISCO<br>REDBRIDGEDESIGN.COM             |
| EXISTING FLOOR PLAN   |                                                                       |
| REF: 1618-1632d_City_MFD<br>REV: 0<br>DRAWN BY: MV<br>AUDITED BY: JK   | SHEET SIZE: 30x42<br>SCALE: 1/4"=1'-0"<br>FIELD MEASURE:<br>7/24/2023 |
| AX-102<br>2 OF 9   |                                                                       |




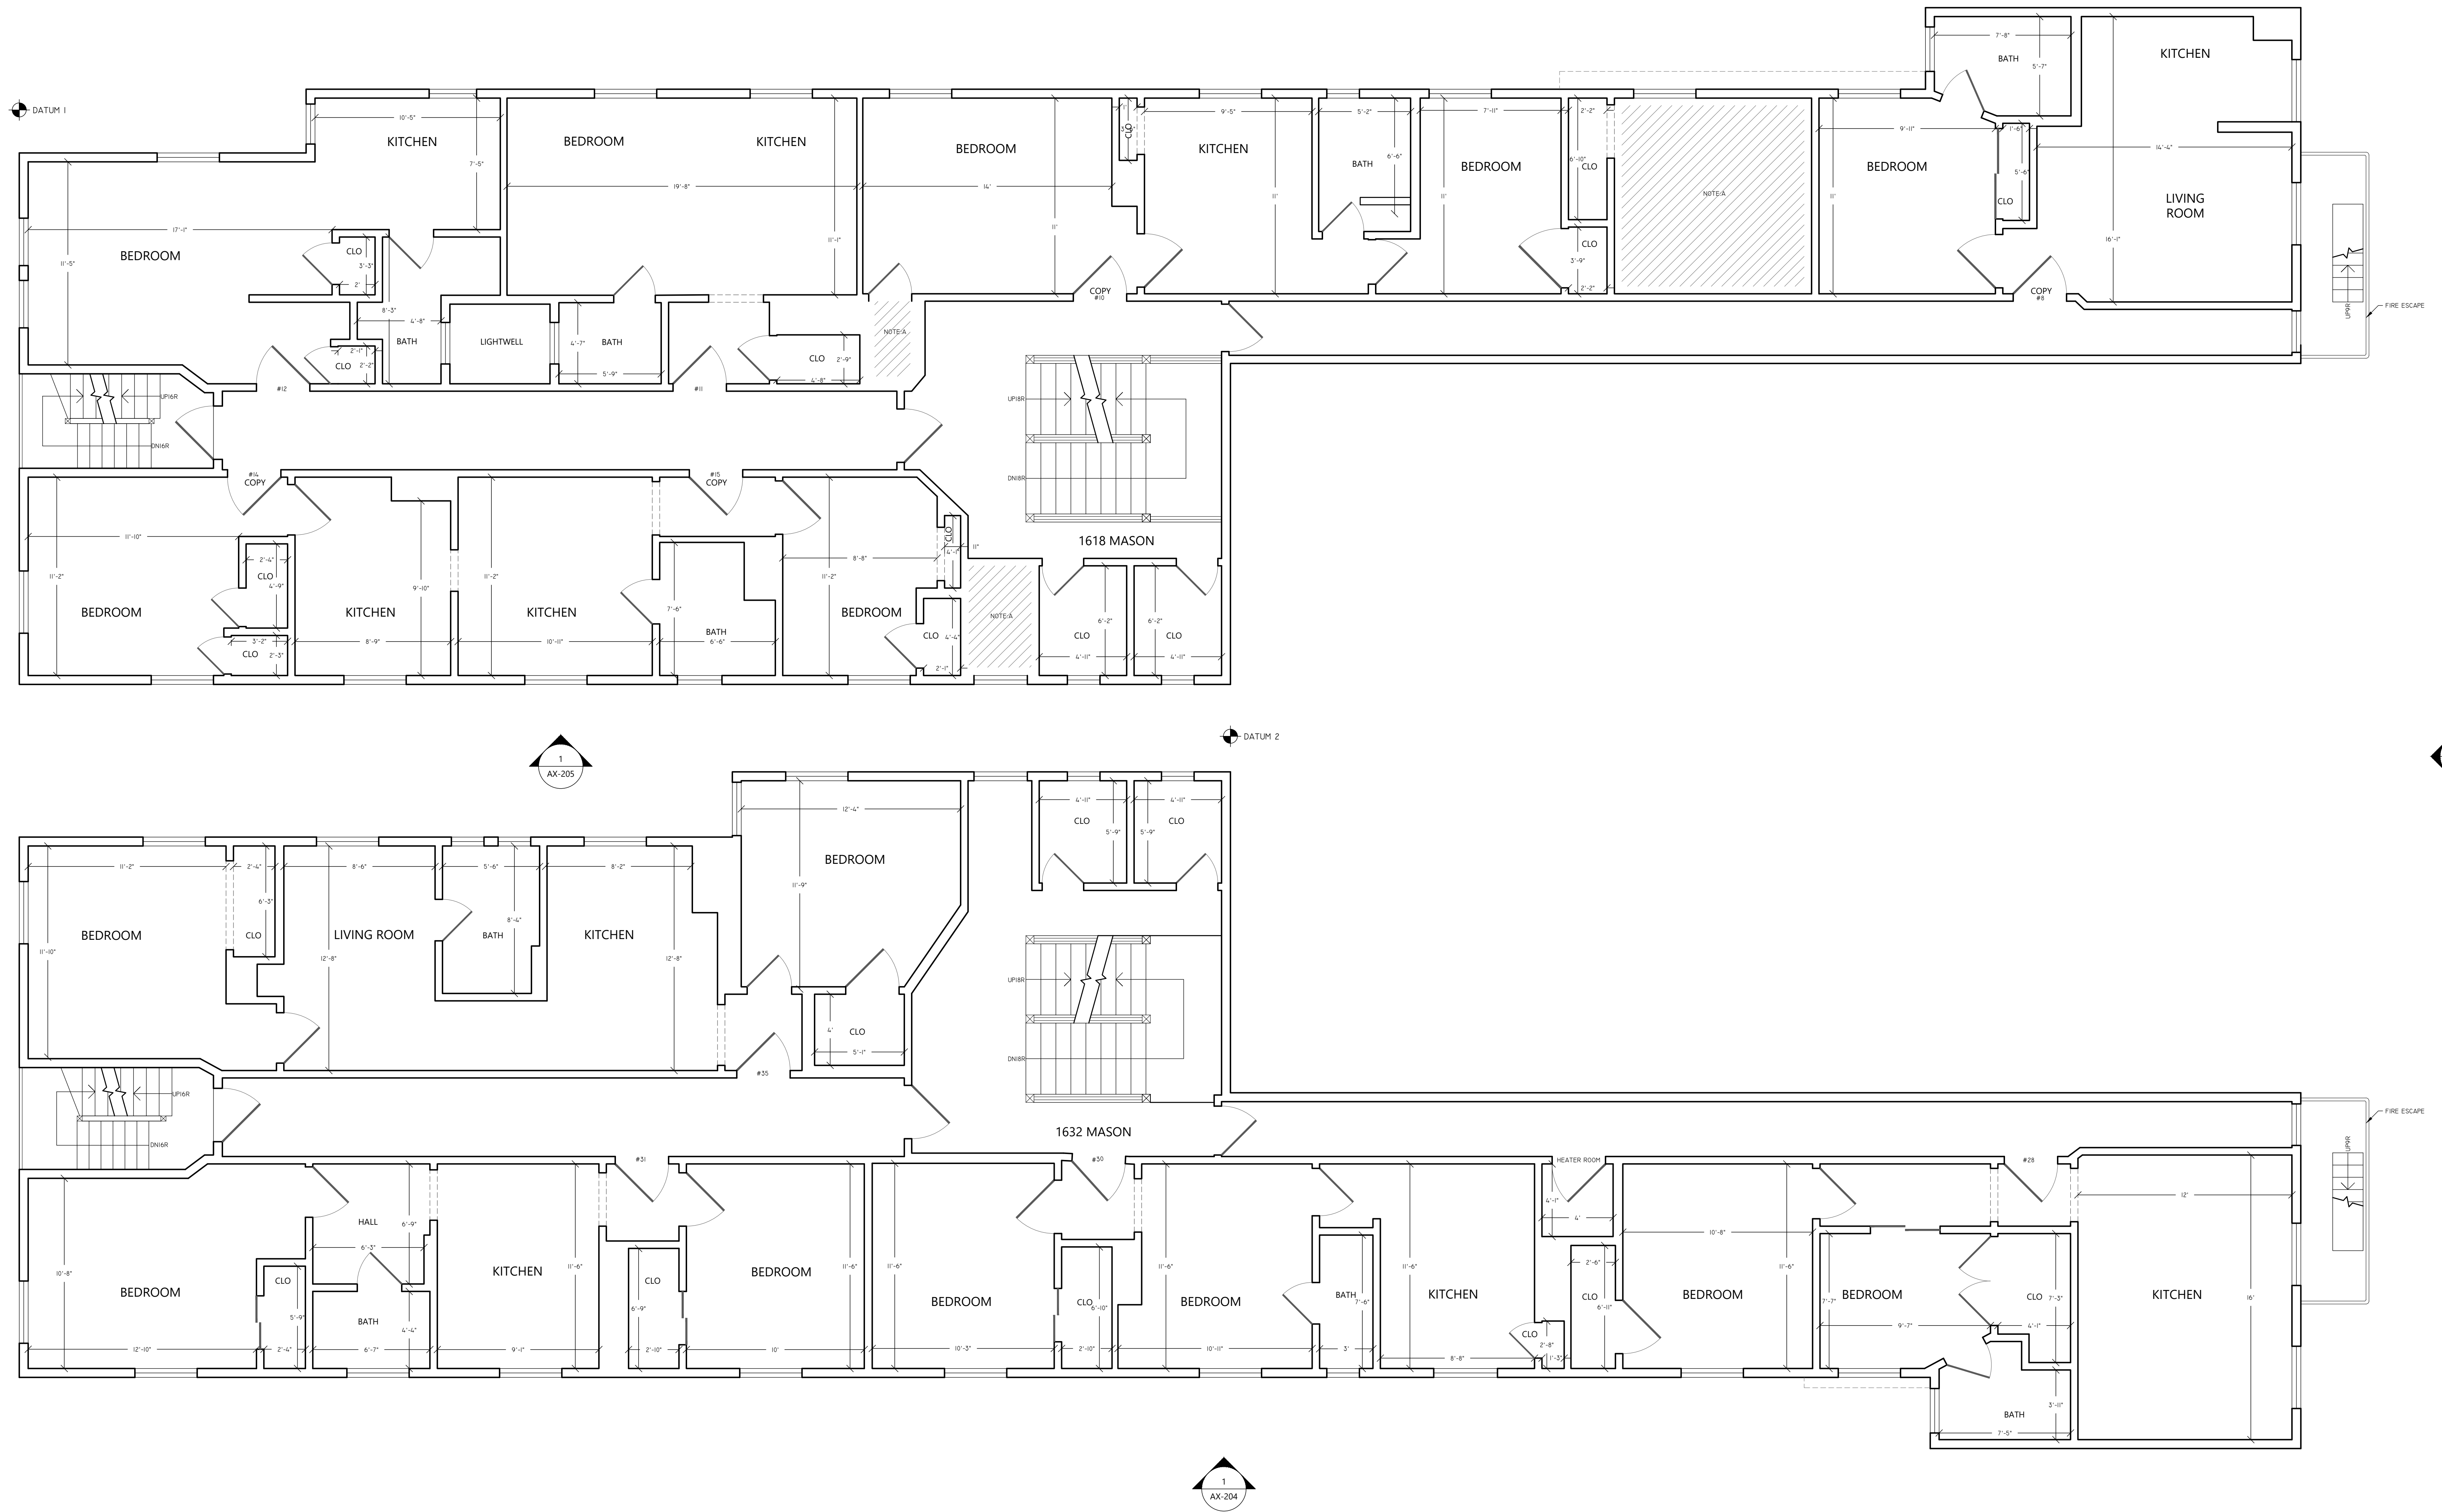


**1 EXISTING SECOND LEVEL FLOOR PLAN**  
 6,343 SQFT GROSS MEASURED AREA  
 207 SQFT MEASURED EXTERIOR SURFACES

THESE ARE BASIC FLOOR PLANS. NO INTERIOR ELEMENTS SHOWN, UNLESS NOTED OTHERWISE.

NOTE A:  
 THIS AREA NOT ACCESSIBLE AT TIME OF DATA ACQUISITION, AREA NOT MEASURED.
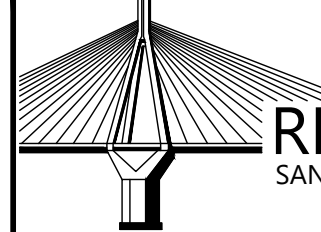
|   |   |
|---|---|
| 1618-1632 MASON STREET<br>SAN FRANCISCO, CA 94133   |   |
| THIS DRAWING IS A RECORD OF REAL PROPERTY THAT IS GENERALLY ACCEPTED TO BE SUITABLE FOR USE IN PLANNING, DESIGN, LEASE AND GENERAL ASSET MANAGEMENT. IT SHOULD NOT BE USED TO DETERMINE EXACT MEASUREMENTS OF SPACES OR ARTIFACTS FOUND HEREIN FOR ANY PURPOSE.<br><br>EXTERIOR ELEMENTS HAVE BEEN MEASURED AND DRAFTED FOR REFERENCE ONLY - THIS IS NOT A SURVEY. |  <b>RED BRIDGE DESIGN</b><br>SAN FRANCISCO<br>REDBRIDGEDSIGN.COM |
| <b>EXISTING FLOOR PLAN</b>   |   |
| REF: 1618-1632sf_City_MFD<br>REV: 0<br>DRAWN BY: MW<br>AUDITED BY: JK   | SHEET SIZE: 30x42<br>SCALE: 1/4"=1'-0"<br>FIELD MEASURE:<br>7/24/2023                                                                                 |
| <b>AX-103</b><br>3 OF 9   |   |



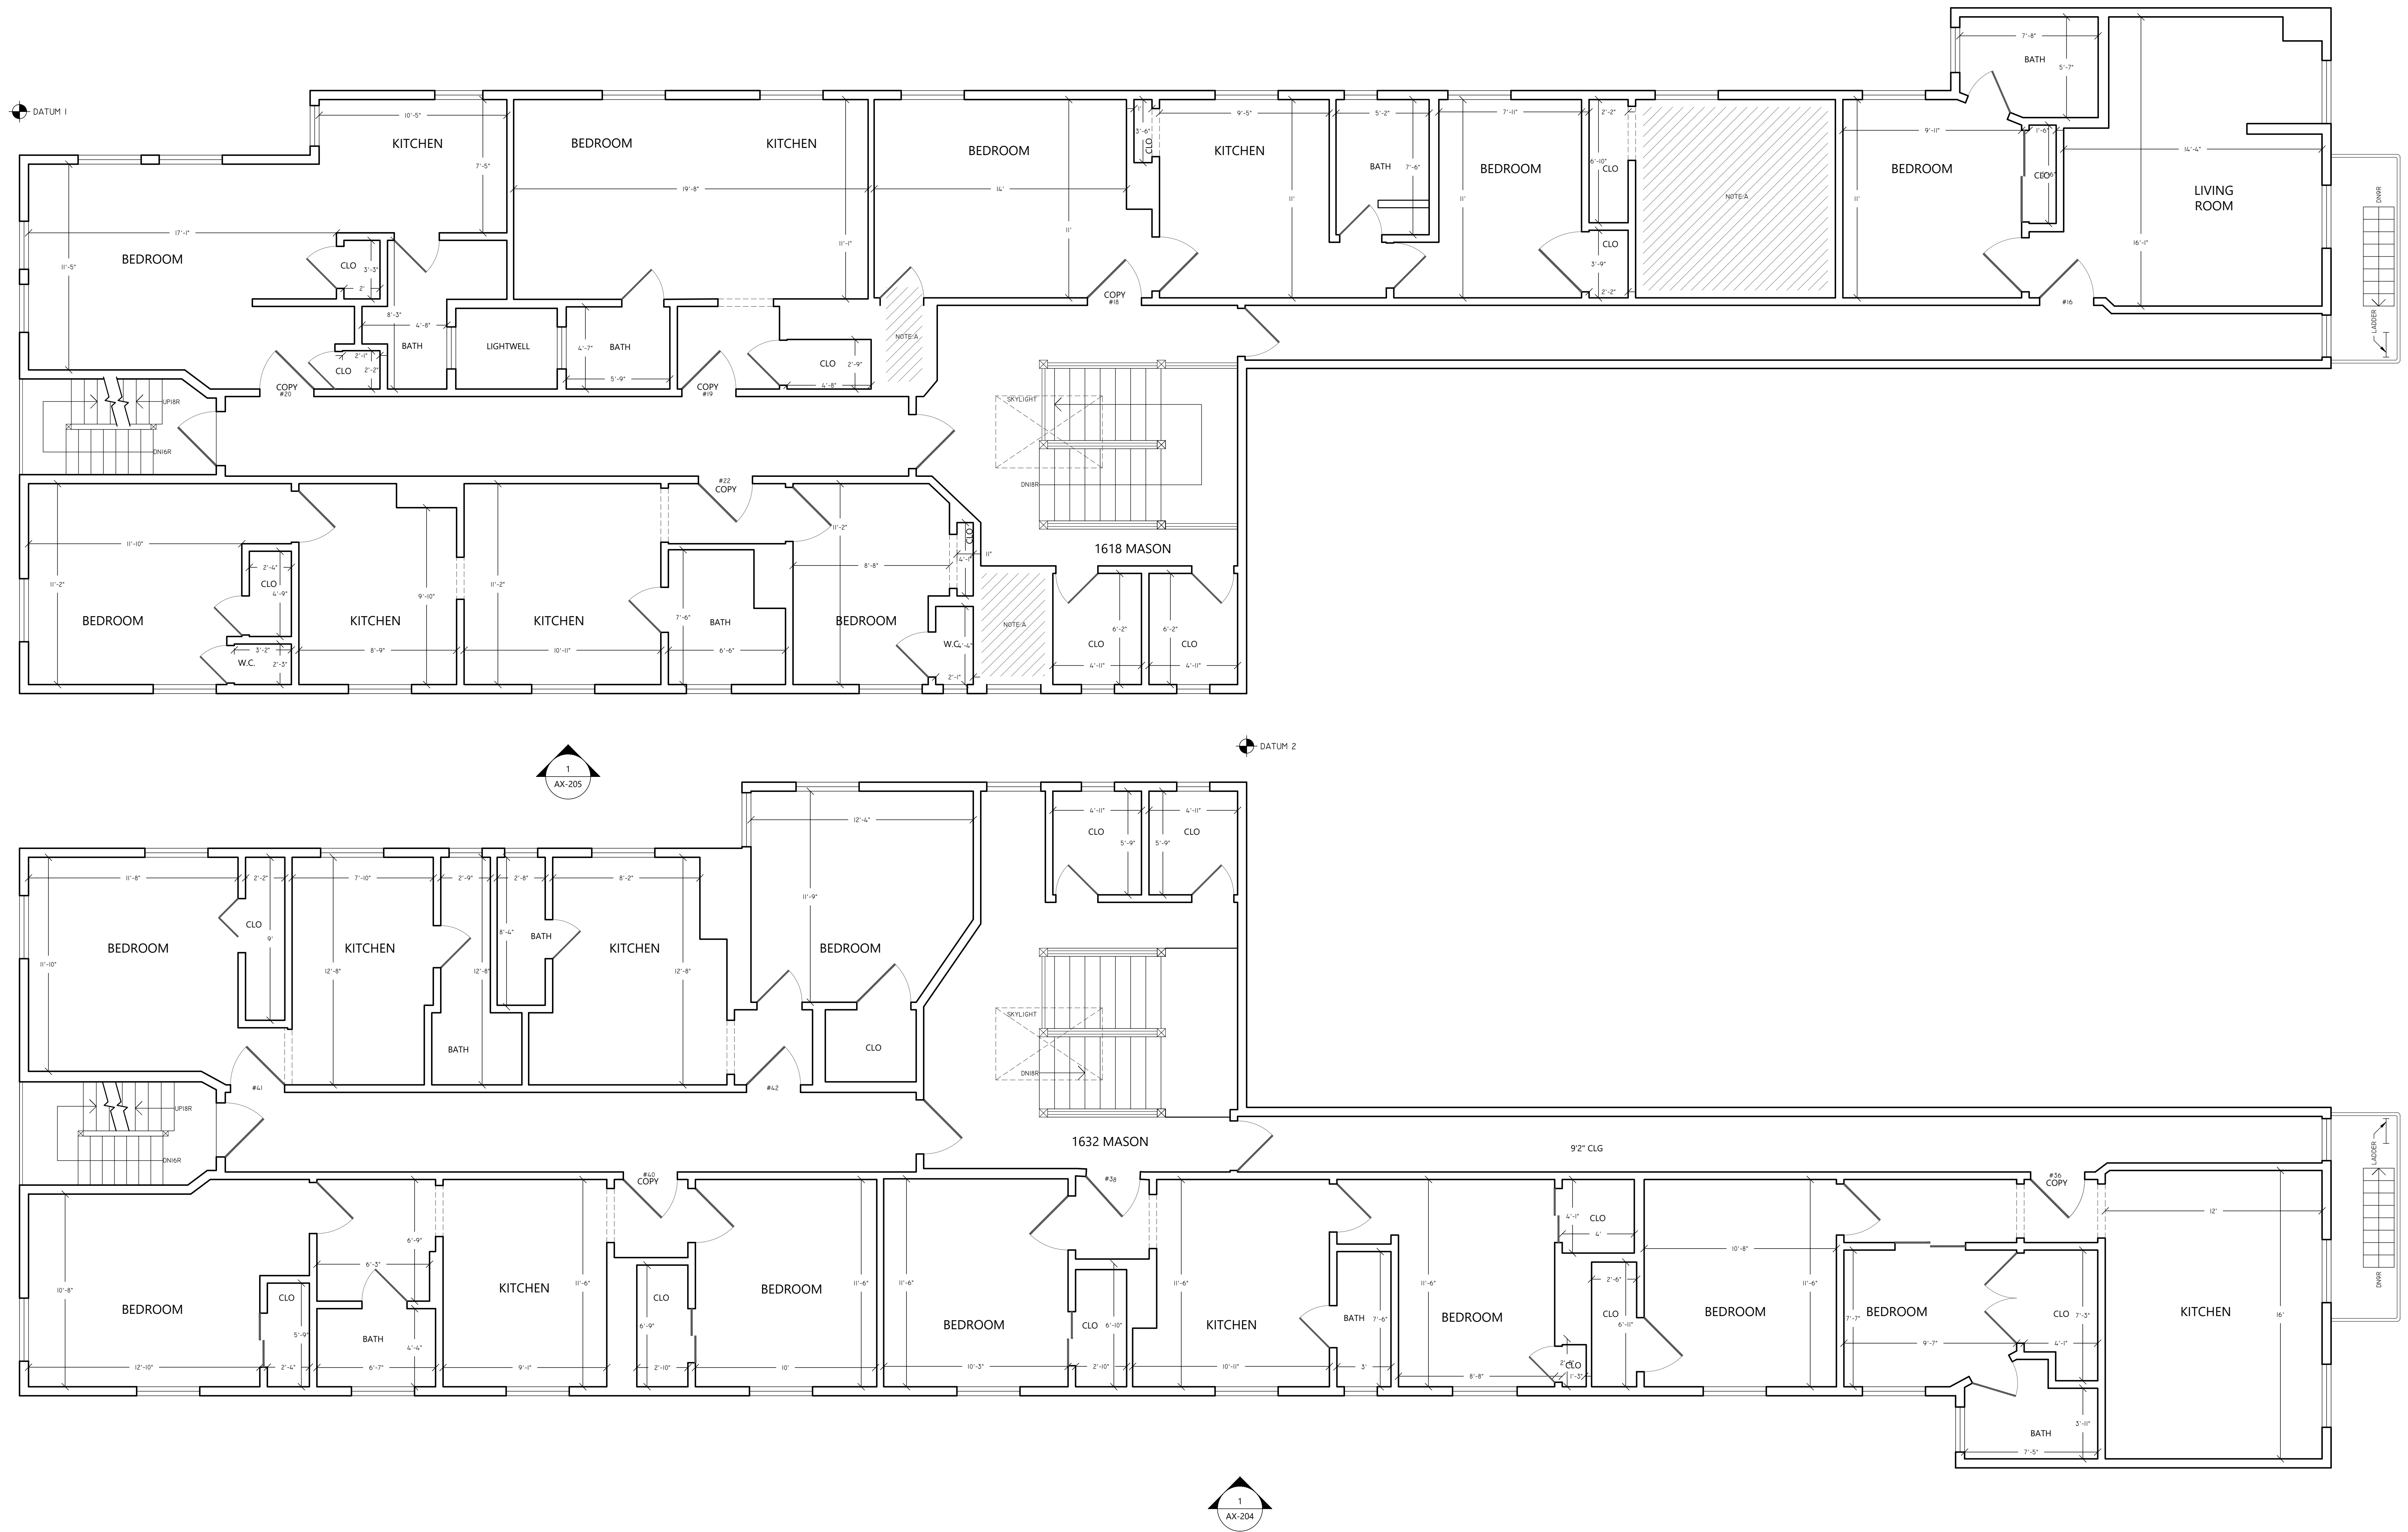

**1 EXISTING THIRD LEVEL FLOOR PLAN**  
6,343 SQFT GROSS MEASURED AREA  
207 SQFT MEASURED EXTERIOR SURFACES

THESE ARE BASIC FLOOR PLANS. NO INTERIOR ELEMENTS SHOWN, UNLESS NOTED OTHERWISE.

NOTE A:  
THIS AREA NOT ACCESSIBLE AT TIME OF DATA ACQUISITION, AREA NOT MEASURED.

|   |                                                                       |
|---|-----------------------------------------------------------------------|
| 1618-1632 MASON STREET<br>SAN FRANCISCO, CA 94133   |                                                                       |
| <small>THIS DRAWING IS A RECORD OF REAL PROPERTY THAT IS GENERALLY ACCEPTED TO BE SUITABLE FOR USE IN PLANNING, DESIGN, LEASE AND GENERAL ASSET MANAGEMENT. IT SHOULD NOT BE USED TO DETERMINE EXACT MEASUREMENTS OF SPACES OR ARTIFACTS FOUND HEREIN FOR ANY PURPOSE.</small> |                                                                       |
| <small>EXTERIOR ELEMENTS HAVE BEEN MEASURED AND DRAFTED FOR REFERENCE ONLY - THIS IS NOT A SURVEY.</small>   |                                                                       |
| RED BRIDGE DESIGN<br>SAN FRANCISCO<br>REDBRIDGEDESIGN.COM   |                                                                       |
| EXISTING FLOOR PLAN   |                                                                       |
| REF: 1618-1632d_City_MFD<br>REV: 0<br>DRAWN BY: MV<br>AUDITED BY: JK   | SHEET SIZE: 30x42<br>SCALE: 1/4"=1'-0"<br>FIELD MEASURE:<br>7/24/2023 |
| AX-104<br>4 OF 9   |                                                                       |






1 EXISTING WEST ELEVATION





1 EXISTING SOUTH ELEVATION



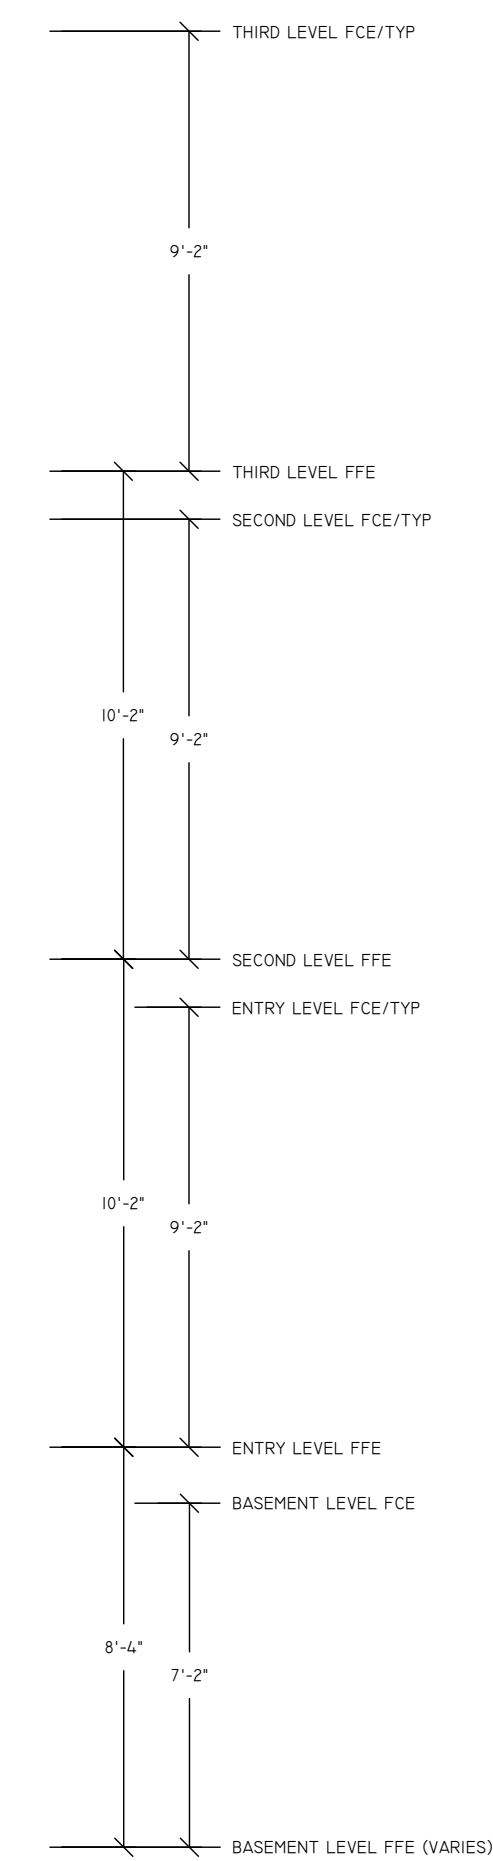

1 EXISTING EAST ELEVATION

1618-1632 MASON STREET  
SAN FRANCISCO, CA 94133

THIS DRAWING IS A RECORD OF REAL PROPERTY THAT IS GENERALLY ACCEPTED TO BE SUITABLE FOR USE IN PLANNING, DESIGN, LEASE AND GENERAL ASSET MANAGEMENT. IT SHOULD NOT BE USED TO DETERMINE EXACT MEASUREMENTS OF SPACES OR ARTIFACTS FOUND HEREIN FOR ANY PURPOSE.




EXISTING EXTERIOR ELEVATIONS

REF: 1618-1632sf\_City\_MFD  
REV: 0  
DRAWN BY: MM  
AUDITED BY: JK

SHEET SIZE: 30x42  
SCALE: 1/4"=1'-0"  
FIELD MEASURE:  
7/24/2023


AX-203  
7 OF 9



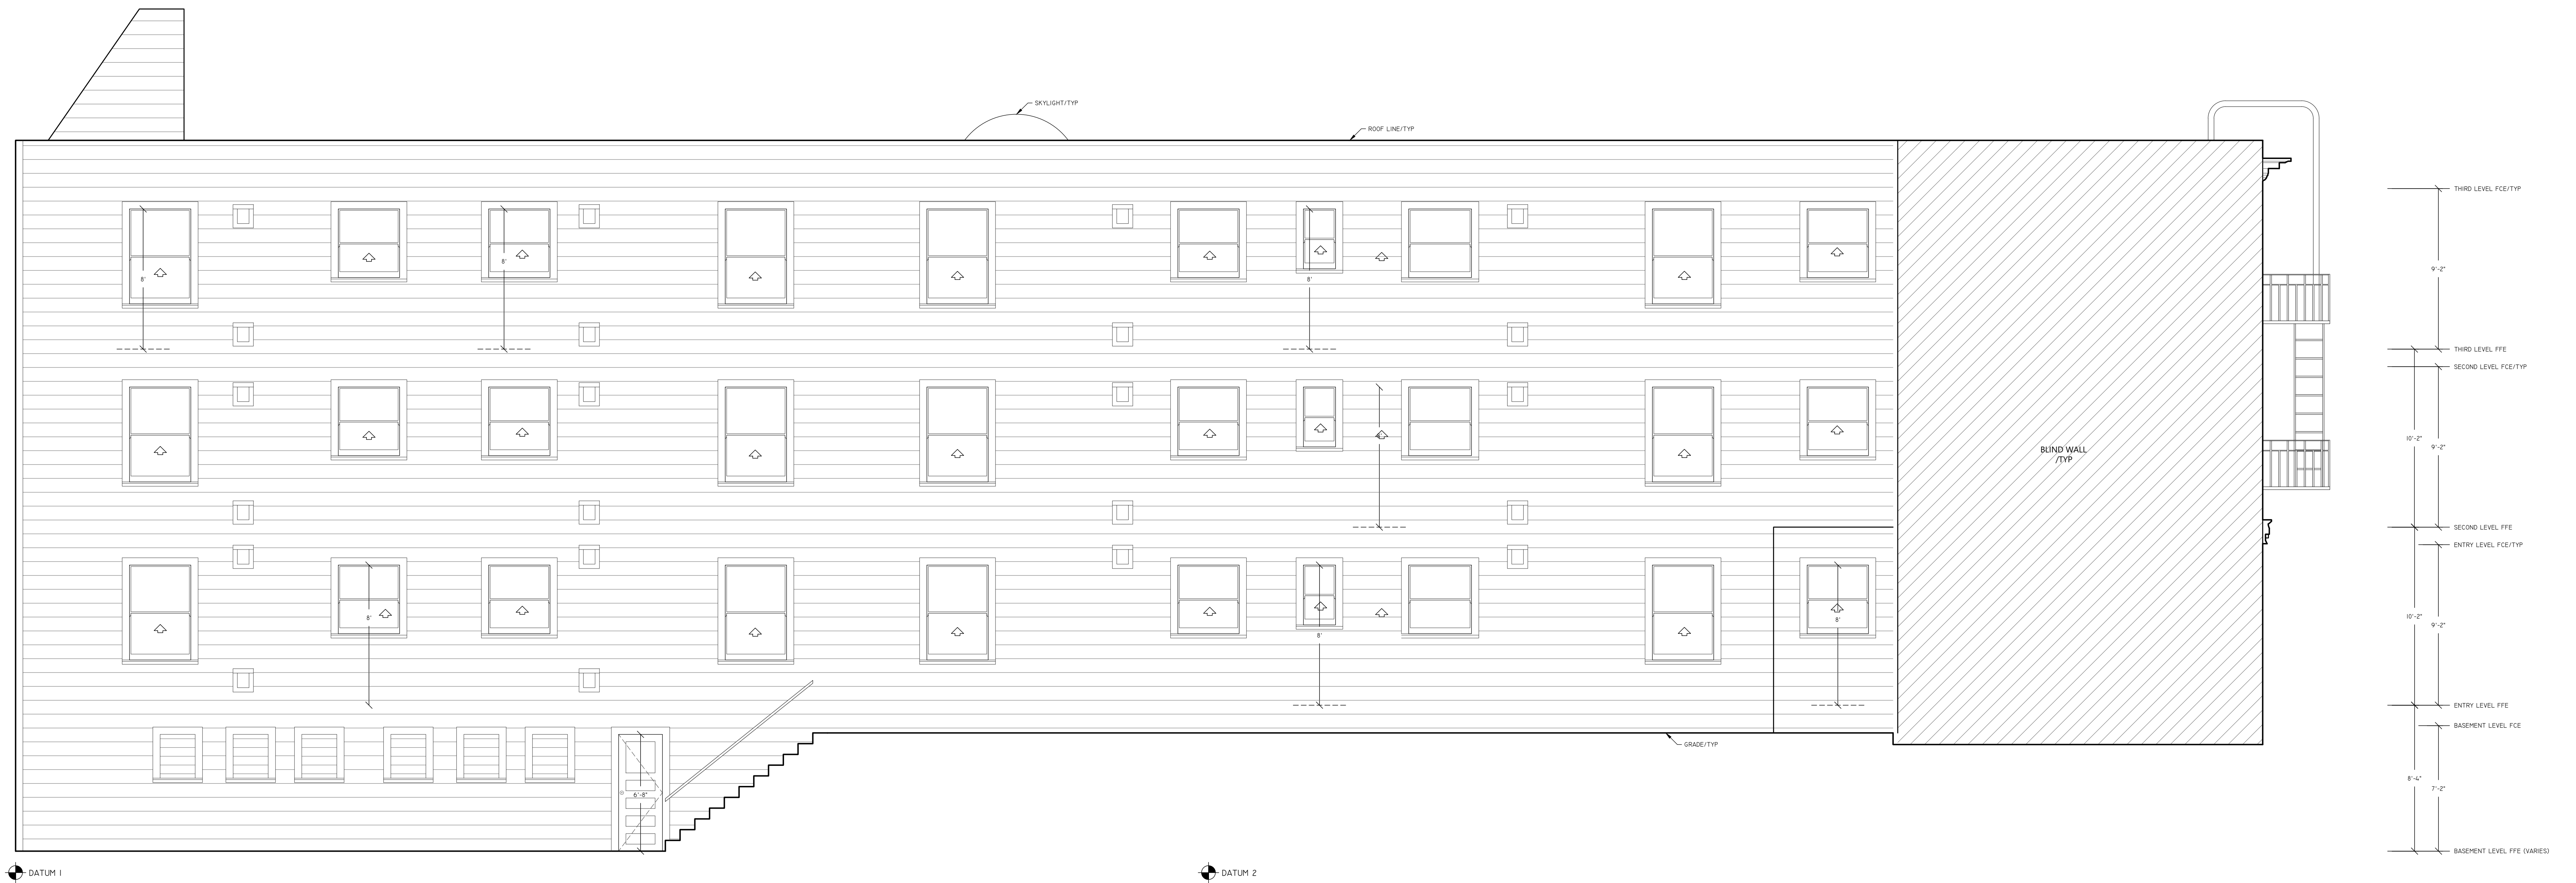

① EXISTING NORTH ELEVATION



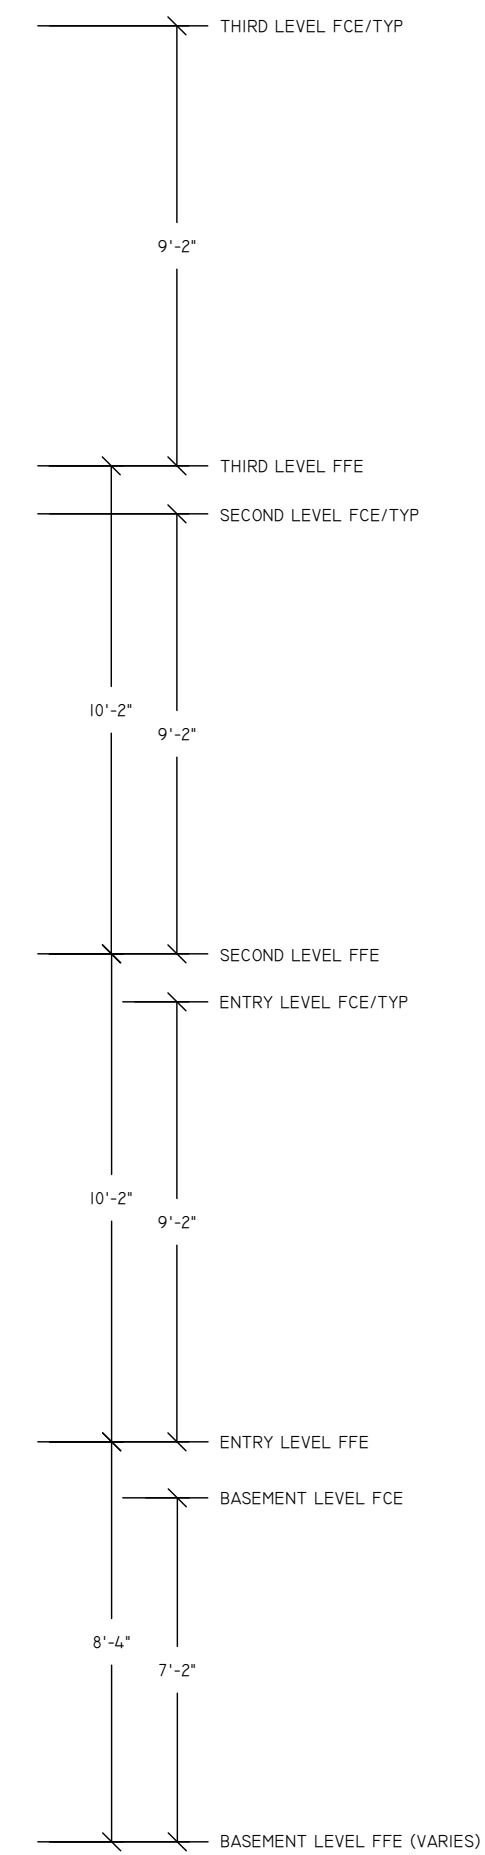

1 EXISTING NORTH ELEVATION 2

1618-1632 MASON STREET  
SAN FRANCISCO, CA 94133

THIS DRAWING IS A RECORD OF REAL PROPERTY THAT IS GENERALLY ACCEPTED TO BE SUITABLE FOR USE IN PLANNING, DESIGN, LEASE AND GENERAL ASSET MANAGEMENT. IT SHOULD NOT BE USED TO DETERMINE EXACT MEASUREMENTS OF SPACES OR ARTIFACTS FOUND HEREIN FOR ANY PURPOSE.



EXISTING EXTERIOR ELEVATIONS

REF: 1618-1632sf\_City\_MFD  
REV: 0  
DRAWN BY: MM  
AUDITED BY: JK

SHEET SIZE: 30x42  
SCALE: 1/4"=1'-0"  
FIELD MEASURE:  
7/24/2023

AX-205  
9 OF 9