


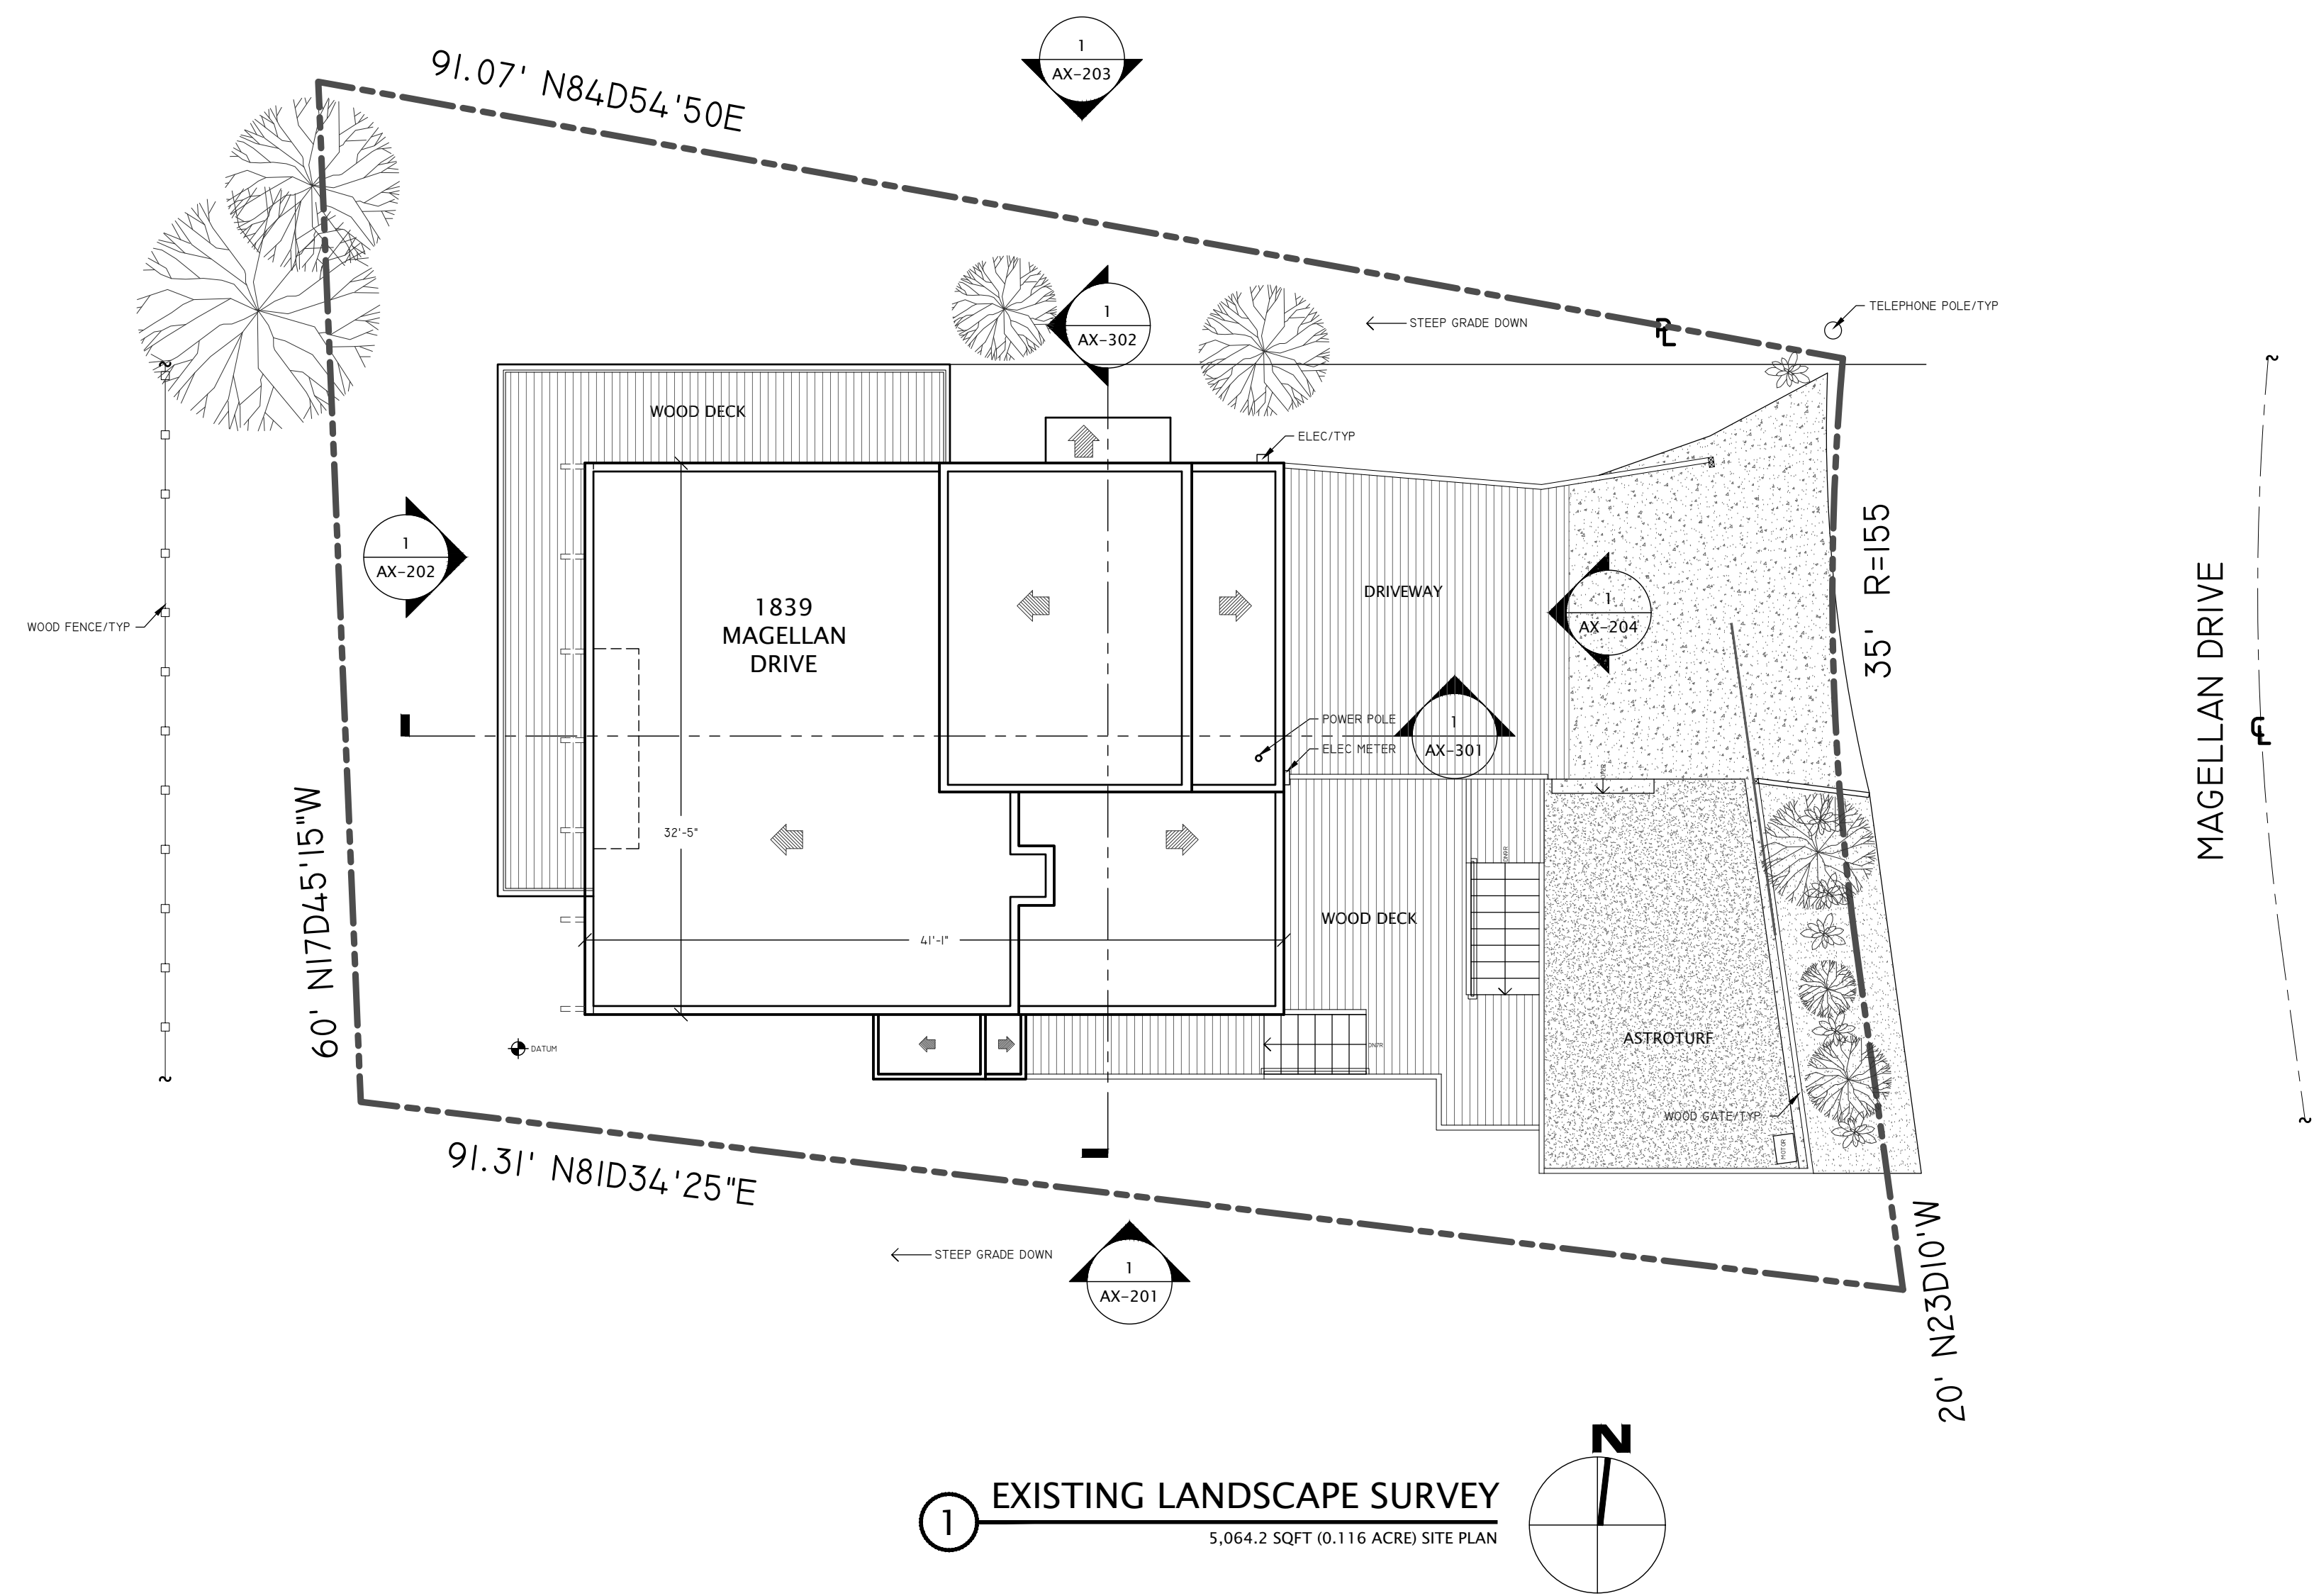

1.) THIS IS NOT A LAND SURVEY, PROPERTY LINES ARE NOT DETERMINED.
2.) PROPERTY LINES ARE COPIED FROM TAX ASSESSOR'S MAP. PLACEMENT ASSUMED.

1839 MAGELLAN DRIVE
OAKLAND, CA 94611

THIS DRAWING IS A RECORD OF REAL PROPERTY THAT IS GENERALLY ACCEPTED TO BE SUITABLE FOR USE IN PLANNING, DESIGN, LEASE, AND GENERAL ASSET MANAGEMENT. IT SHOULD NOT BE USED TO DETERMINE EXACT MEASUREMENTS OF SPACES OR ARTIFACTS FOUND HEREIN FOR ANY PURPOSE.
EXTERIOR ELEMENTS HAVE BEEN MEASURED AND DRAFTED FOR REFERENCE ONLY - THIS IS NOT A SURVEY.




EXISTING LANDSCAPE SURVEY

REF: 1839sf_Oakland_SFD
REV: 0
DRAWN BY: MV
AUDITED BY: JK

SHEET SIZE: 24x36
SCALE: 1/4"=1'-0"
FIELD MEASURE:
12/20/19

AX-101
1 OF 10

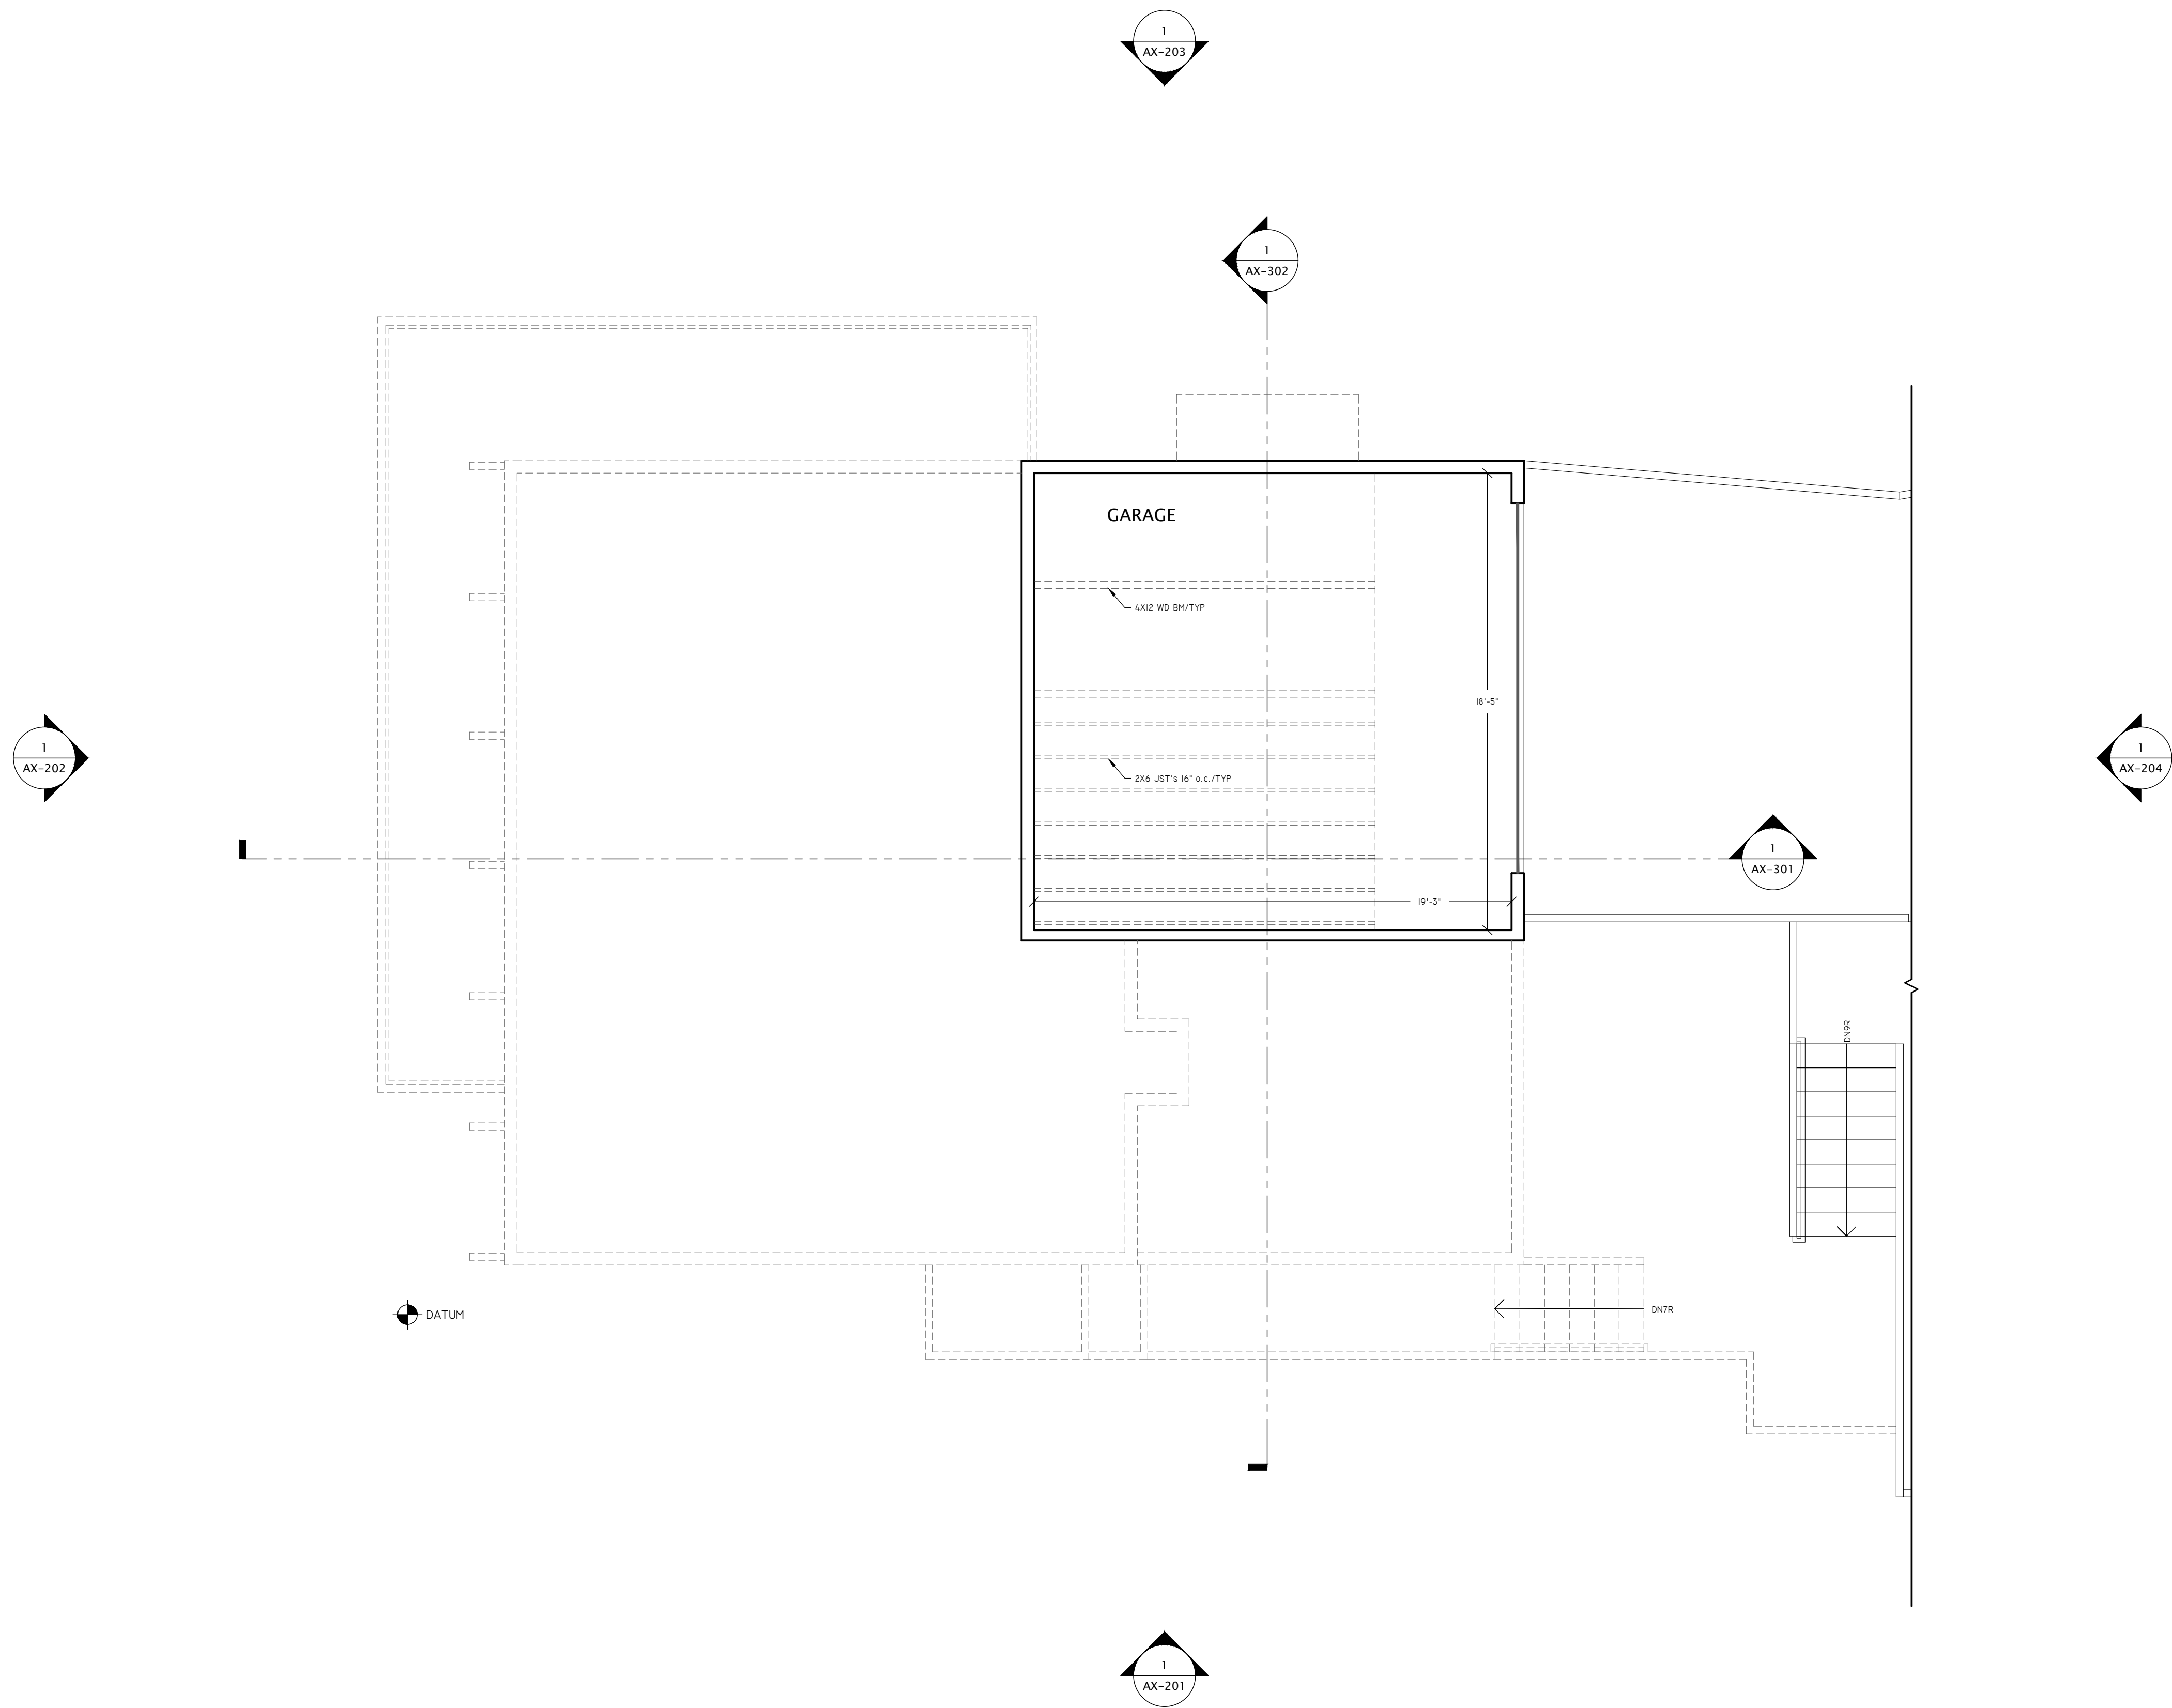

1 EXISTING GARAGE LEVEL FLOOR PLAN
392 SQFT GROSS MEASURED AREA

THESE ARE BASIC FLOOR PLANS. NO INTERIOR ELEMENTS SHOWN,
UNLESS NOTED OTHERWISE.

1839 MAGELLAN DRIVE
OAKLAND, CA 94611

THIS DRAWING IS A RECORD OF REAL PROPERTY
THAT IS GENERALLY ACCEPTED TO BE SUITABLE
FOR USE IN PLANNING, DESIGN, LEASE, AND
GENERAL ASSET MANAGEMENT. IT SHOULD NOT BE
USED TO DETERMINE EXACT MEASUREMENTS OF
SPACES OR ARTIFACTS FOUND HEREIN FOR ANY
PURPOSE.
EXTERIOR ELEMENTS HAVE BEEN MEASURED AND
DRAFTED FOR REFERENCE ONLY - THIS IS NOT A
SURVEY.




EXISTING FLOOR PLAN

REF: 1839sf_Oakland_SFD
REV: 0
DRAWN BY: MV
AUDITED BY: JK

SHEET SIZE: 24x36
SCALE: 1/4"=1'-0"
FIELD MEASURE:
12/20/19

AX-102
2 OF 10

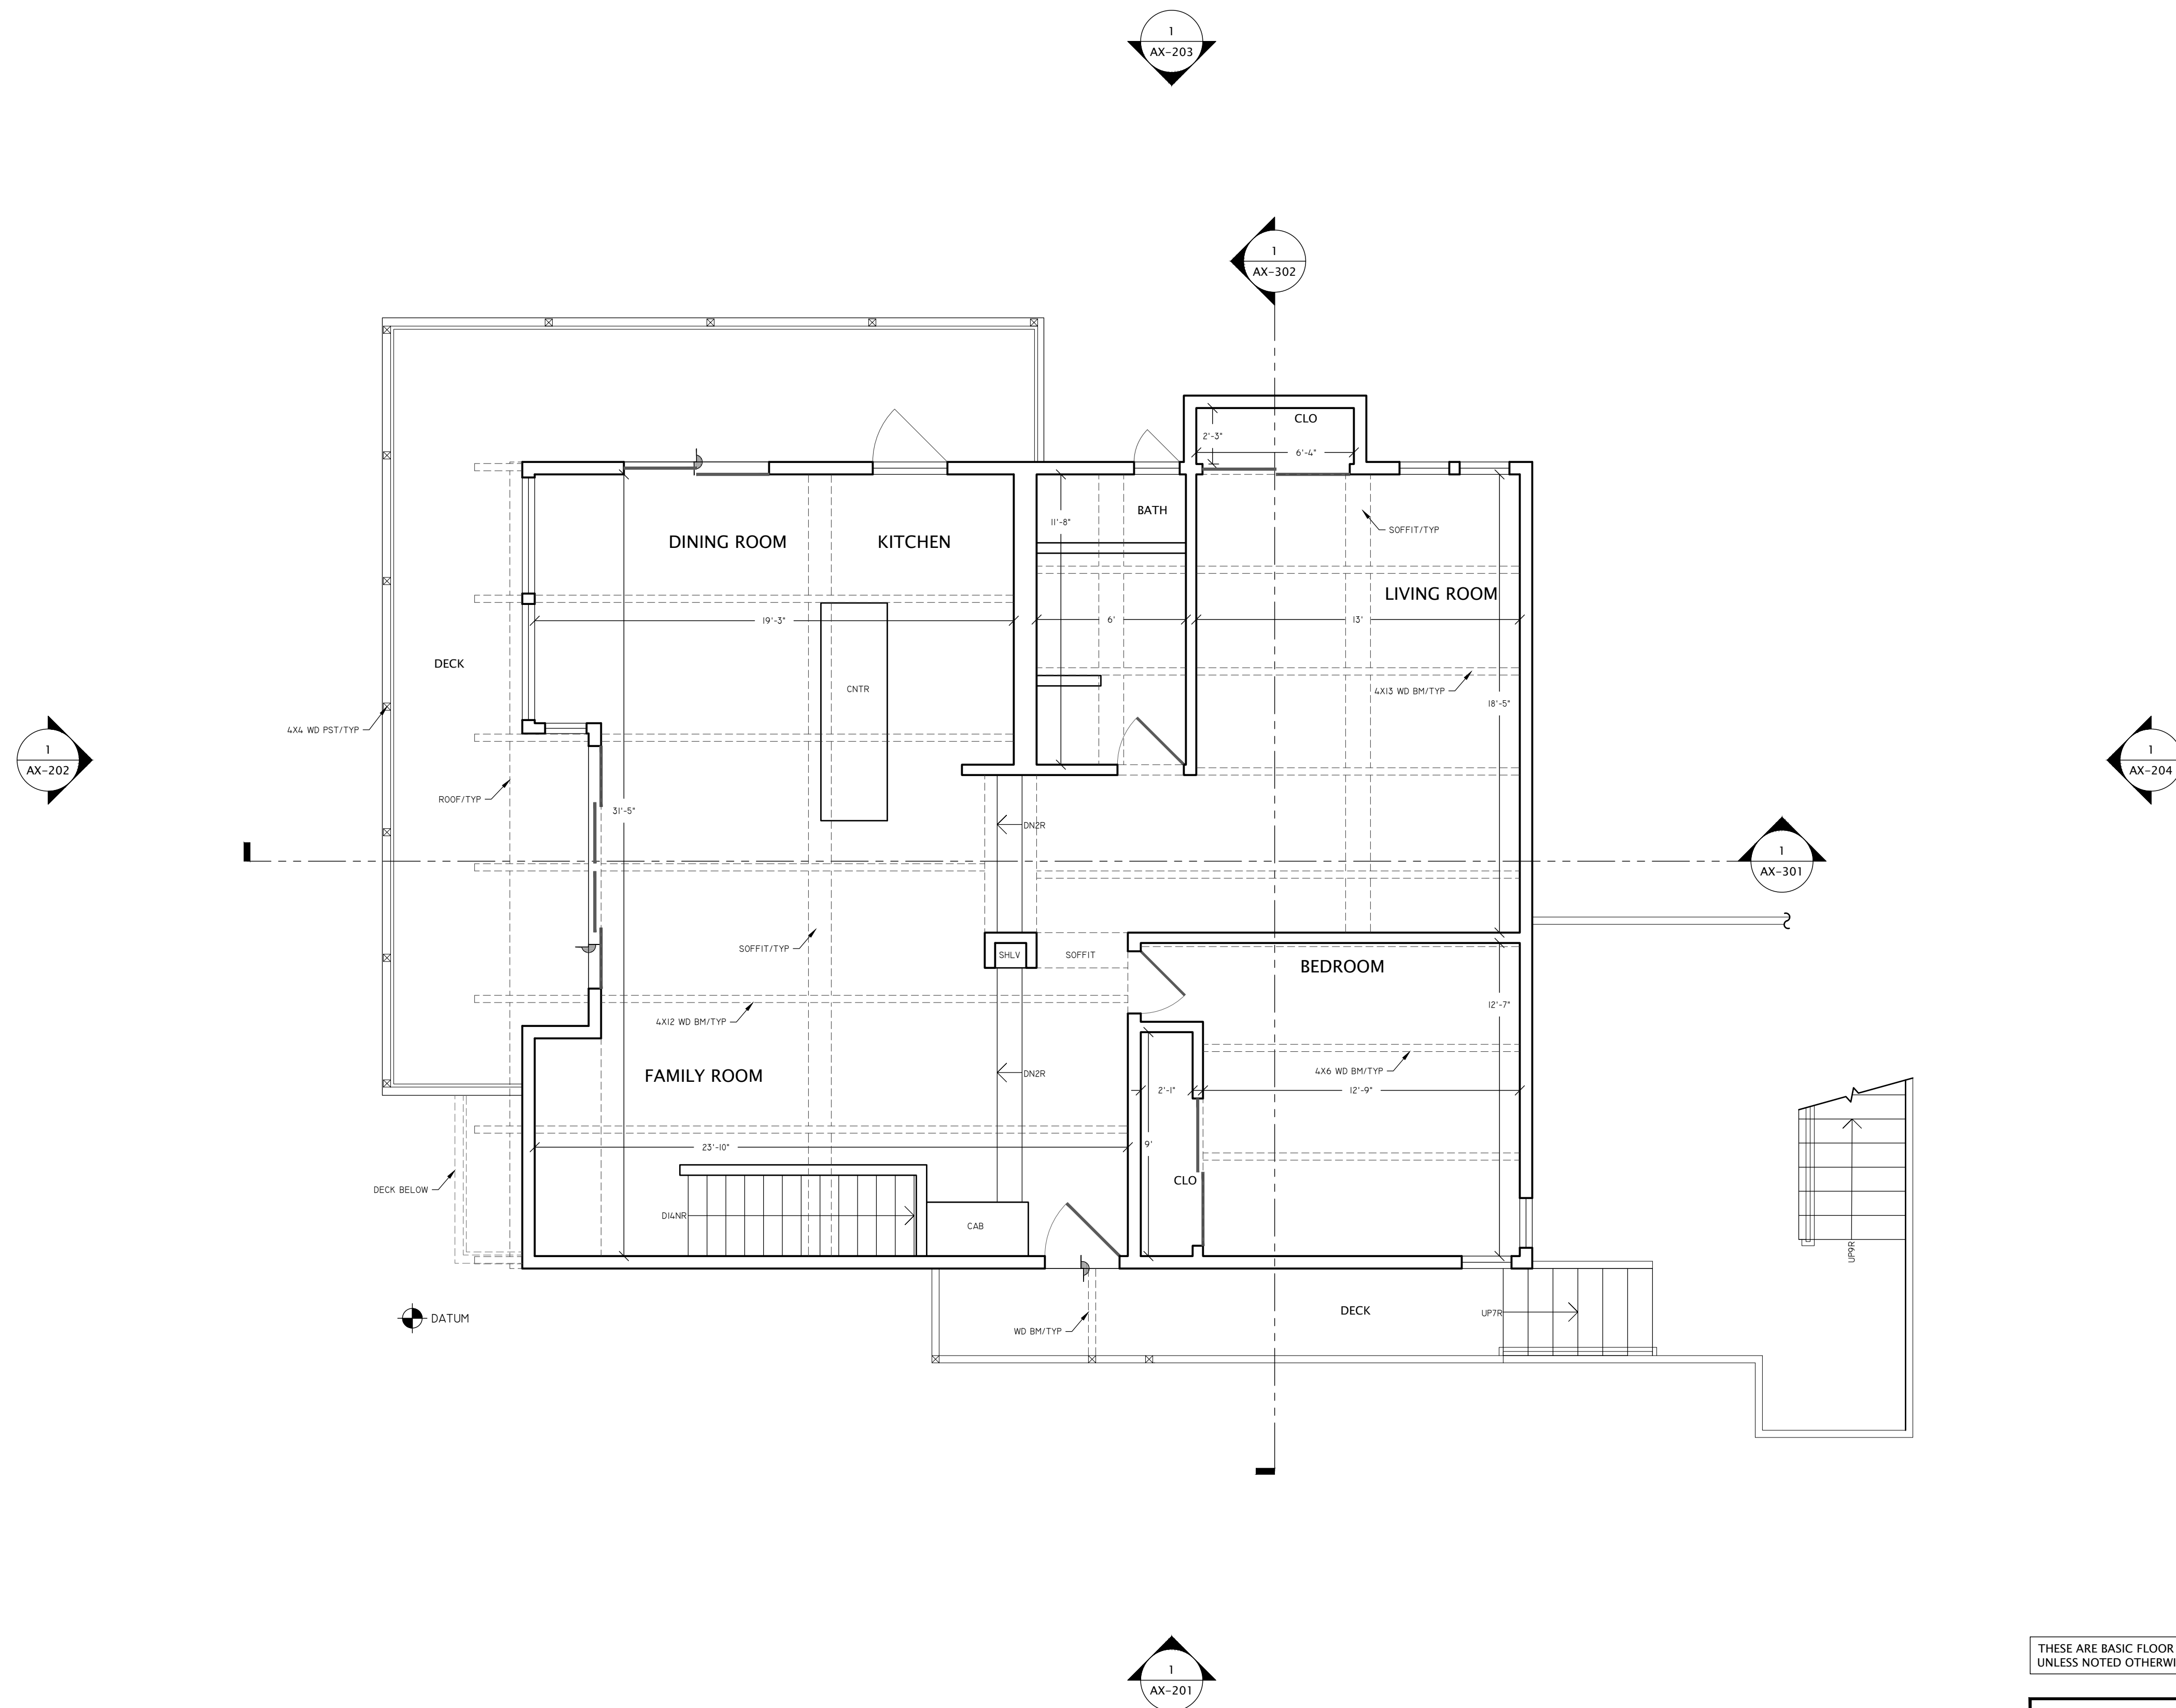

1 EXISTING ENTRY LEVEL FLOOR PLAN
1,304 SQFT GROSS MEASURED AREA
676 SQFT MEASURED EXTERIOR SURFACES

THESE ARE BASIC FLOOR PLANS. NO INTERIOR ELEMENTS SHOWN, UNLESS NOTED OTHERWISE.

1839 MAGELLAN DRIVE
OAKLAND, CA 94611

THIS DRAWING IS A RECORD OF REAL PROPERTY THAT IS GENERALLY ACCEPTED TO BE SUITABLE FOR USE IN PLANNING, DESIGN, LEASE, AND GENERAL ASSET MANAGEMENT. IT SHOULD NOT BE USED TO DETERMINE EXACT MEASUREMENTS OF SPACES OR ARTIFACTS FOUND HEREIN FOR ANY PURPOSE.




EXISTING FLOOR PLAN

REF: 1839sf_Oakland_SFD
REV: 0
DRAWN BY: MV
AUDITED BY: JK

SHEET SIZE: 24x36
SCALE: 1/4"=1'-0"
FIELD MEASURE:
12/20/19

AX-103
3 OF 10

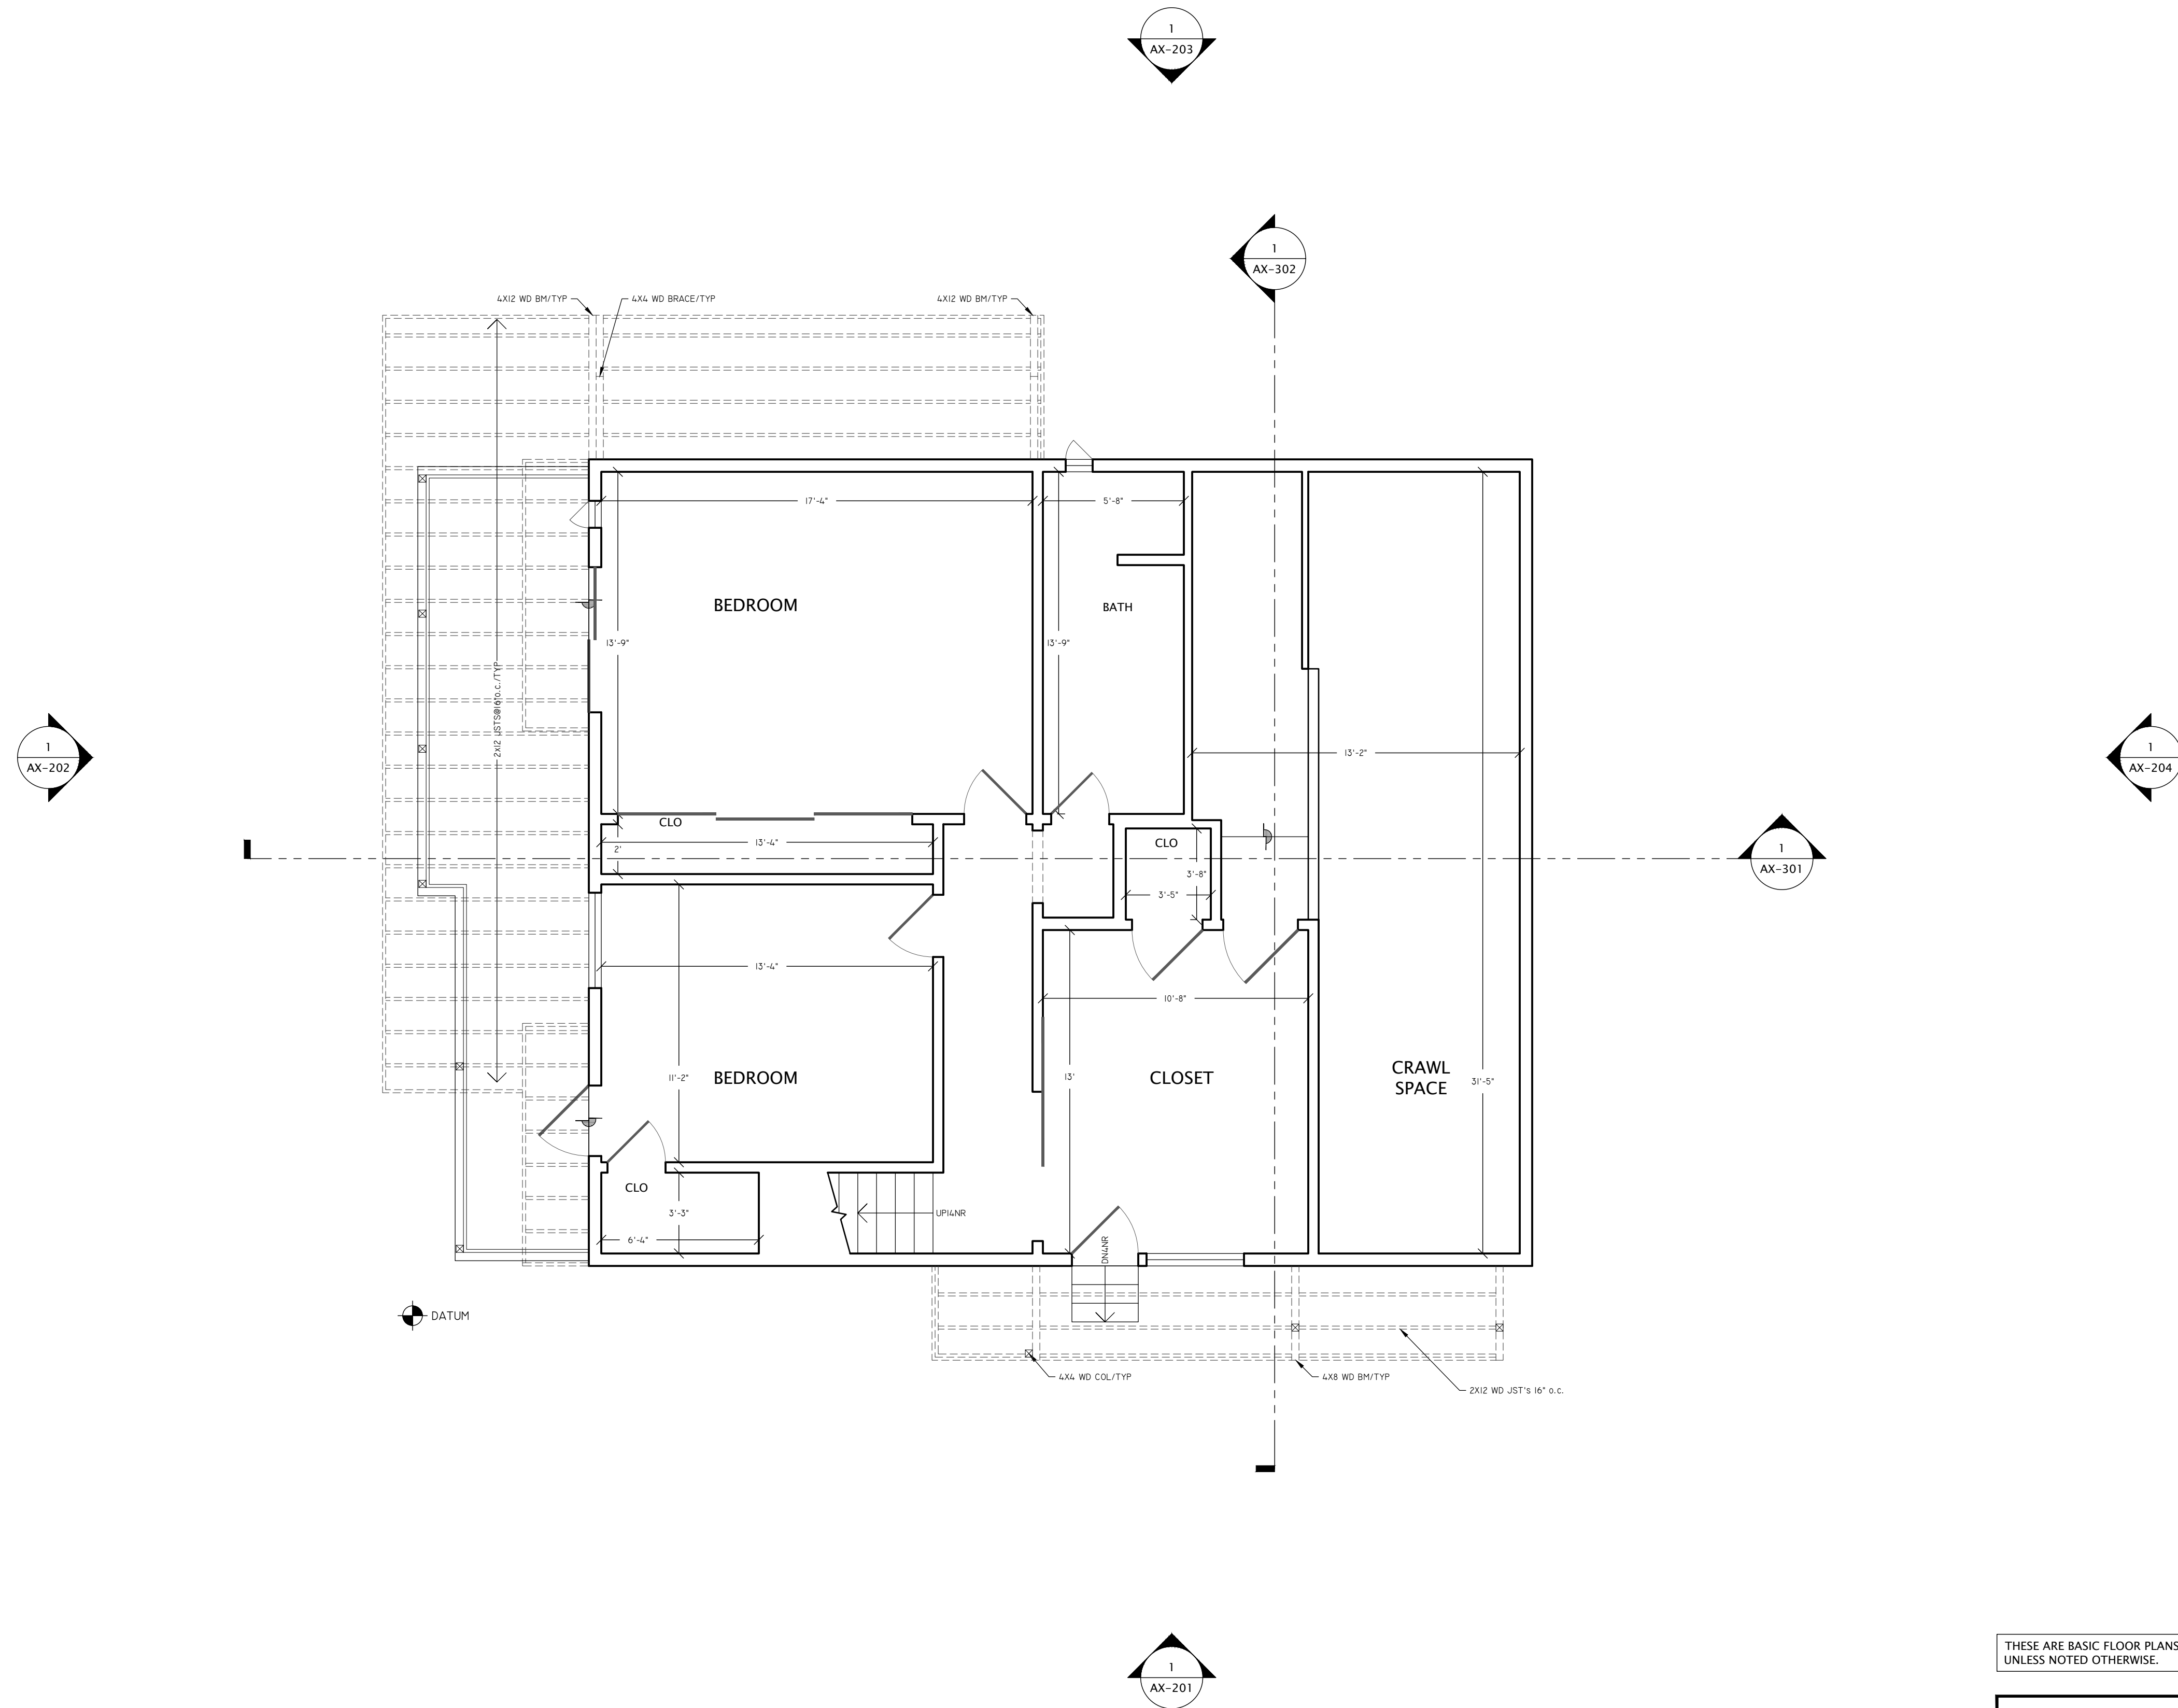

1 EXISTING SECOND LEVEL FLOOR PLAN

1,229 SQFT GROSS MEASURED AREA
203 SQFT MEASURED EXTERIOR SURFACES

THESE ARE BASIC FLOOR PLANS. NO INTERIOR ELEMENTS SHOWN, UNLESS NOTED OTHERWISE.

1839 MAGELLAN DRIVE
OAKLAND, CA 94611

THIS DRAWING IS A RECORD OF REAL PROPERTY THAT IS GENERALLY ACCEPTED TO BE SUITABLE FOR USE IN PLANNING, DESIGN, LEASE, AND GENERAL ASSET MANAGEMENT. IT SHOULD NOT BE USED TO DETERMINE EXACT MEASUREMENTS OF SPACES OR ARTIFACTS FOUND HEREIN FOR ANY PURPOSE.

EXTERIOR ELEMENTS HAVE BEEN MEASURED AND DRAFTED FOR REFERENCE ONLY - THIS IS NOT A SURVEY.




EXISTING FLOOR PLAN

REF: 1839sf_Oakland_SFD
REV: 0
DRAWN BY: MV
AUDITED BY: JK

SHEET SIZE: 24x36
SCALE: 1/4"=1'-0"
FIELD MEASURE:
12/20/19

AX-104


4 OF 10

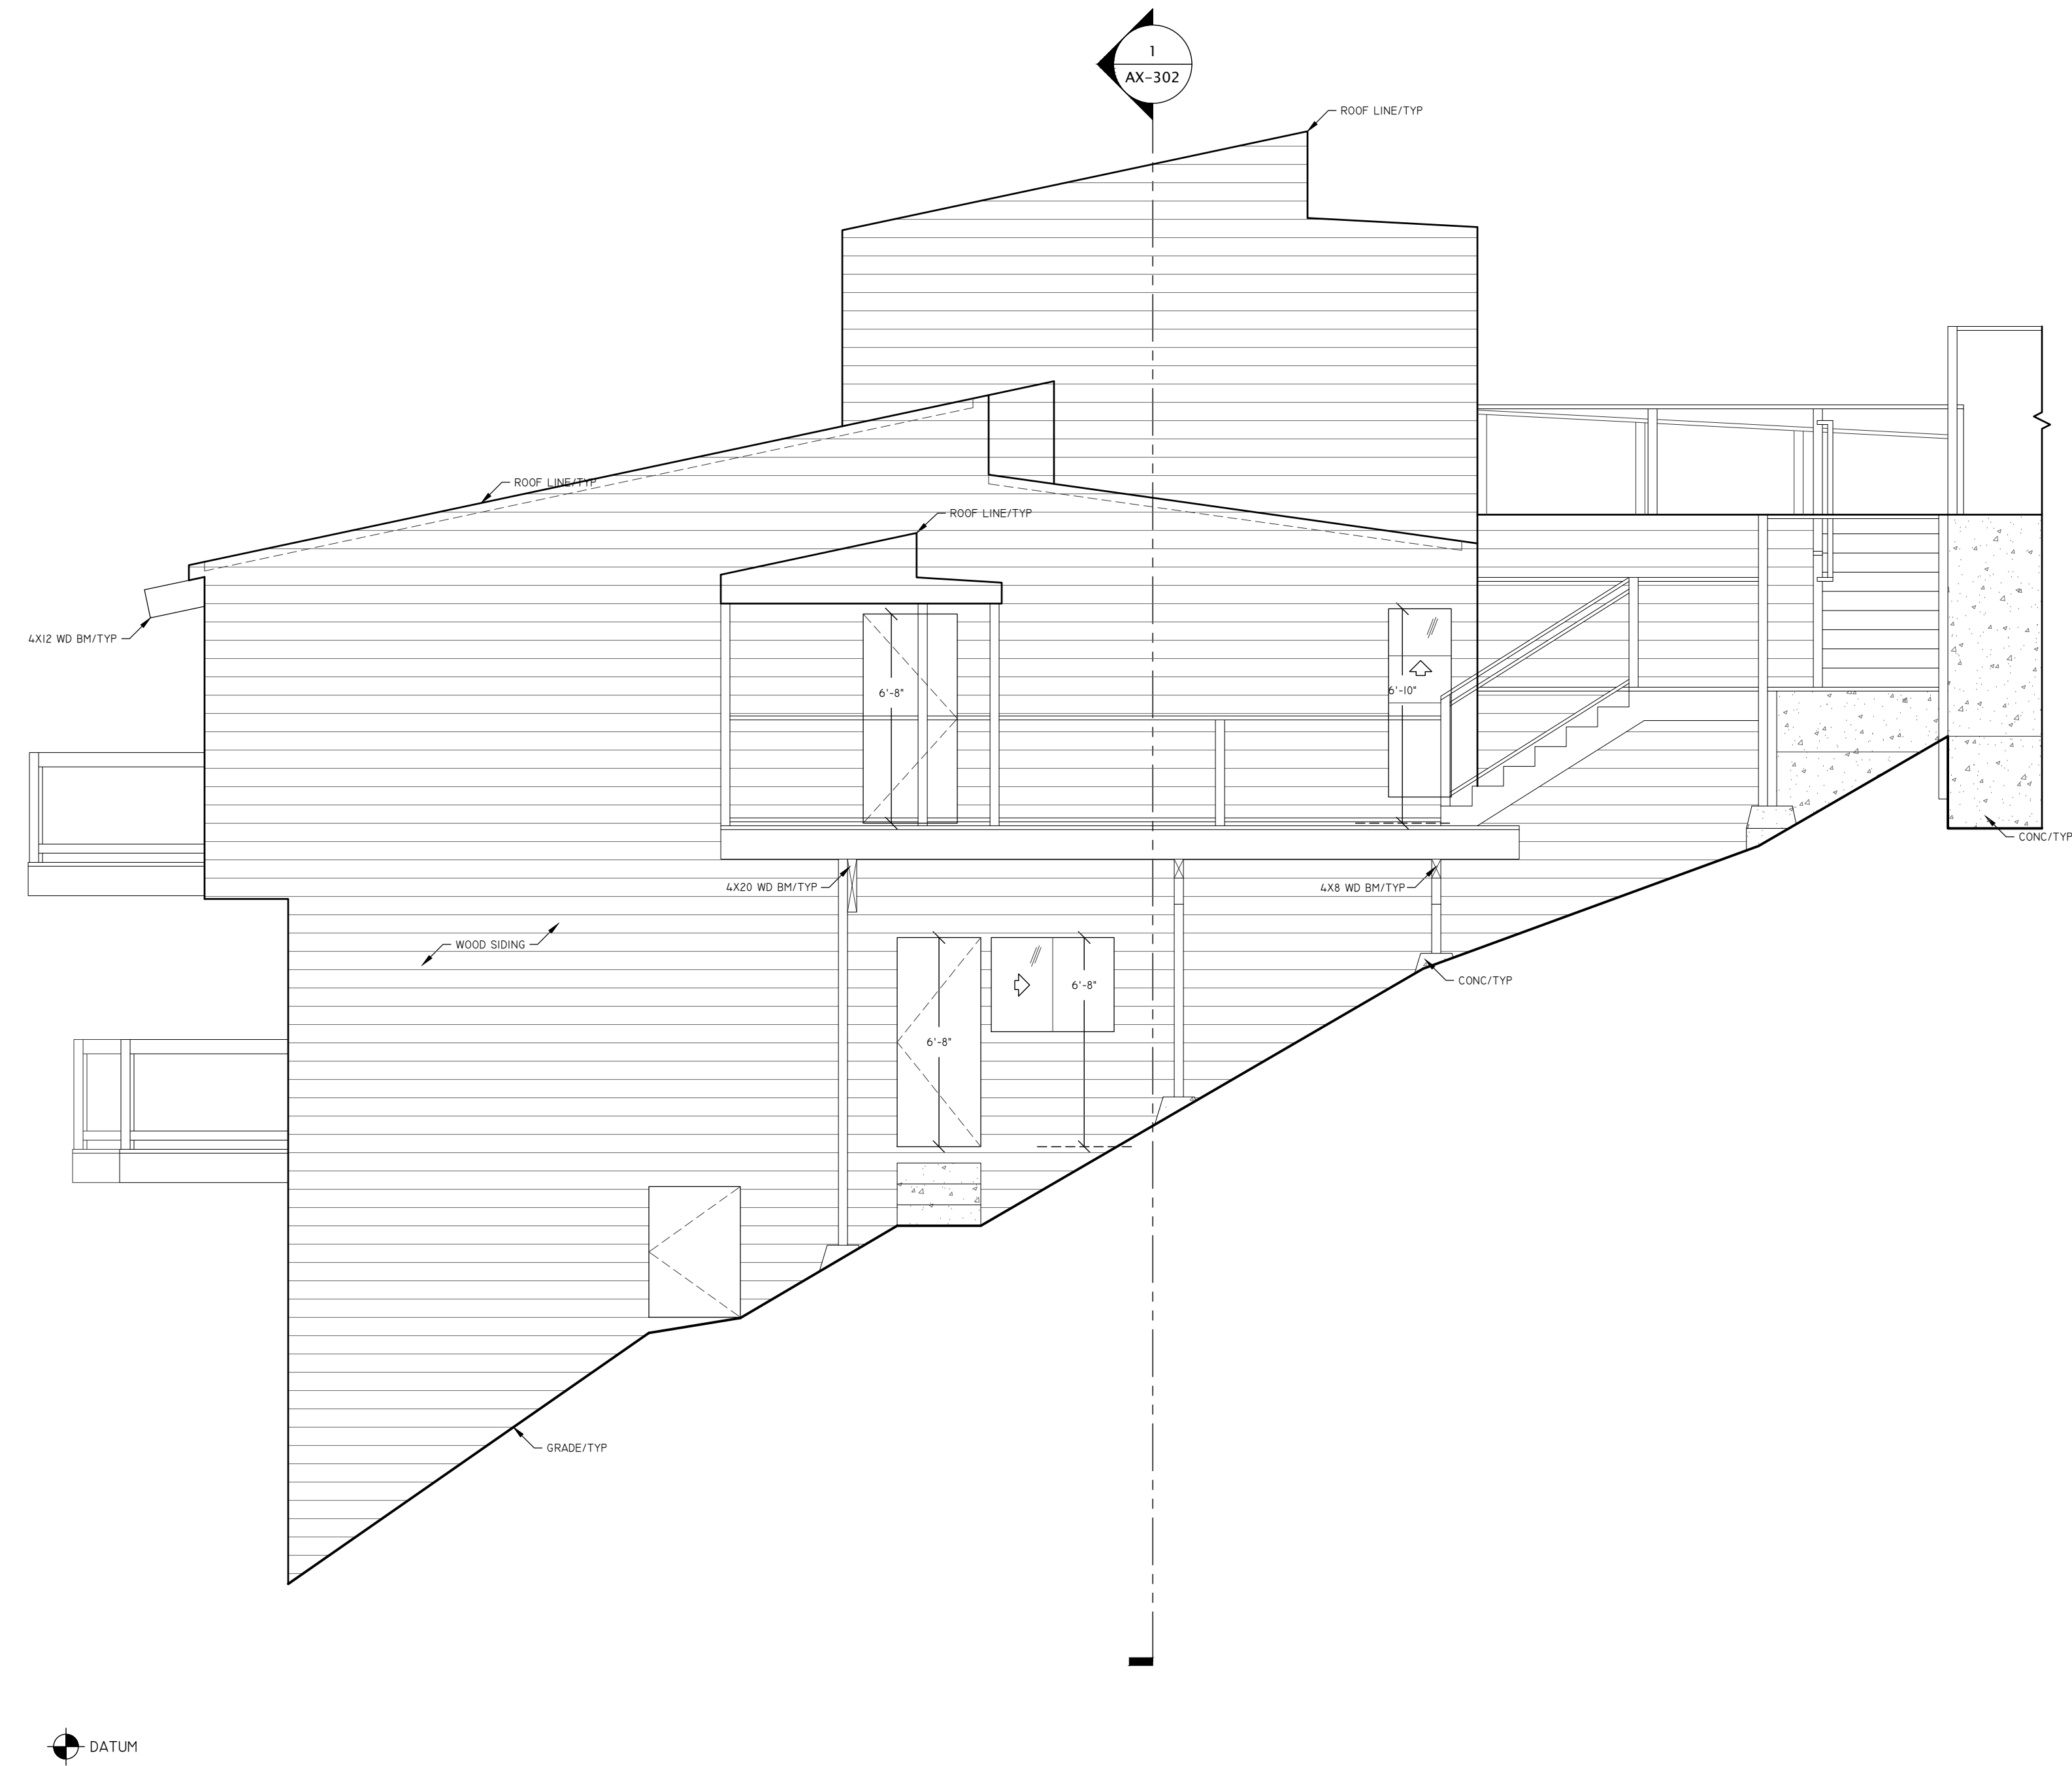

1 EXISTING SOUTH ELEVATION

THESE ARE BASIC ELEVATIONS.
NO BUILDING ORNAMENTATION SHOWN.

1839 MAGELLAN DRIVE OAKLAND, CA 94611		
THIS DRAWING IS A RECORD OF REAL PROPERTY THAT IS GENERALLY ACCEPTED TO BE SUITABLE FOR USE IN PLANNING, DESIGN, LEASE, AND GENERAL ASSET MANAGEMENT. IT SHOULD NOT BE USED TO DETERMINE EXACT MEASUREMENTS OF SPACES OR ARTIFACTS FOUND HEREIN FOR ANY PURPOSE. EXTERIOR ELEMENTS HAVE BEEN MEASURED AND DRAFTED FOR REFERENCE ONLY - THIS IS NOT A SURVEY.	 RED BRIDGE DESIGN SAN FRANCISCO REDBRIDGEDESIGN.COM	
EXISTING EXTERIOR ELEVATIONS		
REF: 1839sf_Oakland_SFD REV: 0 DRAWN BY: MV AUDITED BY: JK	SHEET SIZE: 24x36 SCALE: 1/4"=1'-0" FIELD MEASURE: 12/20/19	AX-201 5 OF 10

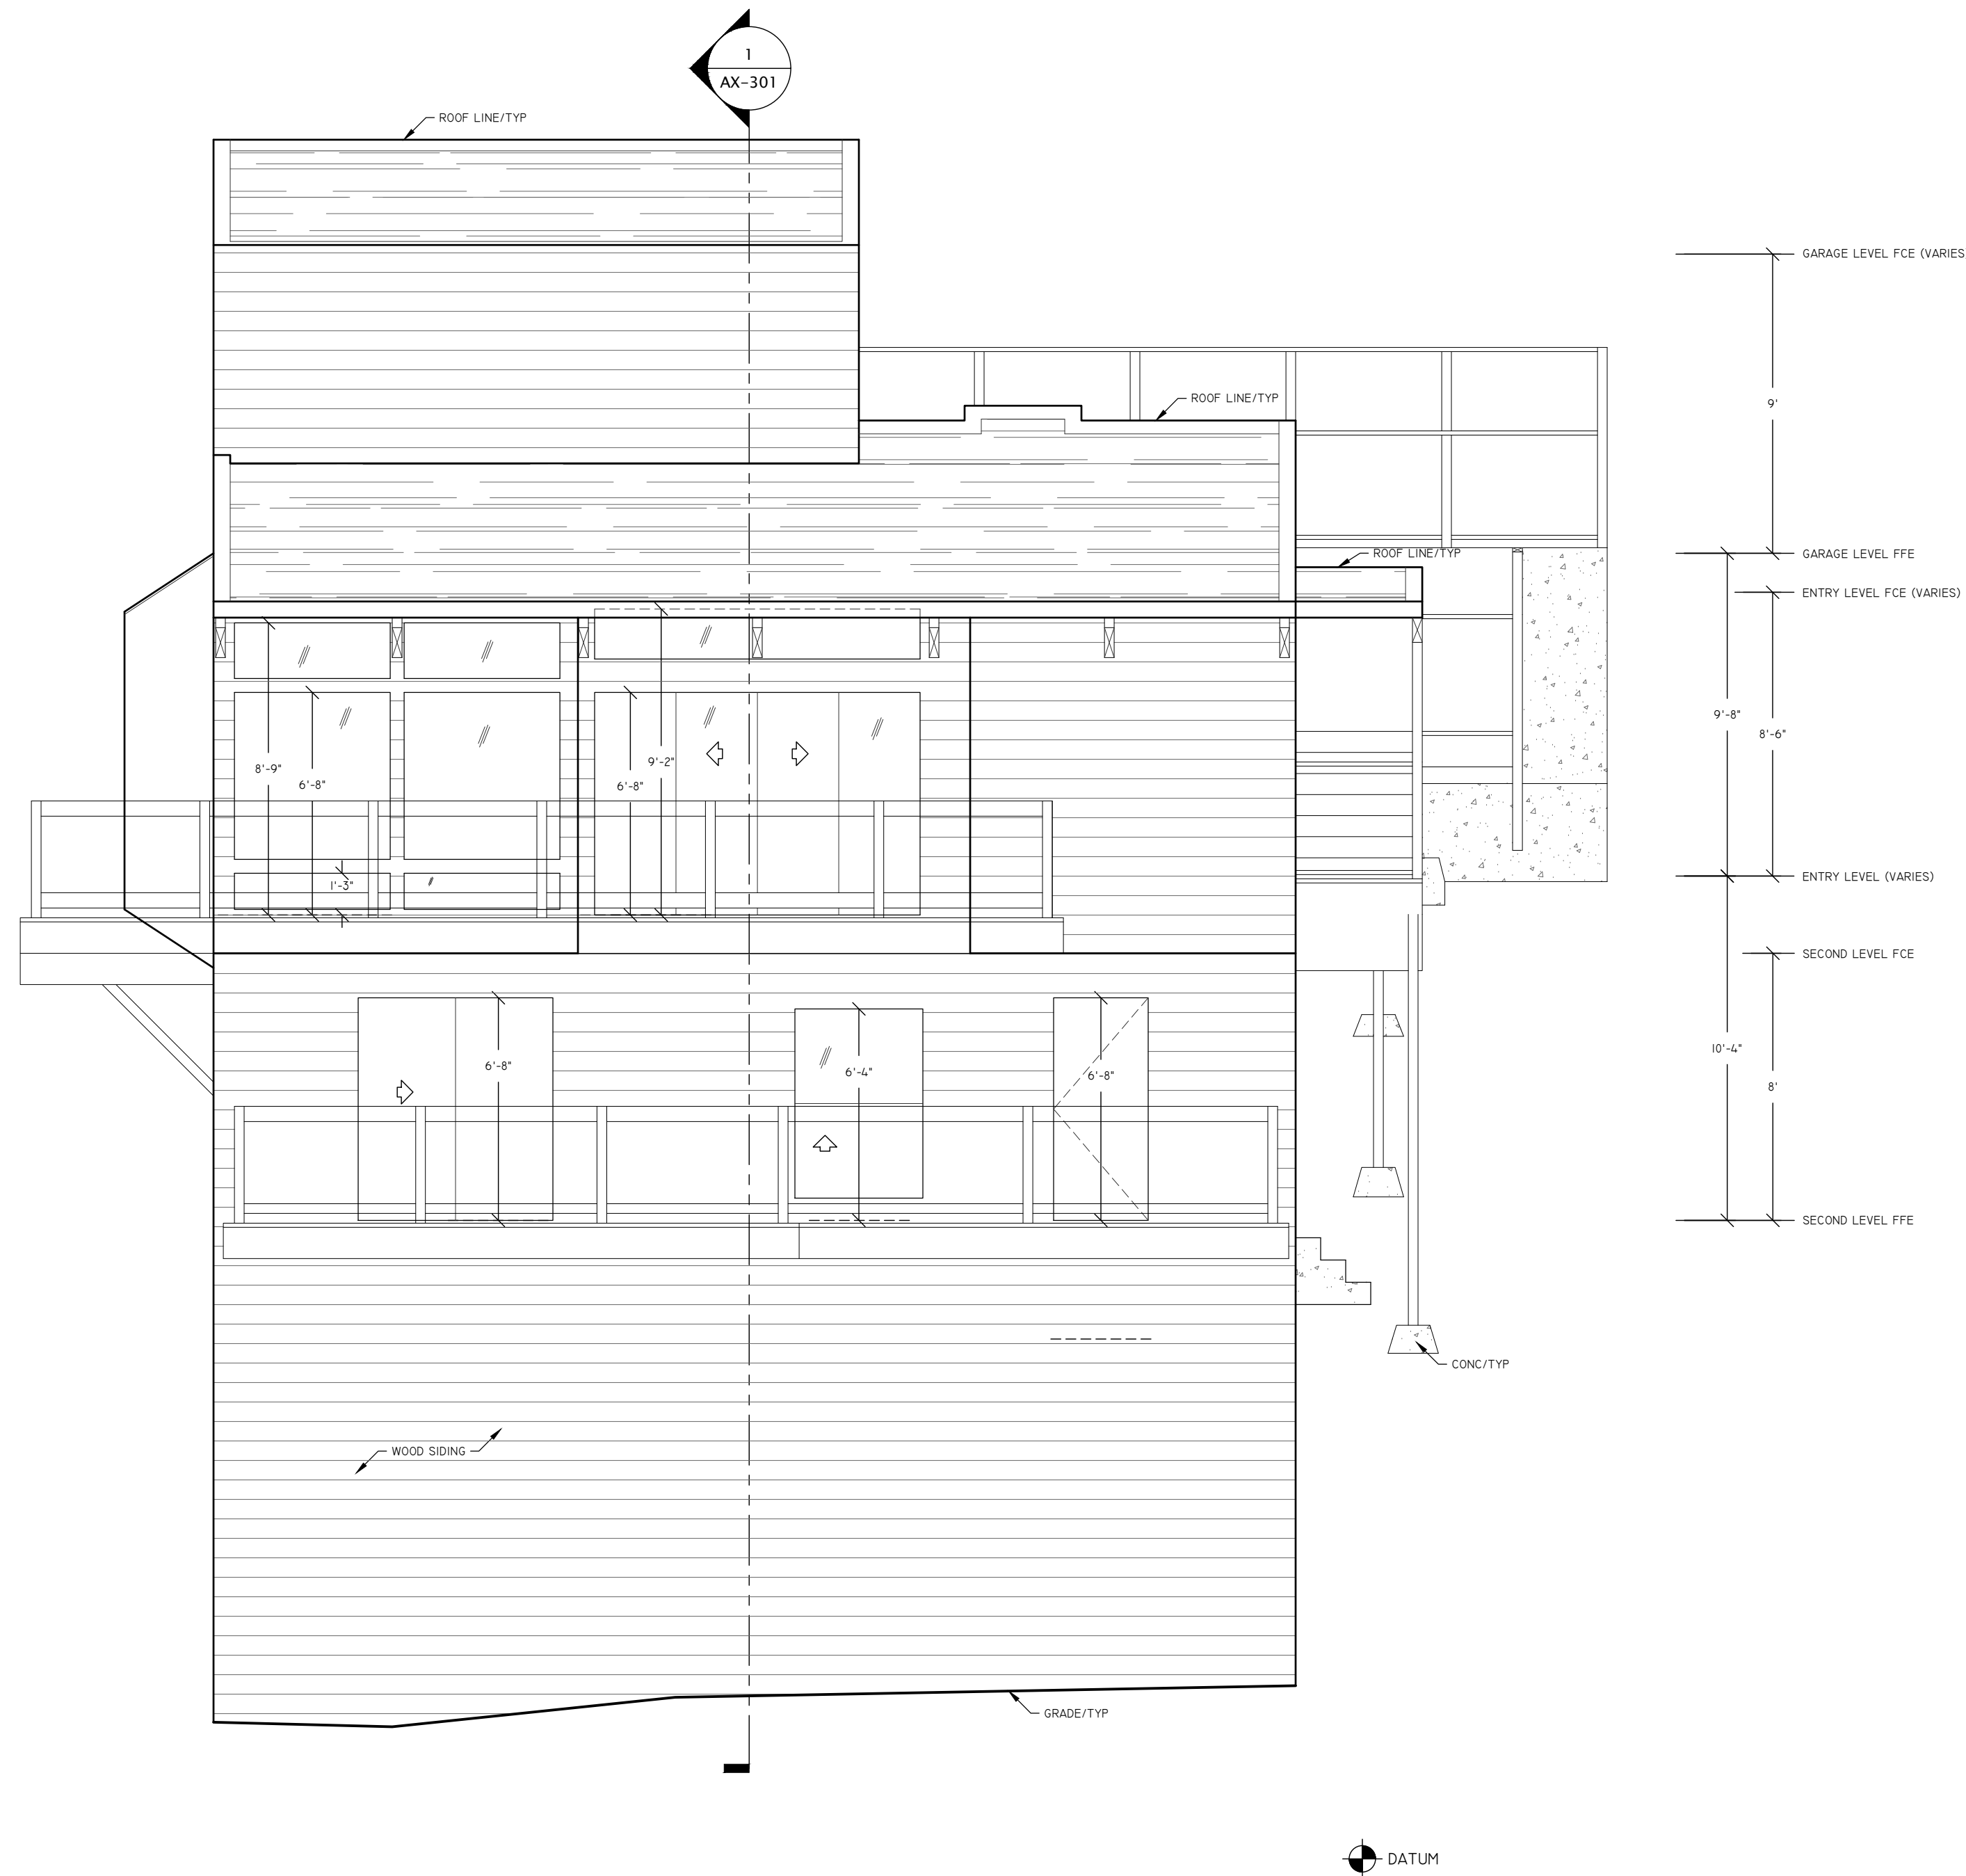

1 EXISTING WEST ELEVATION

THESE ARE BASIC ELEVATIONS.
NO BUILDING ORNAMENTATION SHOWN.

1839 MAGELLAN DRIVE
OAKLAND, CA 94611

THIS DRAWING IS A RECORD OF REAL PROPERTY
THAT IS GENERALLY ACCEPTED TO BE SUITABLE
FOR USE IN PLANNING, DESIGN, LEASE, AND
GENERAL ASSET MANAGEMENT. IT SHOULD NOT BE
USED TO DETERMINE EXACT MEASUREMENTS OF
SPACES OR ARTIFACTS FOUND HEREIN FOR ANY
PURPOSE.
EXTERIOR ELEMENTS HAVE BEEN MEASURED AND
DRAFTED FOR REFERENCE ONLY - THIS IS NOT A
SURVEY.



EXISTING EXTERIOR ELEVATIONS

REF: 1839sf_Oakland_SFD
REV: 0
DRAWN BY: MV
AUDITED BY: JK

SHEET SIZE: 24x36
SCALE: 1/4"=1'-0"
FIELD MEASURE:
12/20/19

AX-202
6 OF 10



THIS DRAWING IS A RECORD OF REAL PROPERTY THAT IS GENERALLY ACCEPTED TO BE SUITABLE FOR USE IN PLANNING, DESIGN, LEASE, AND GENERAL ASSET MANAGEMENT. IT SHOULD NOT BE USED TO DETERMINE EXACT MEASUREMENTS OF SPACES OR ARTIFACTS FOUND HEREIN FOR ANY PURPOSE.

EXTERIOR ELEMENTS HAVE BEEN MEASURED AND DRAFTED FOR REFERENCE ONLY - THIS IS NOT A SURVEY.




EXISTING EXTERIOR ELEVATIONS

SHEET SIZE: 24x36
SCALE: 1/4"=1'-0"
FIELD MEASURE:
12/20/19

AX-203
7 OF 10


1 EXISTING NORTH ELEVATION

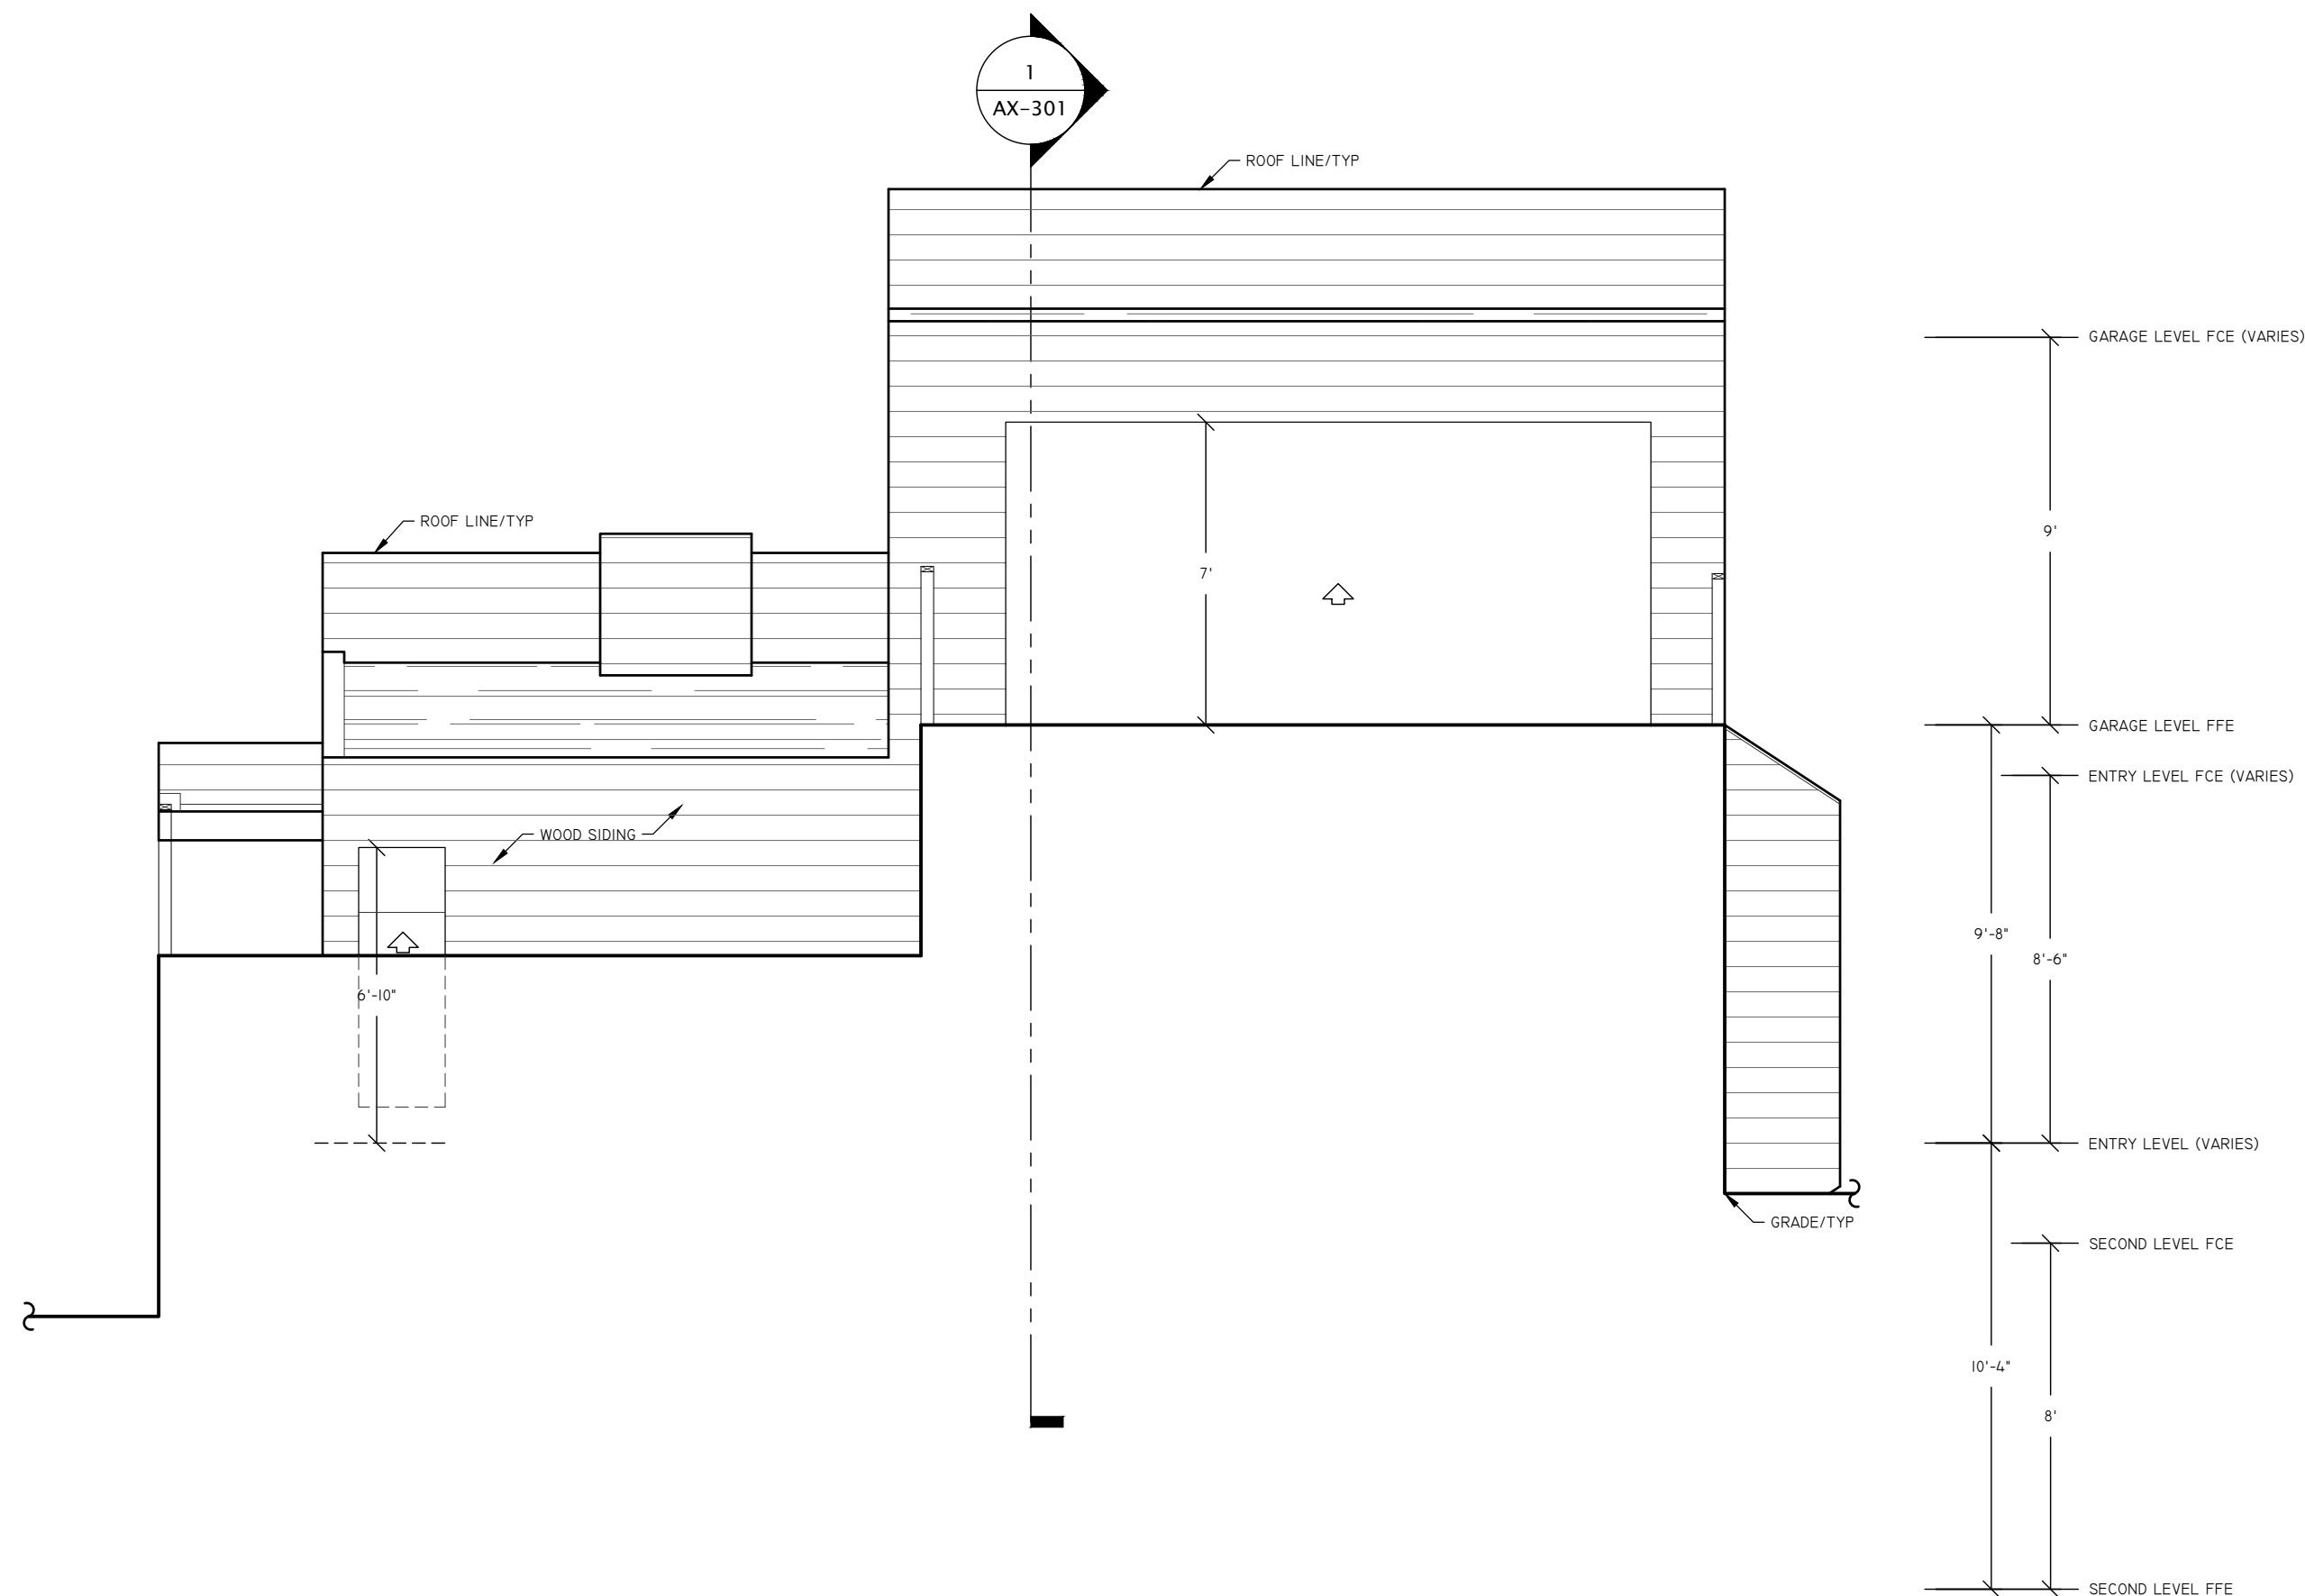

1 EXISTING EAST ELEVATION

THESE ARE BASIC ELEVATIONS.
NO BUILDING ORNAMENTATION SHOWN.

1839 MAGELLAN DRIVE OAKLAND, CA 94611		
THIS DRAWING IS A RECORD OF REAL PROPERTY THAT IS GENERALLY ACCEPTED TO BE SUITABLE FOR USE IN PLANNING, DESIGN, LEASE, AND GENERAL ASSET MANAGEMENT. IT SHOULD NOT BE USED TO DETERMINE EXACT MEASUREMENTS OF SPACES OR ARTIFACTS FOUND HEREIN FOR ANY PURPOSE.	 RED BRIDGE DESIGN SAN FRANCISCO REDBRIDGEDESIGN.COM	
EXISTING EXTERIOR ELEVATIONS		
REF: 1839sf_Oakland_SFD REV: 0 DRAWN BY: MV AUDITED BY: JK	SHEET SIZE: 24x36 SCALE: 1/4"=1'-0" FIELD MEASURE: 12/20/19	AX-204 8 OF 10

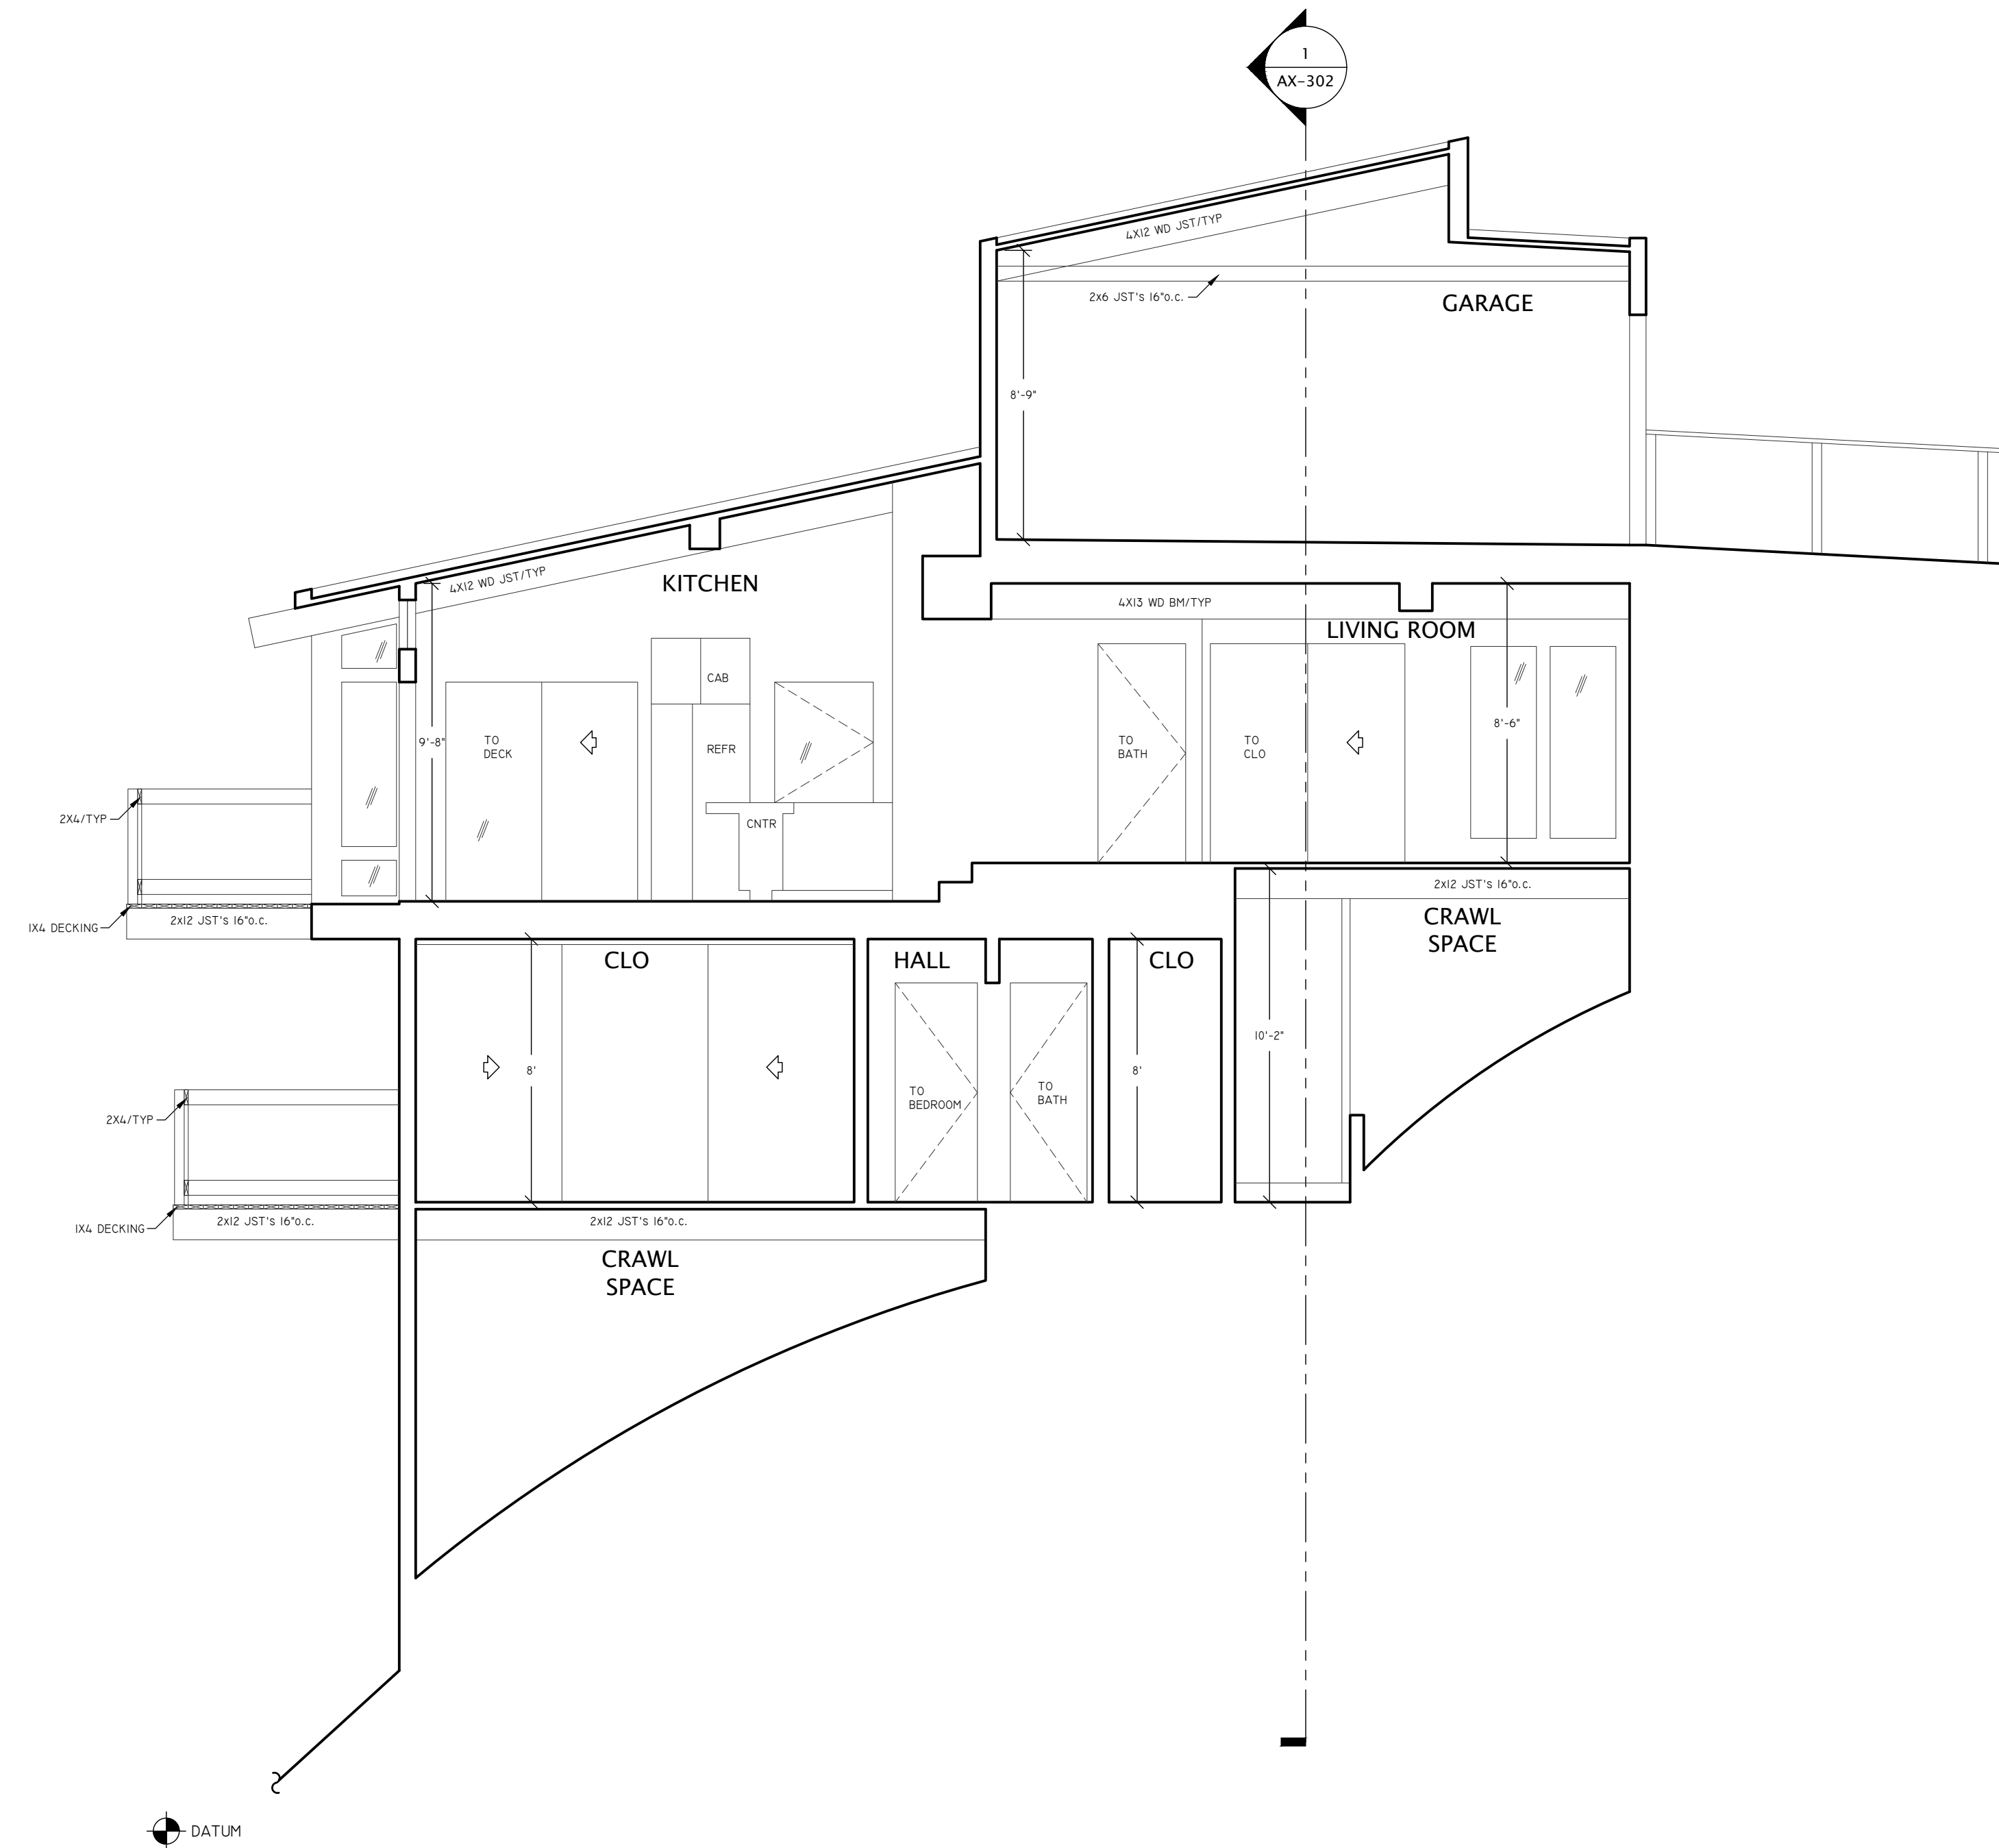

1 EXISTING LONGITUDINAL SECTION

1839 MAGELLAN DRIVE
OAKLAND, CA 94611

THIS DRAWING IS A RECORD OF REAL PROPERTY
THAT IS GENERALLY ACCEPTED TO BE SUITABLE
FOR USE IN PLANNING, DESIGN, LEASE, AND
GENERAL ASSET MANAGEMENT. IT SHOULD NOT BE
USED TO DETERMINE EXACT MEASUREMENTS OF
SPACES OR ARTIFACTS FOUND HEREIN FOR ANY
PURPOSE.
EXTERIOR ELEMENTS HAVE BEEN MEASURED AND
DRAFTED FOR REFERENCE ONLY - THIS IS NOT A
SURVEY.




EXISTING BUILDING SECTIONS

REF: 1839sf_Oakland_SFD
REV: 0
DRAWN BY: MV
AUDITED BY: JK

SHEET SIZE: 24x36
SCALE: 1/4"=1'-0"
FIELD MEASURE:
12/20/19

AX-301
9 OF 10

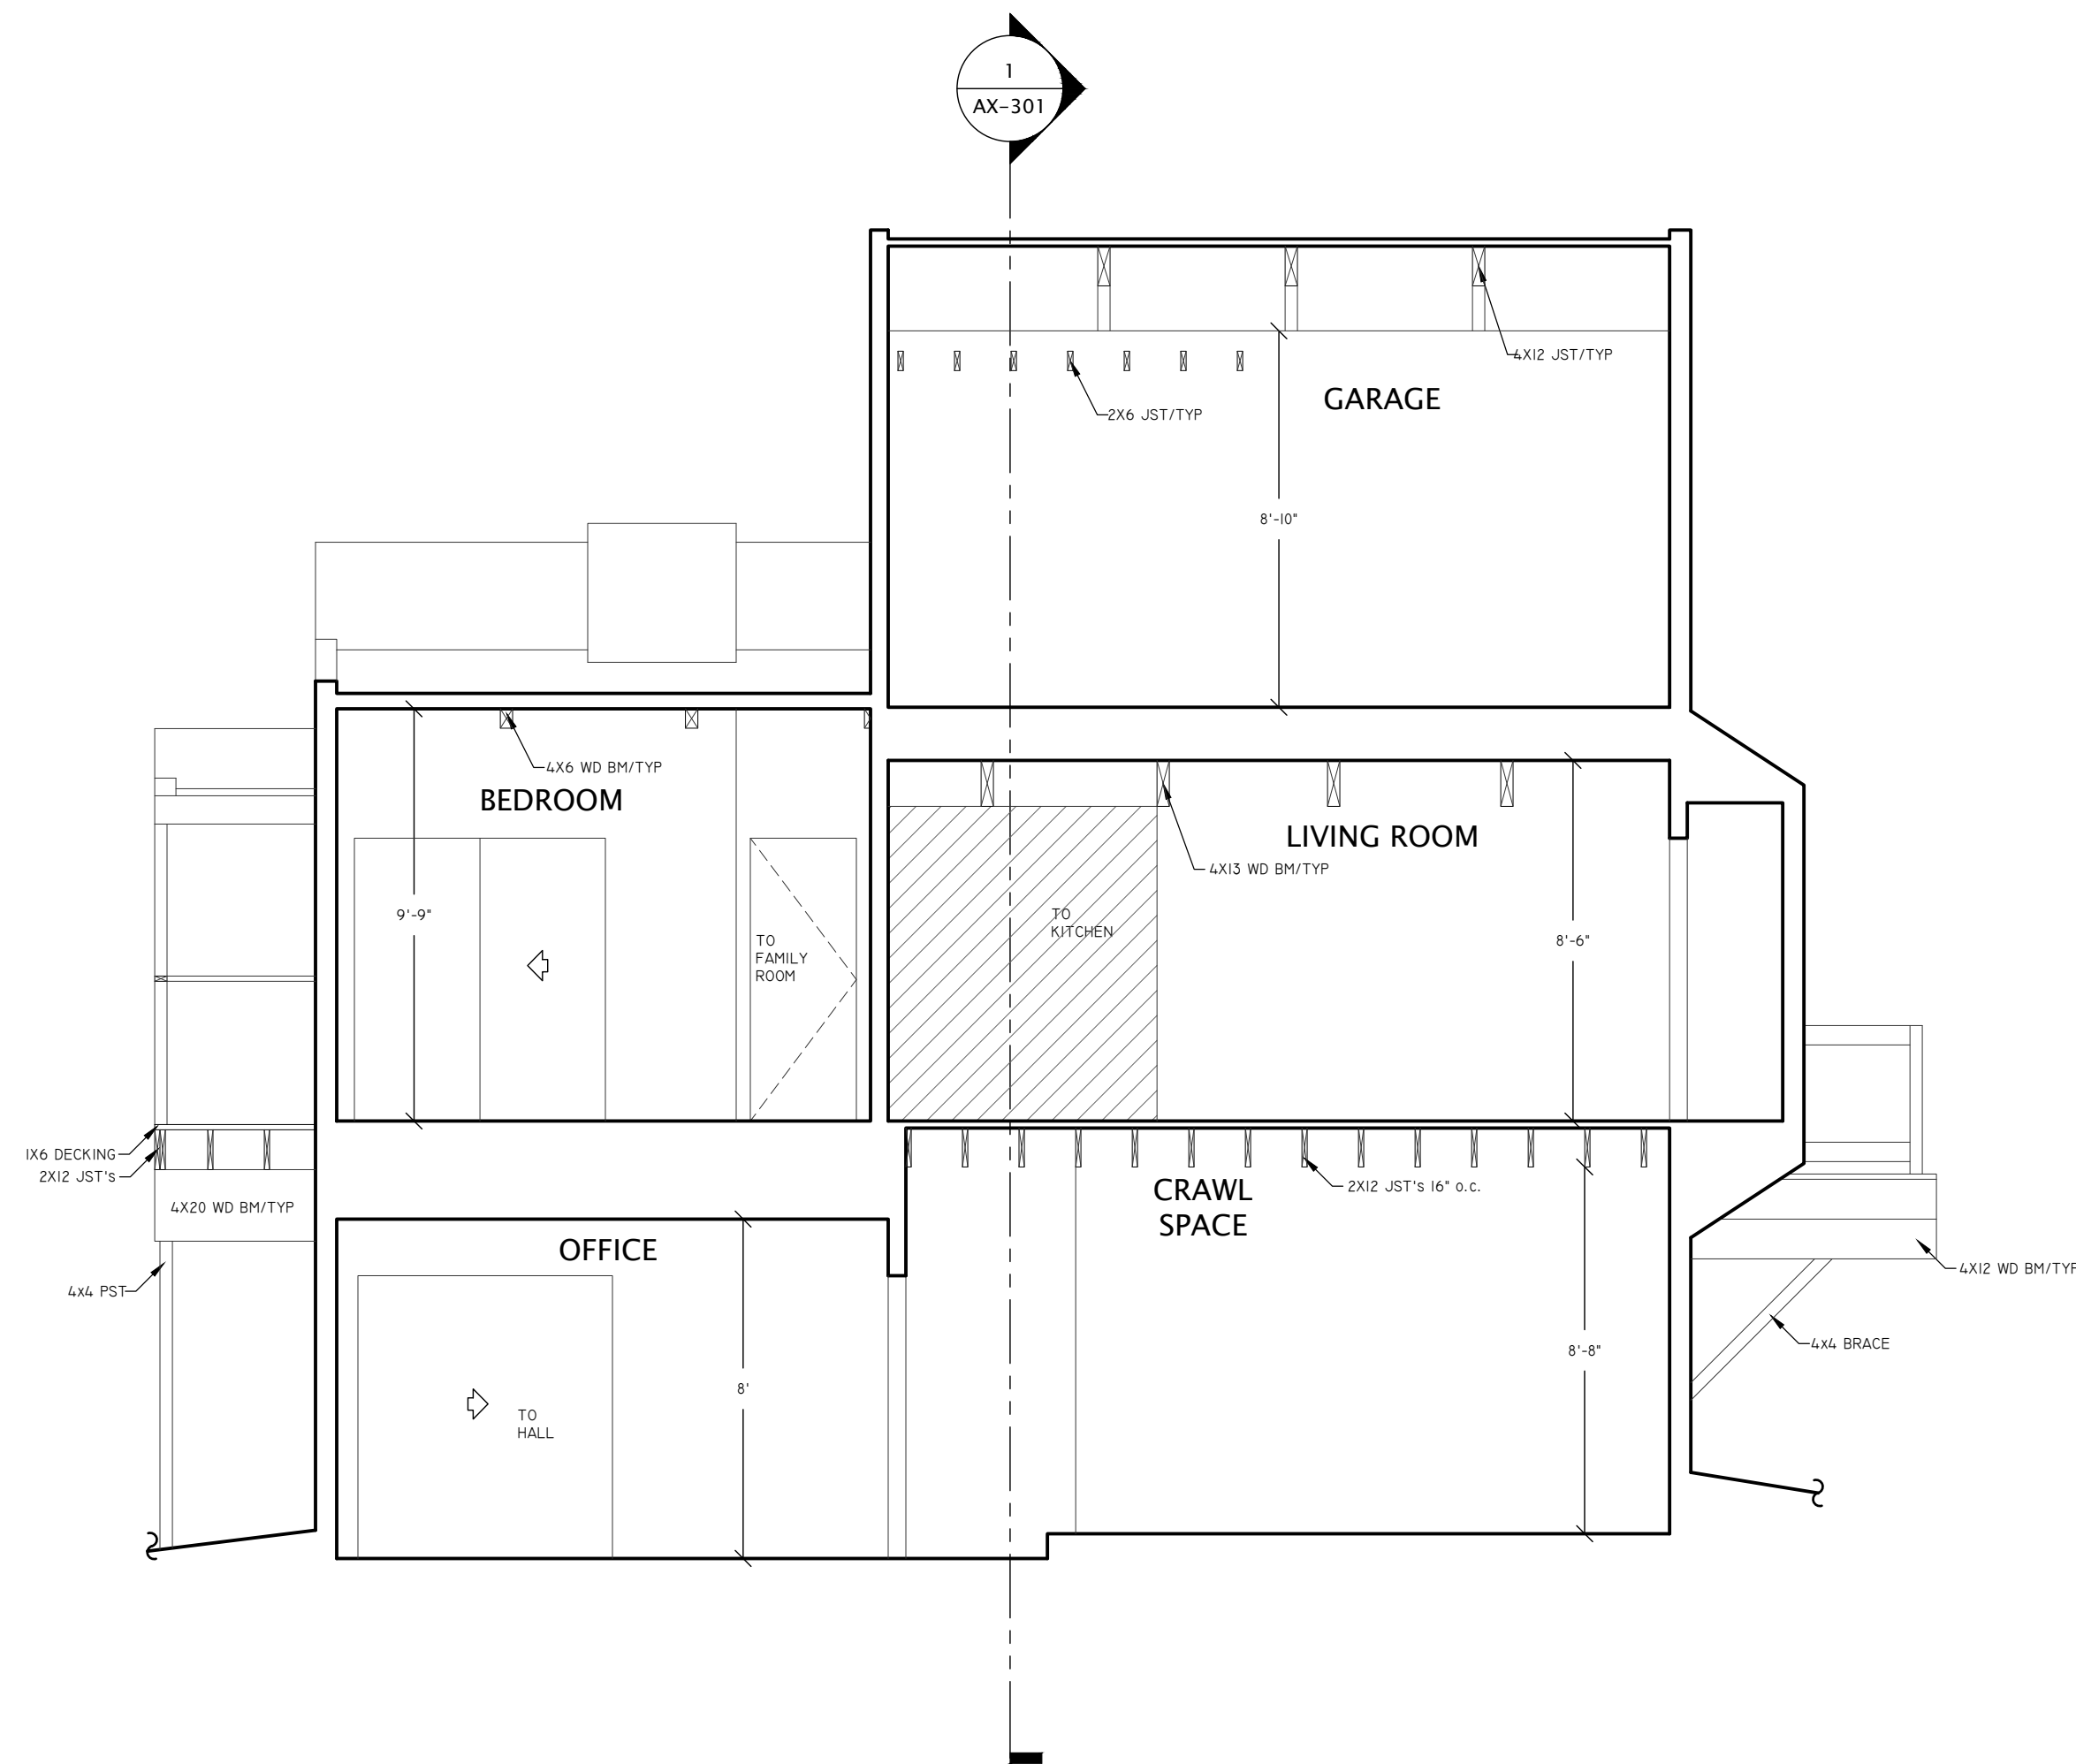

1 EXISTING CROSS SECTION

1839 MAGELLAN DRIVE OAKLAND, CA 94611		
THIS DRAWING IS A RECORD OF REAL PROPERTY THAT IS GENERALLY ACCEPTED TO BE SUITABLE FOR USE IN PLANNING, DESIGN, LEASE, AND GENERAL ASSET MANAGEMENT. IT SHOULD NOT BE USED TO DETERMINE EXACT MEASUREMENTS OF SPACES OR ARTIFACTS FOUND HEREIN FOR ANY PURPOSE. EXTERIOR ELEMENTS HAVE BEEN MEASURED AND DRAFTED FOR REFERENCE ONLY - THIS IS NOT A SURVEY.		
 RED BRIDGE DESIGN SAN FRANCISCO REDBRIDGEDESIGN.COM		
EXISTING BUILDING SECTIONS		
REF: 1839sf_Oakland_SFD REV: 0 DRAWN BY: MV AUDITED BY: JK	SHEET SIZE: 24x36 SCALE: 1/4"=1'-0" FIELD MEASURE: 12/20/19	AX-302 10 OF 10