




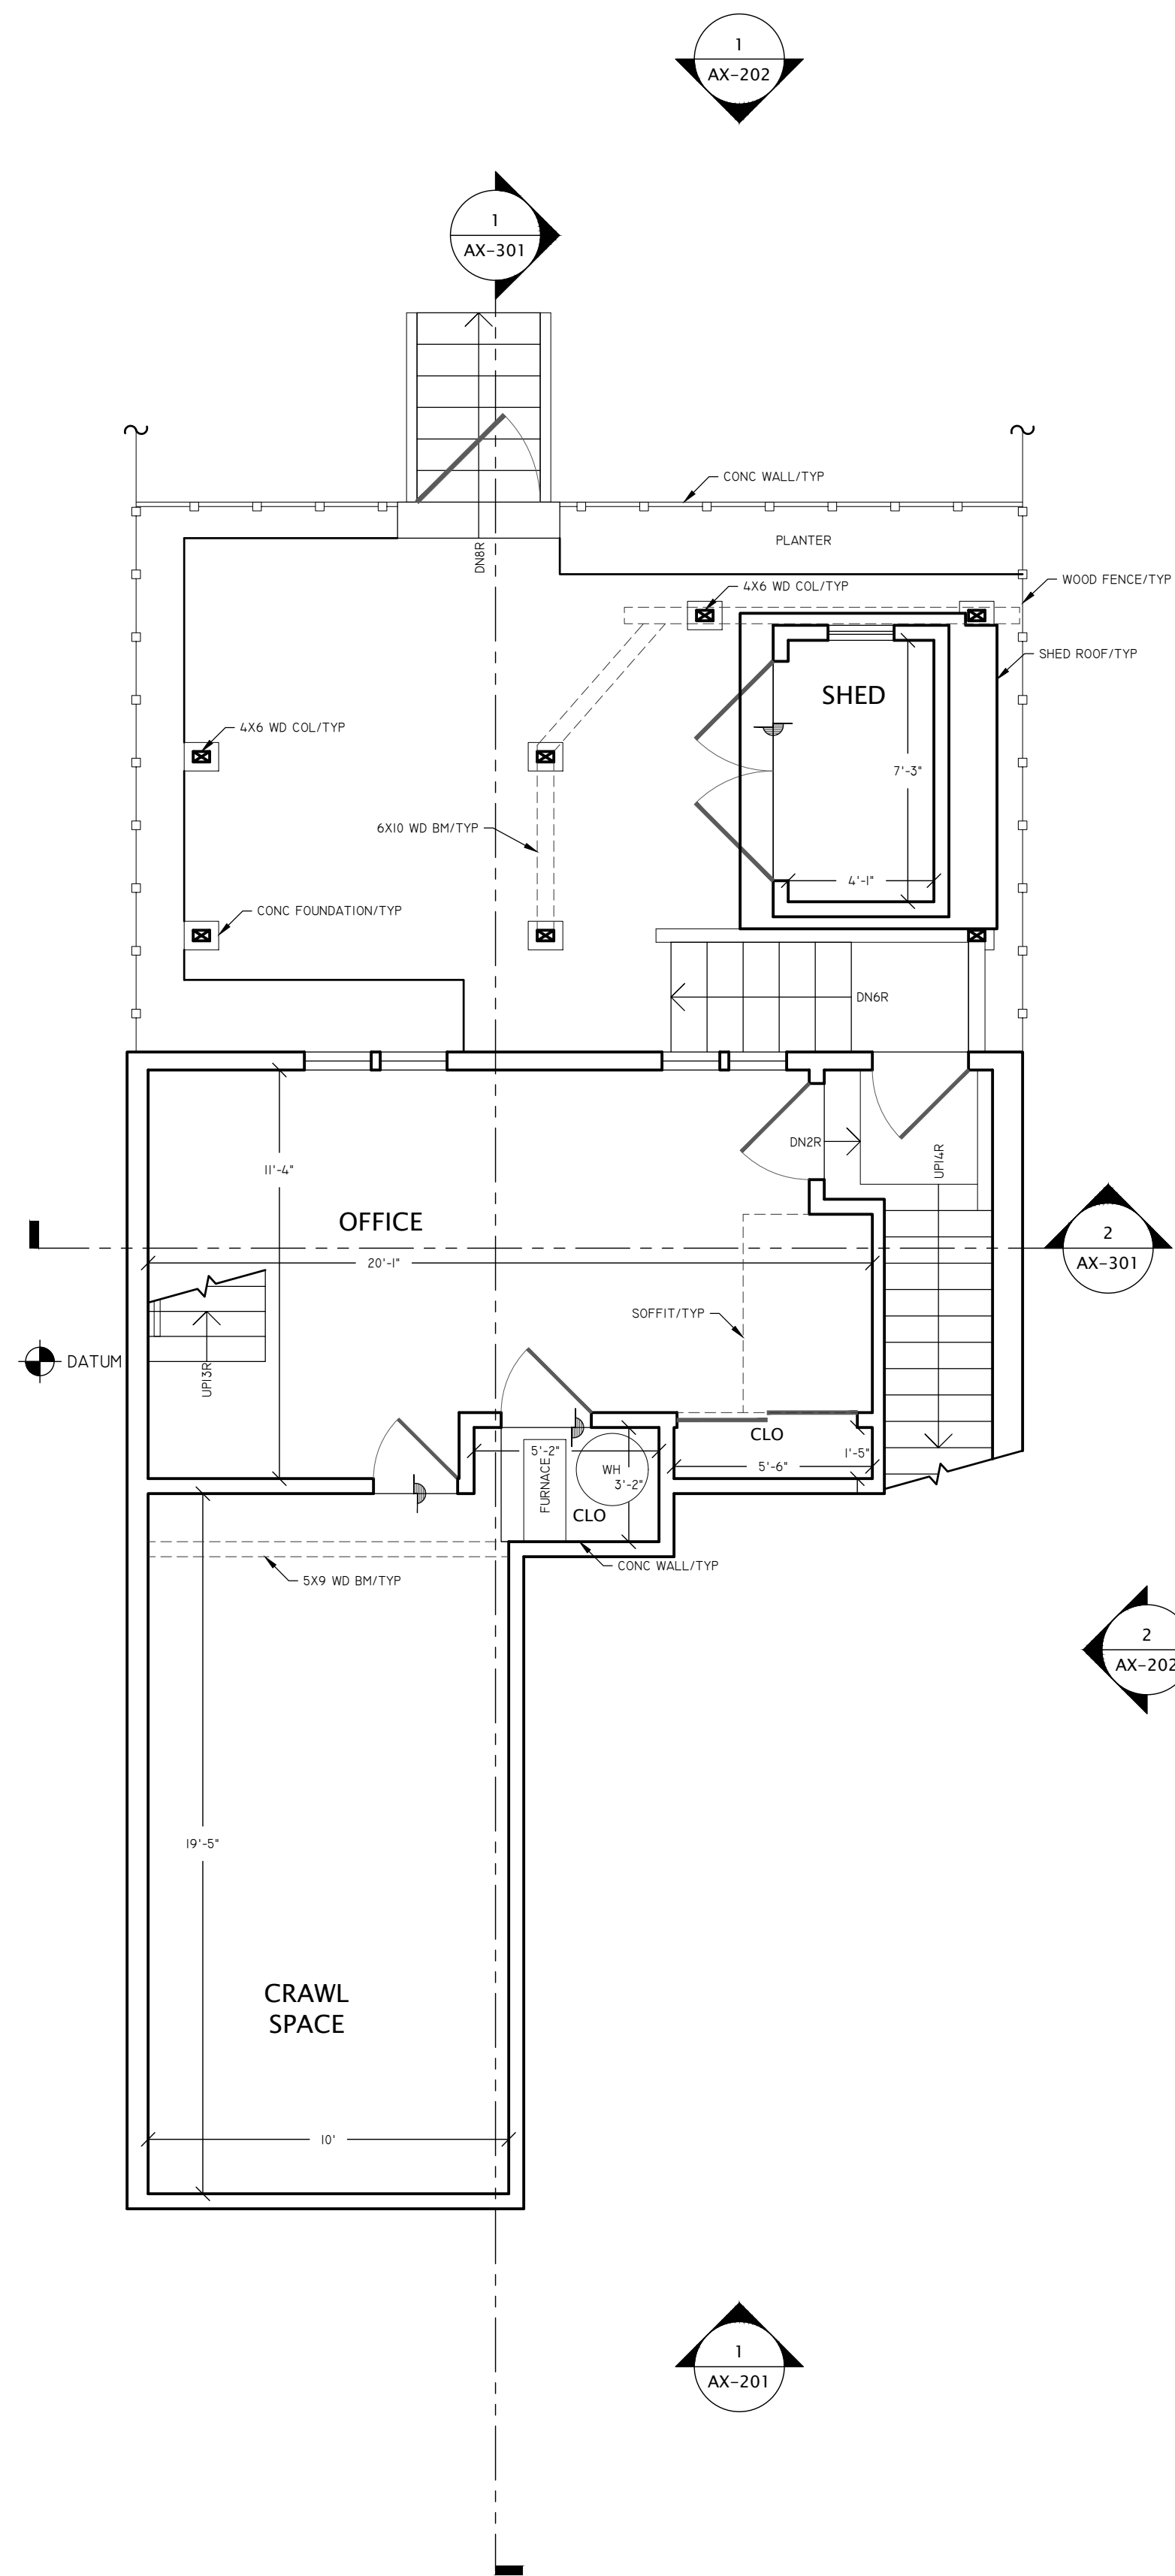

1 EXISTING LOWER LEVEL FLOOR PLAN
566 SQFT CROSS MEASURED AREA
357 SQFT MEASURED EXTERIOR SURFACES

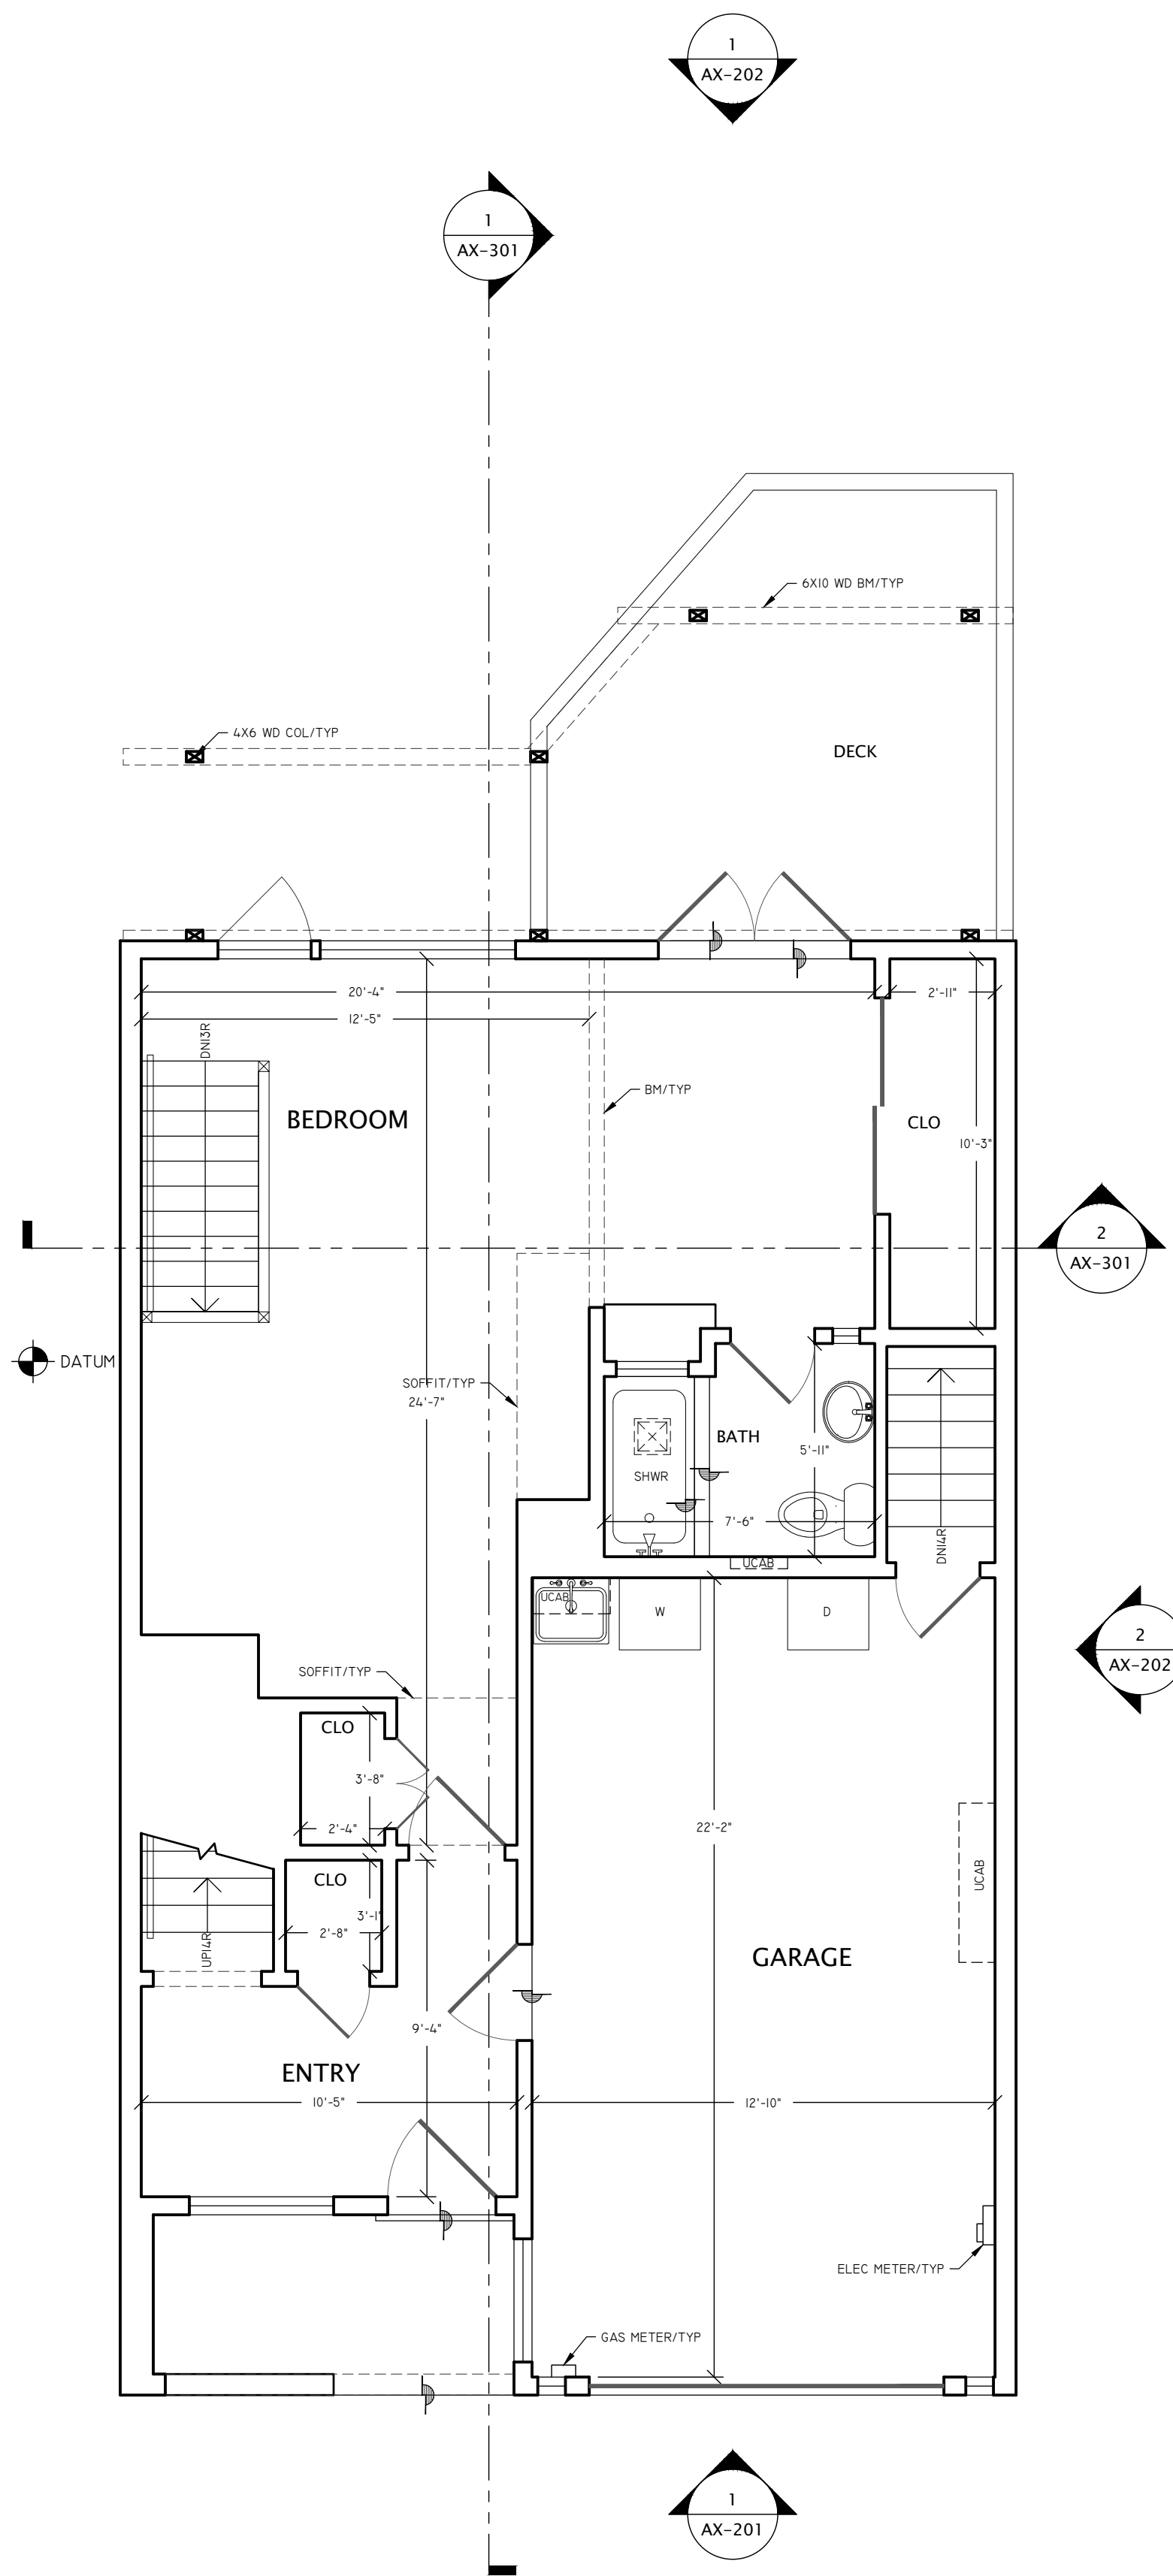

2 EXISTING ENTRY LEVEL FLOOR PLAN
955 SQFT CROSS MEASURED AREA
200 SQFT MEASURED EXTERIOR SURFACES

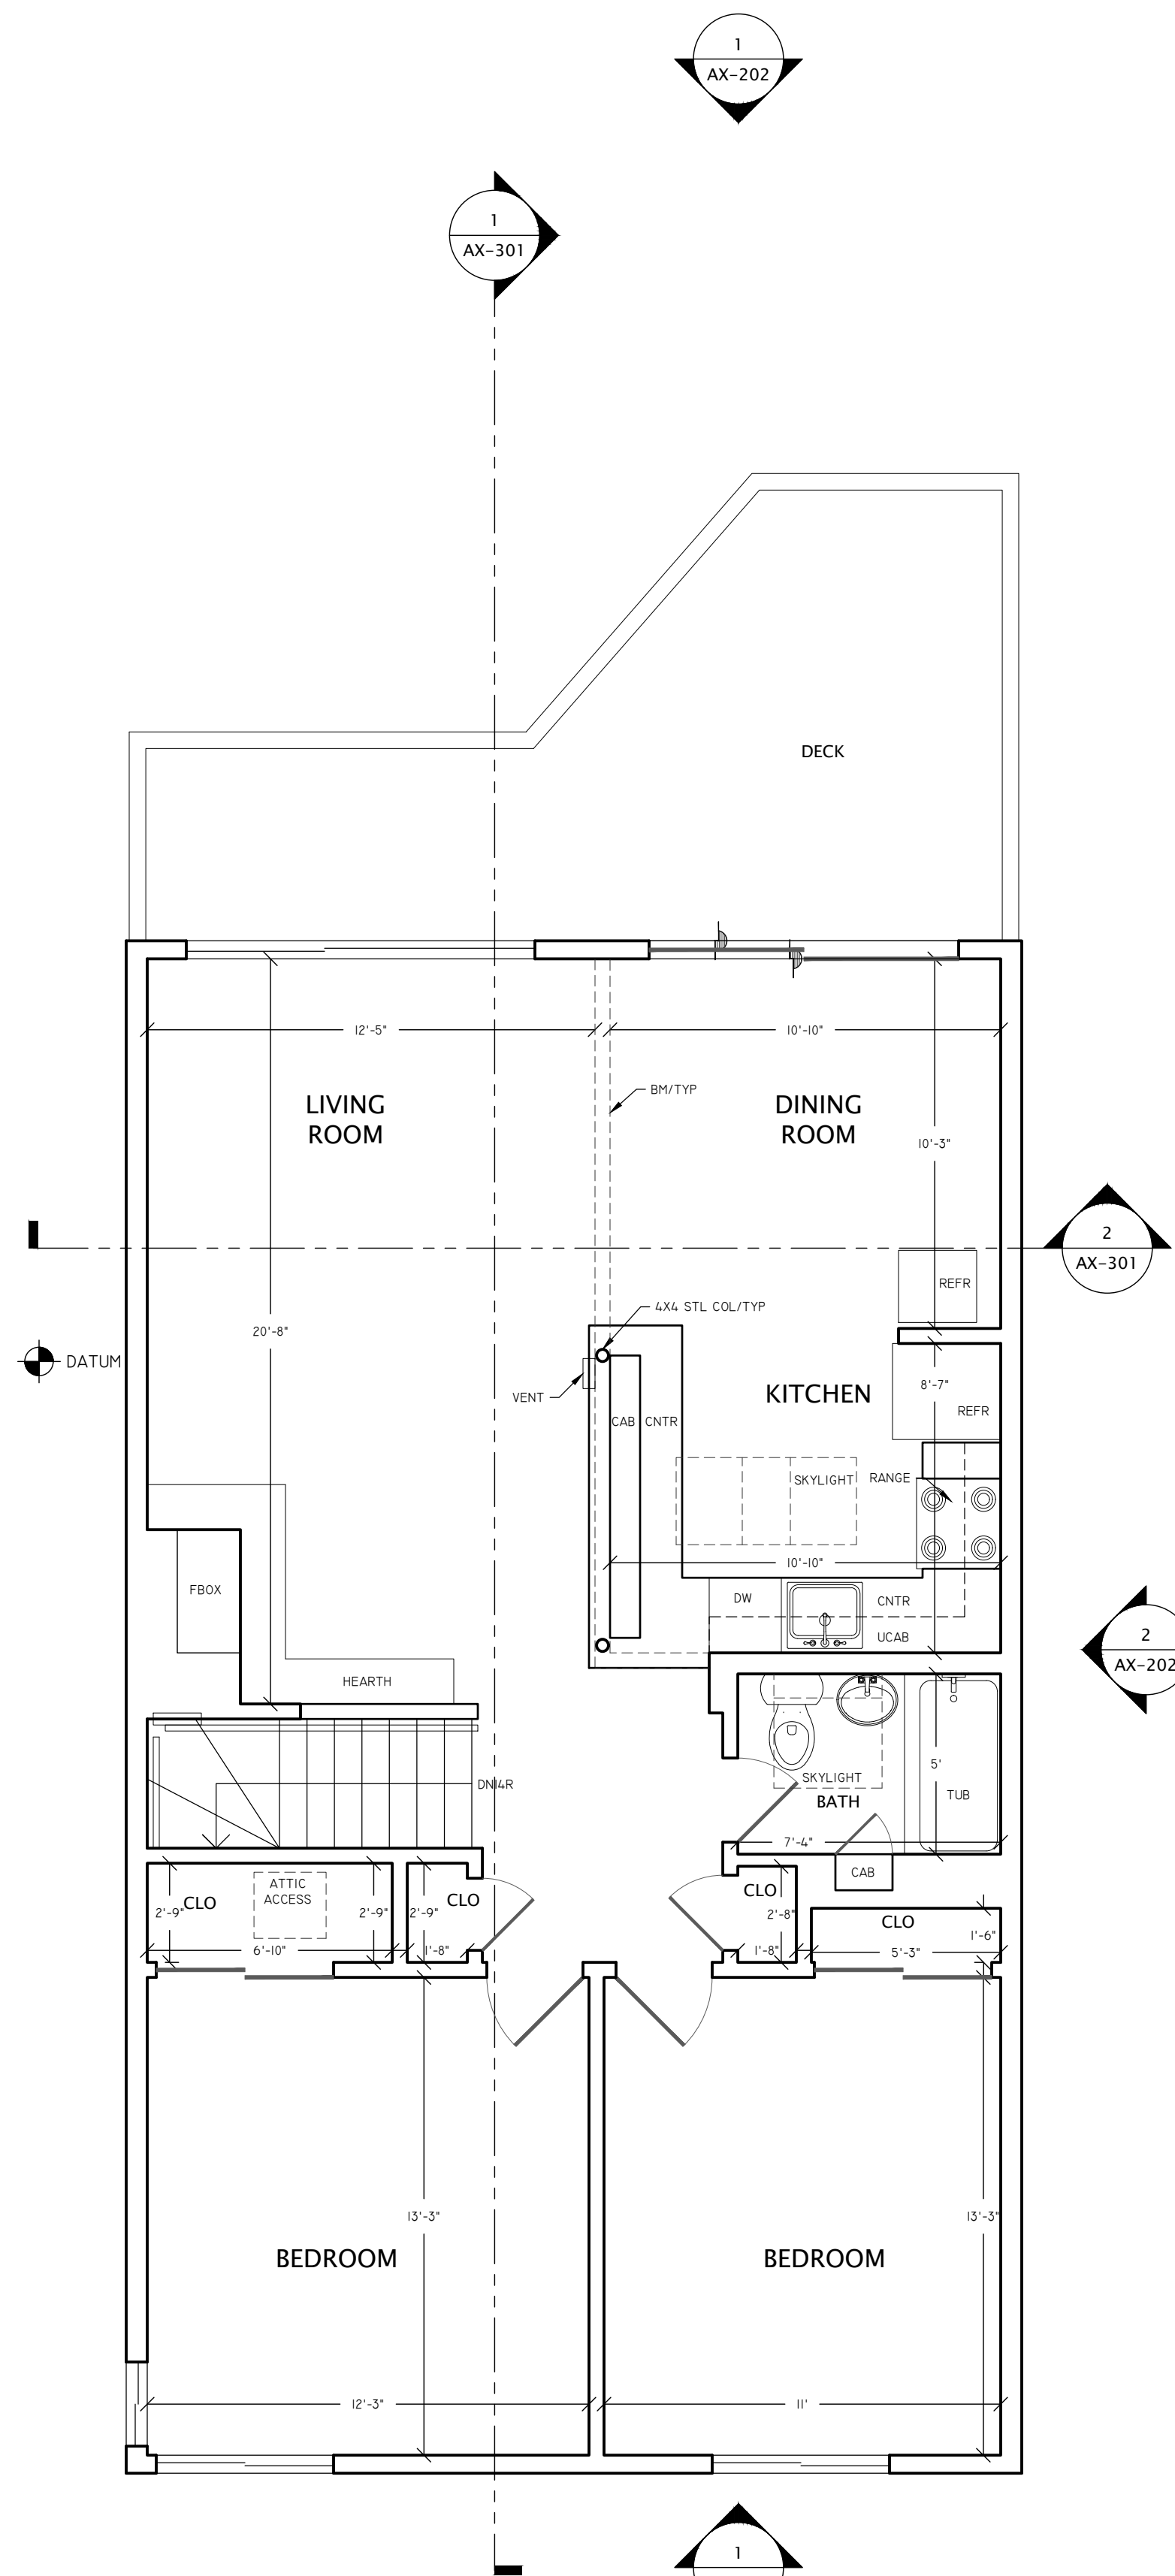

3 EXISTING SECOND LEVEL FLOOR PLAN
1,055 SQFT CROSS MEASURED AREA
218 SQFT MEASURED EXTERIOR SURFACES

LEGEND	
	HVAC CEILING REGISTER

27 SATURN STREET
SAN FRANCISCO, CA 94114

THIS DRAWING IS A RECORD OF REAL PROPERTY THAT IS GENERALLY ACCEPTED TO BE SUITABLE FOR USE IN PLANNING, DESIGN, LEASE, AND GENERAL ASSET MANAGEMENT. IT SHOULD NOT BE USED TO DETERMINE EXACT MEASUREMENTS OF SPACES OR ARTIFACTS FOUND HEREIN FOR ANY PURPOSE.

EXTERIOR ELEMENTS HAVE BEEN MEASURED AND DRAFTED FOR REFERENCE ONLY - THIS IS NOT A SURVEY.


RED BRIDGE DESIGN
SAN FRANCISCO
REDBRIDGEDESIGN.COM

EXISTING FLOOR PLAN


REF: 27sf_City_SFD
REV: 0
DRAWN BY: MV
AUDITED BY: JK

SHEET SIZE: 24x36
SCALE: 1/4"=1'-0"
FIELD MEASURE:
10/7/19

AX-101
1 OF 4

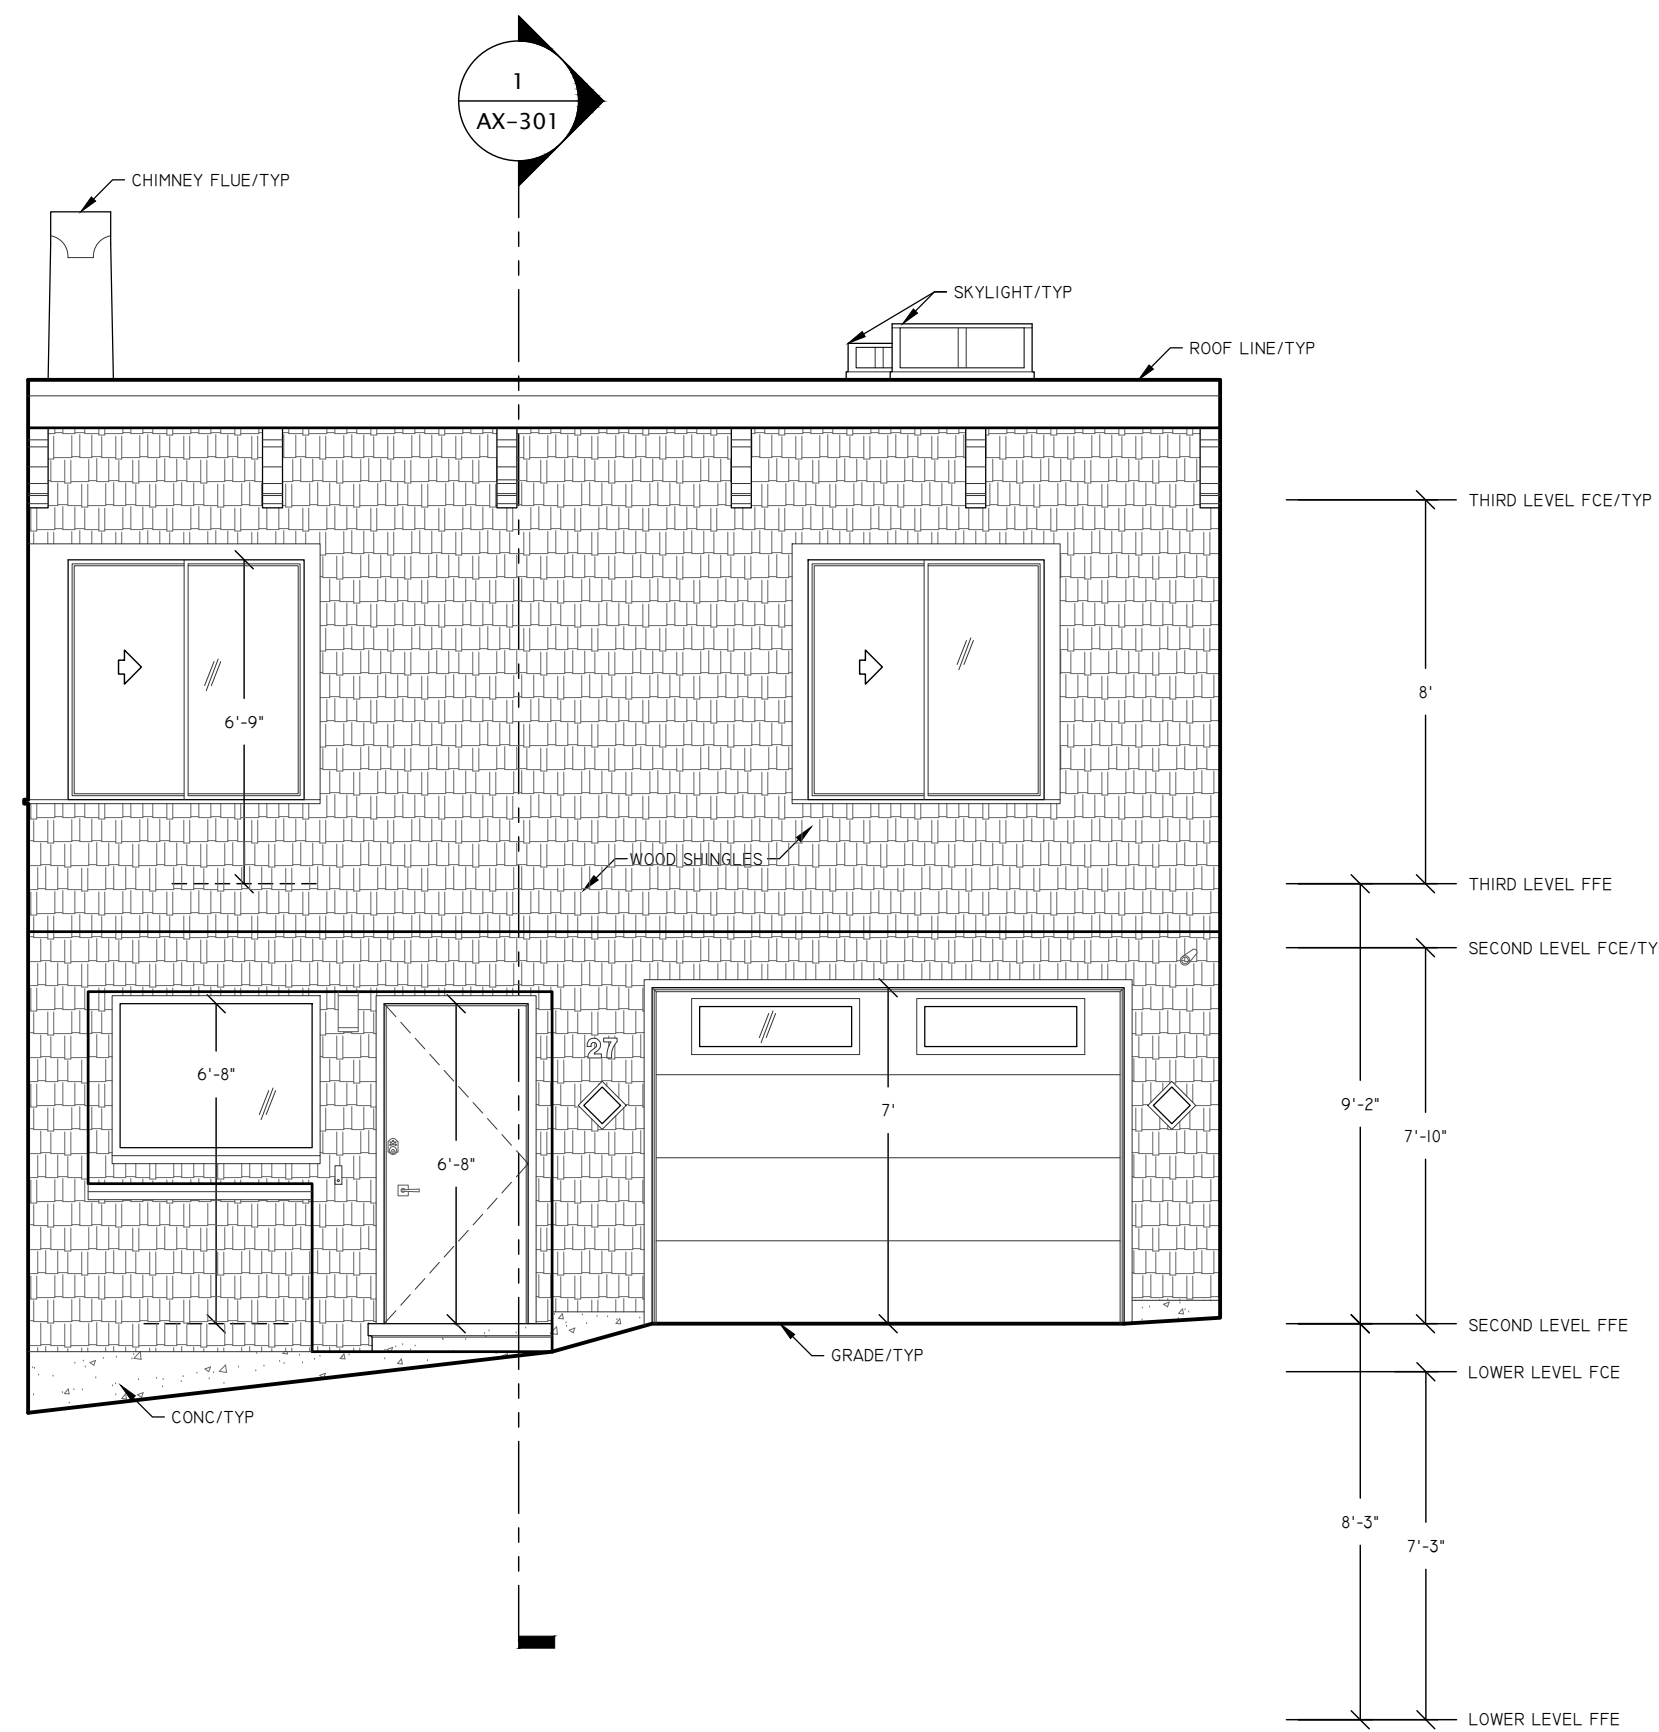

1 EXISTING NORTH ELEVATION

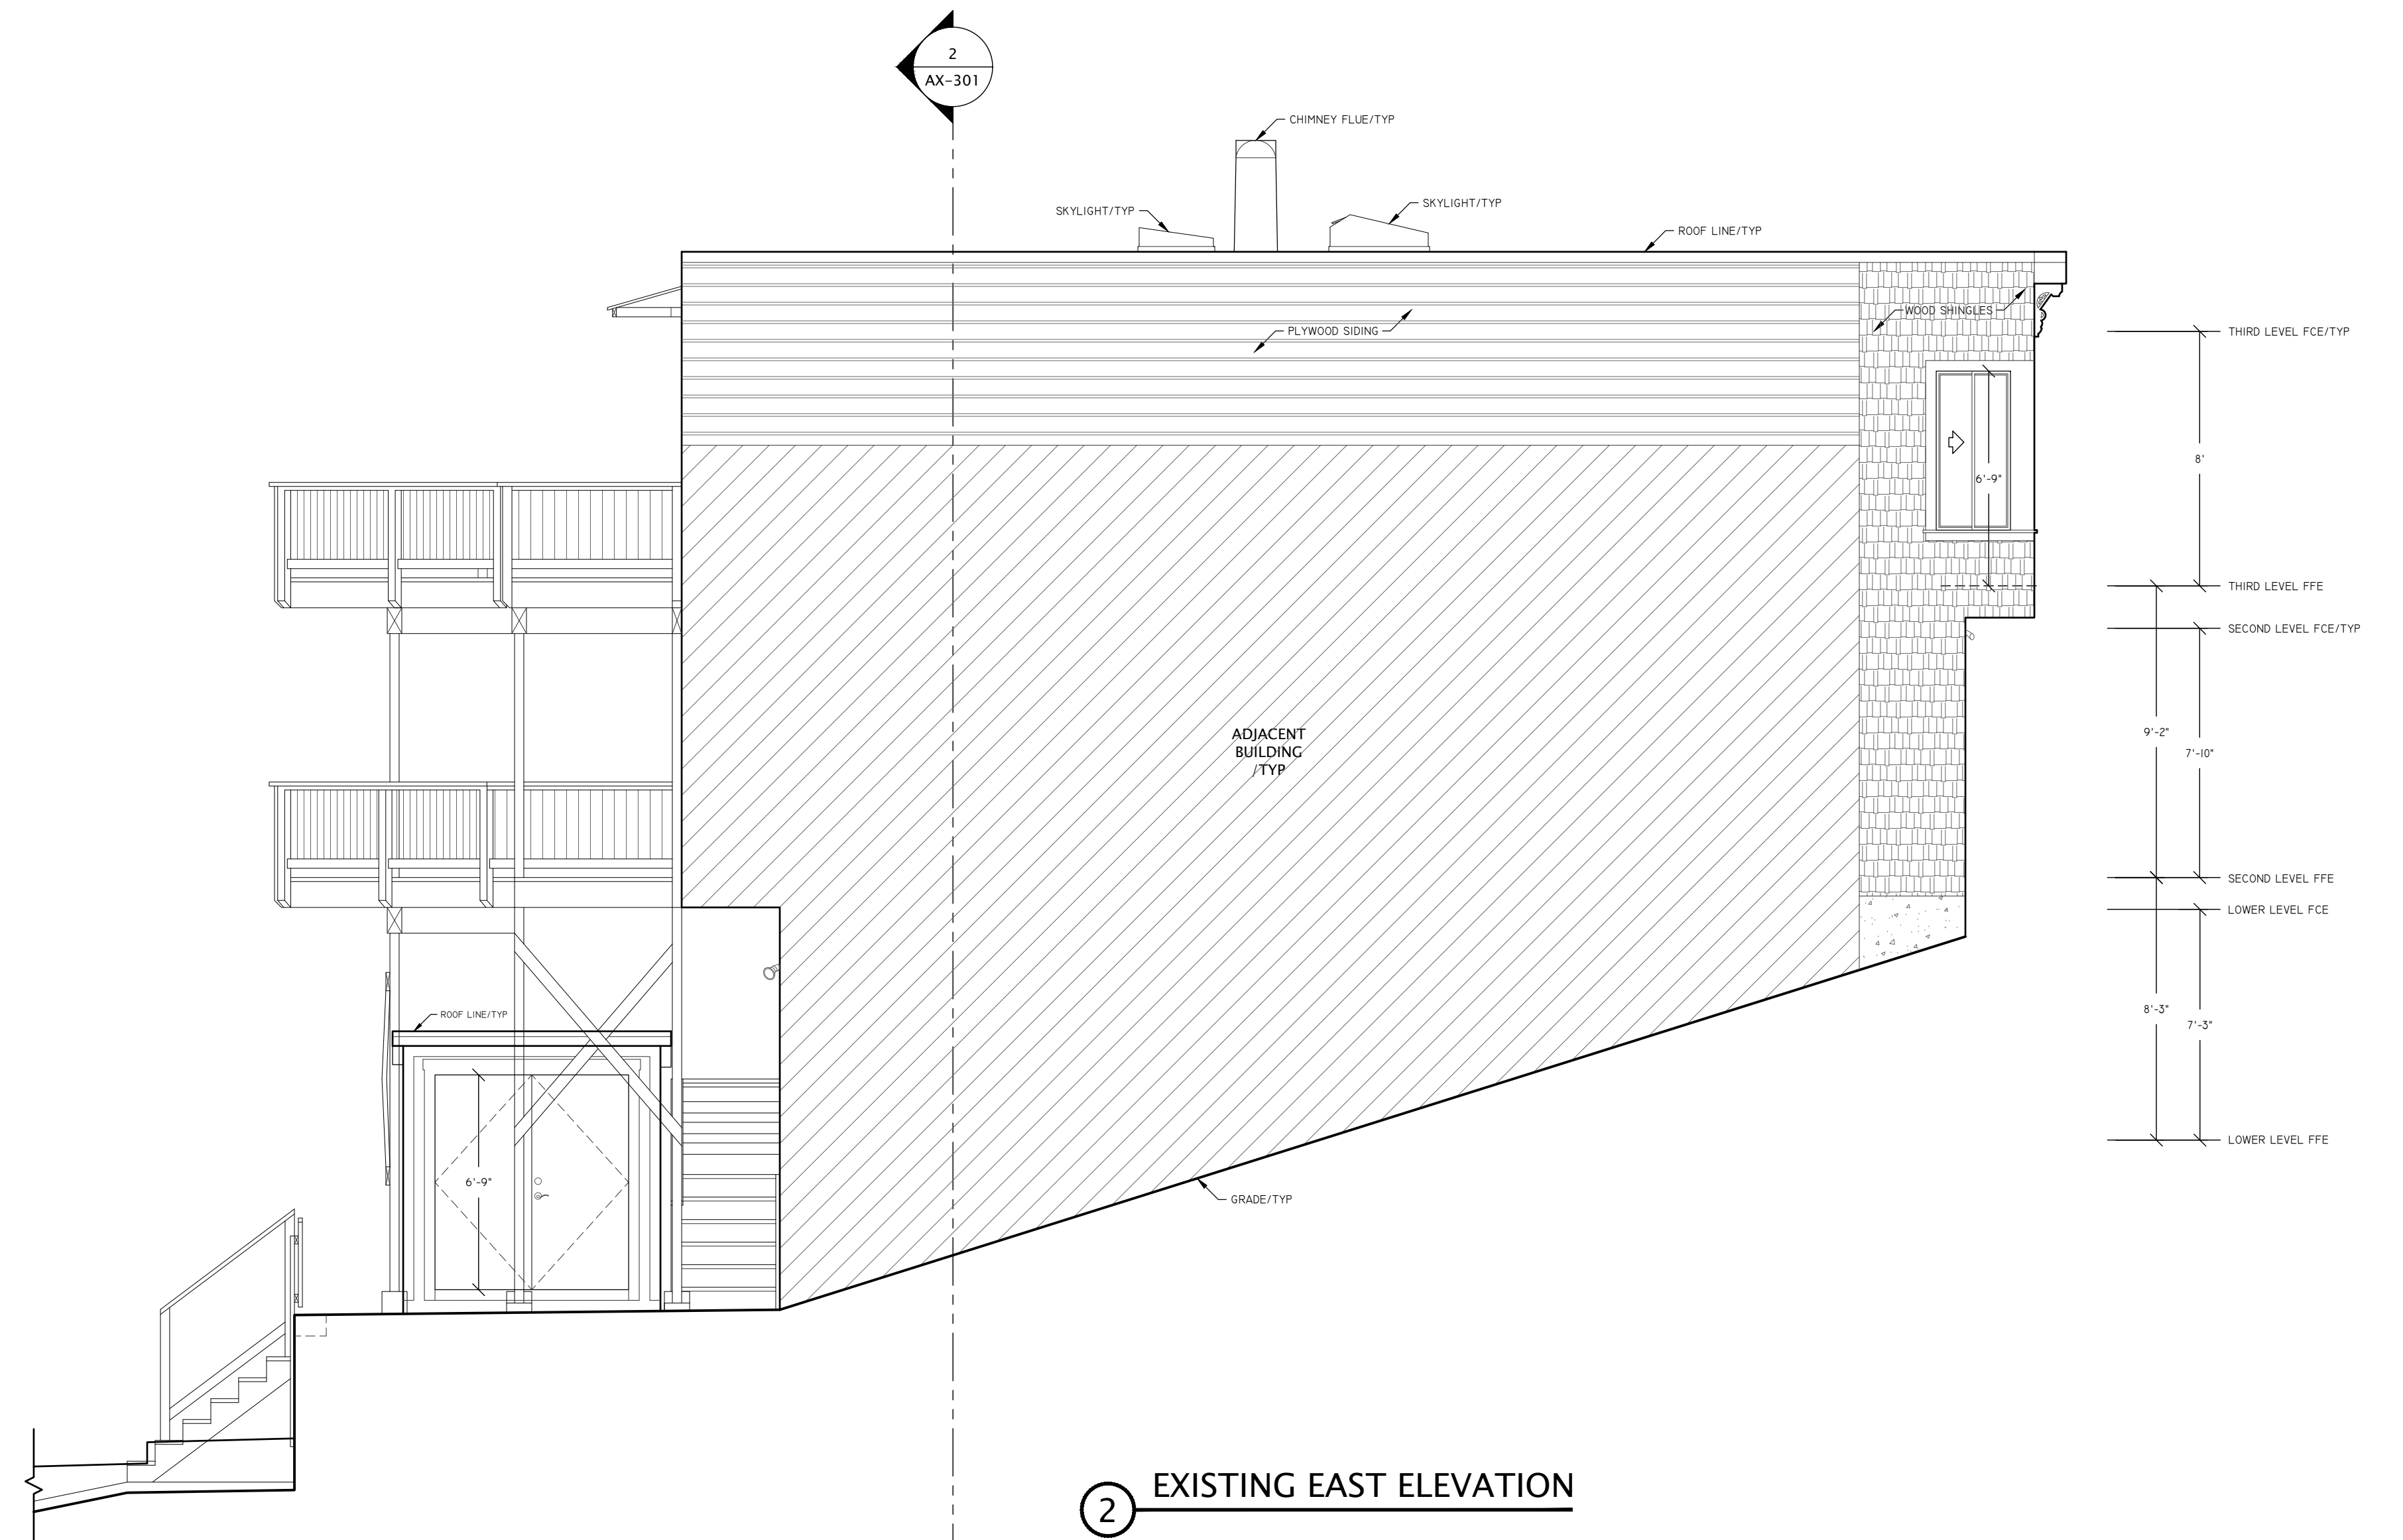

2 EXISTING EAST ELEVATION



27 SATURN STREET
SAN FRANCISCO, CA 94114

THIS DRAWING IS A RECORD OF REAL PROPERTY THAT IS GENERALLY ACCEPTED TO BE SUITABLE FOR USE IN PLANNING, DESIGN, LEASE, AND GENERAL ASSET MANAGEMENT. IT SHOULD NOT BE USED TO DETERMINE EXACT MEASUREMENTS OF SPACES OR ARTIFACTS FOUND HEREIN FOR ANY PURPOSE.
EXTERIOR ELEMENTS HAVE BEEN MEASURED AND DRAFTED FOR REFERENCE ONLY - THIS IS NOT A SURVEY.




EXISTING EXTERIOR ELEVATIONS


REF: 27sf_City_SFD
REV: 0
DRAWN BY: MV
AUDITED BY: JK

SHEET SIZE: 24x36
SCALE: 1/4"=1'-0"
FIELD MEASURE:
10/7/19

AX-201
2 OF 4

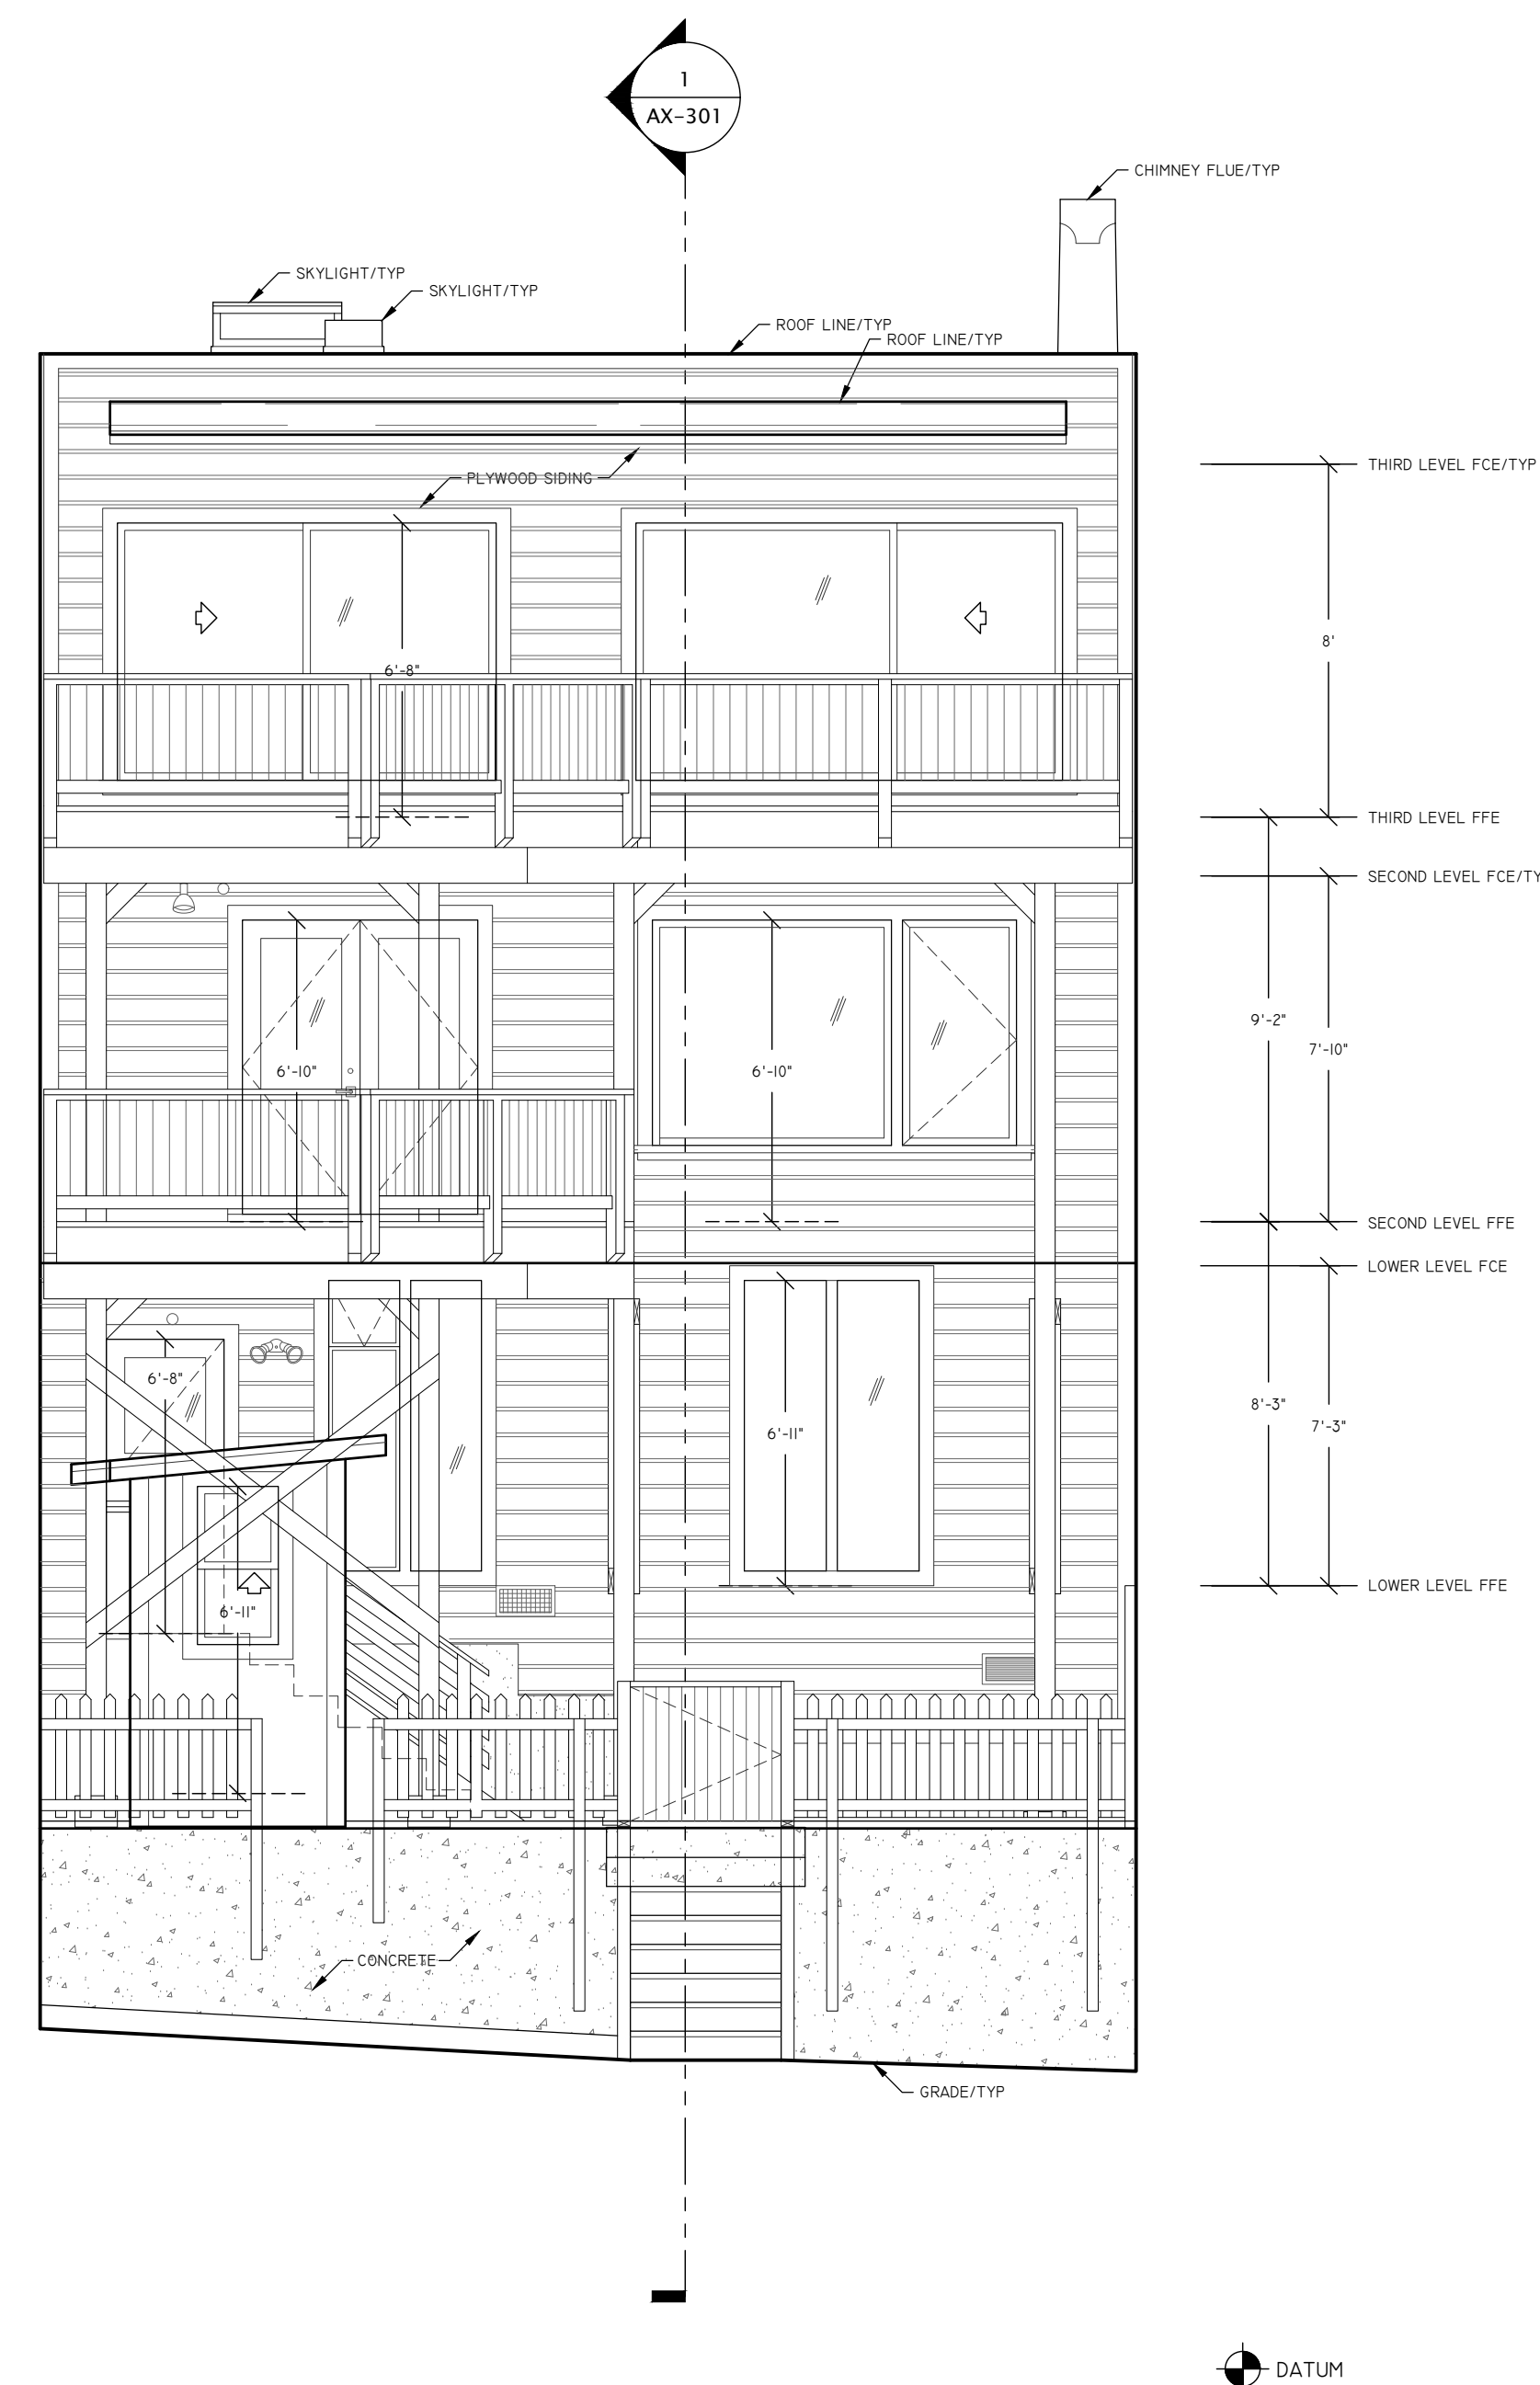

① EXISTING SOUTH ELEVATION

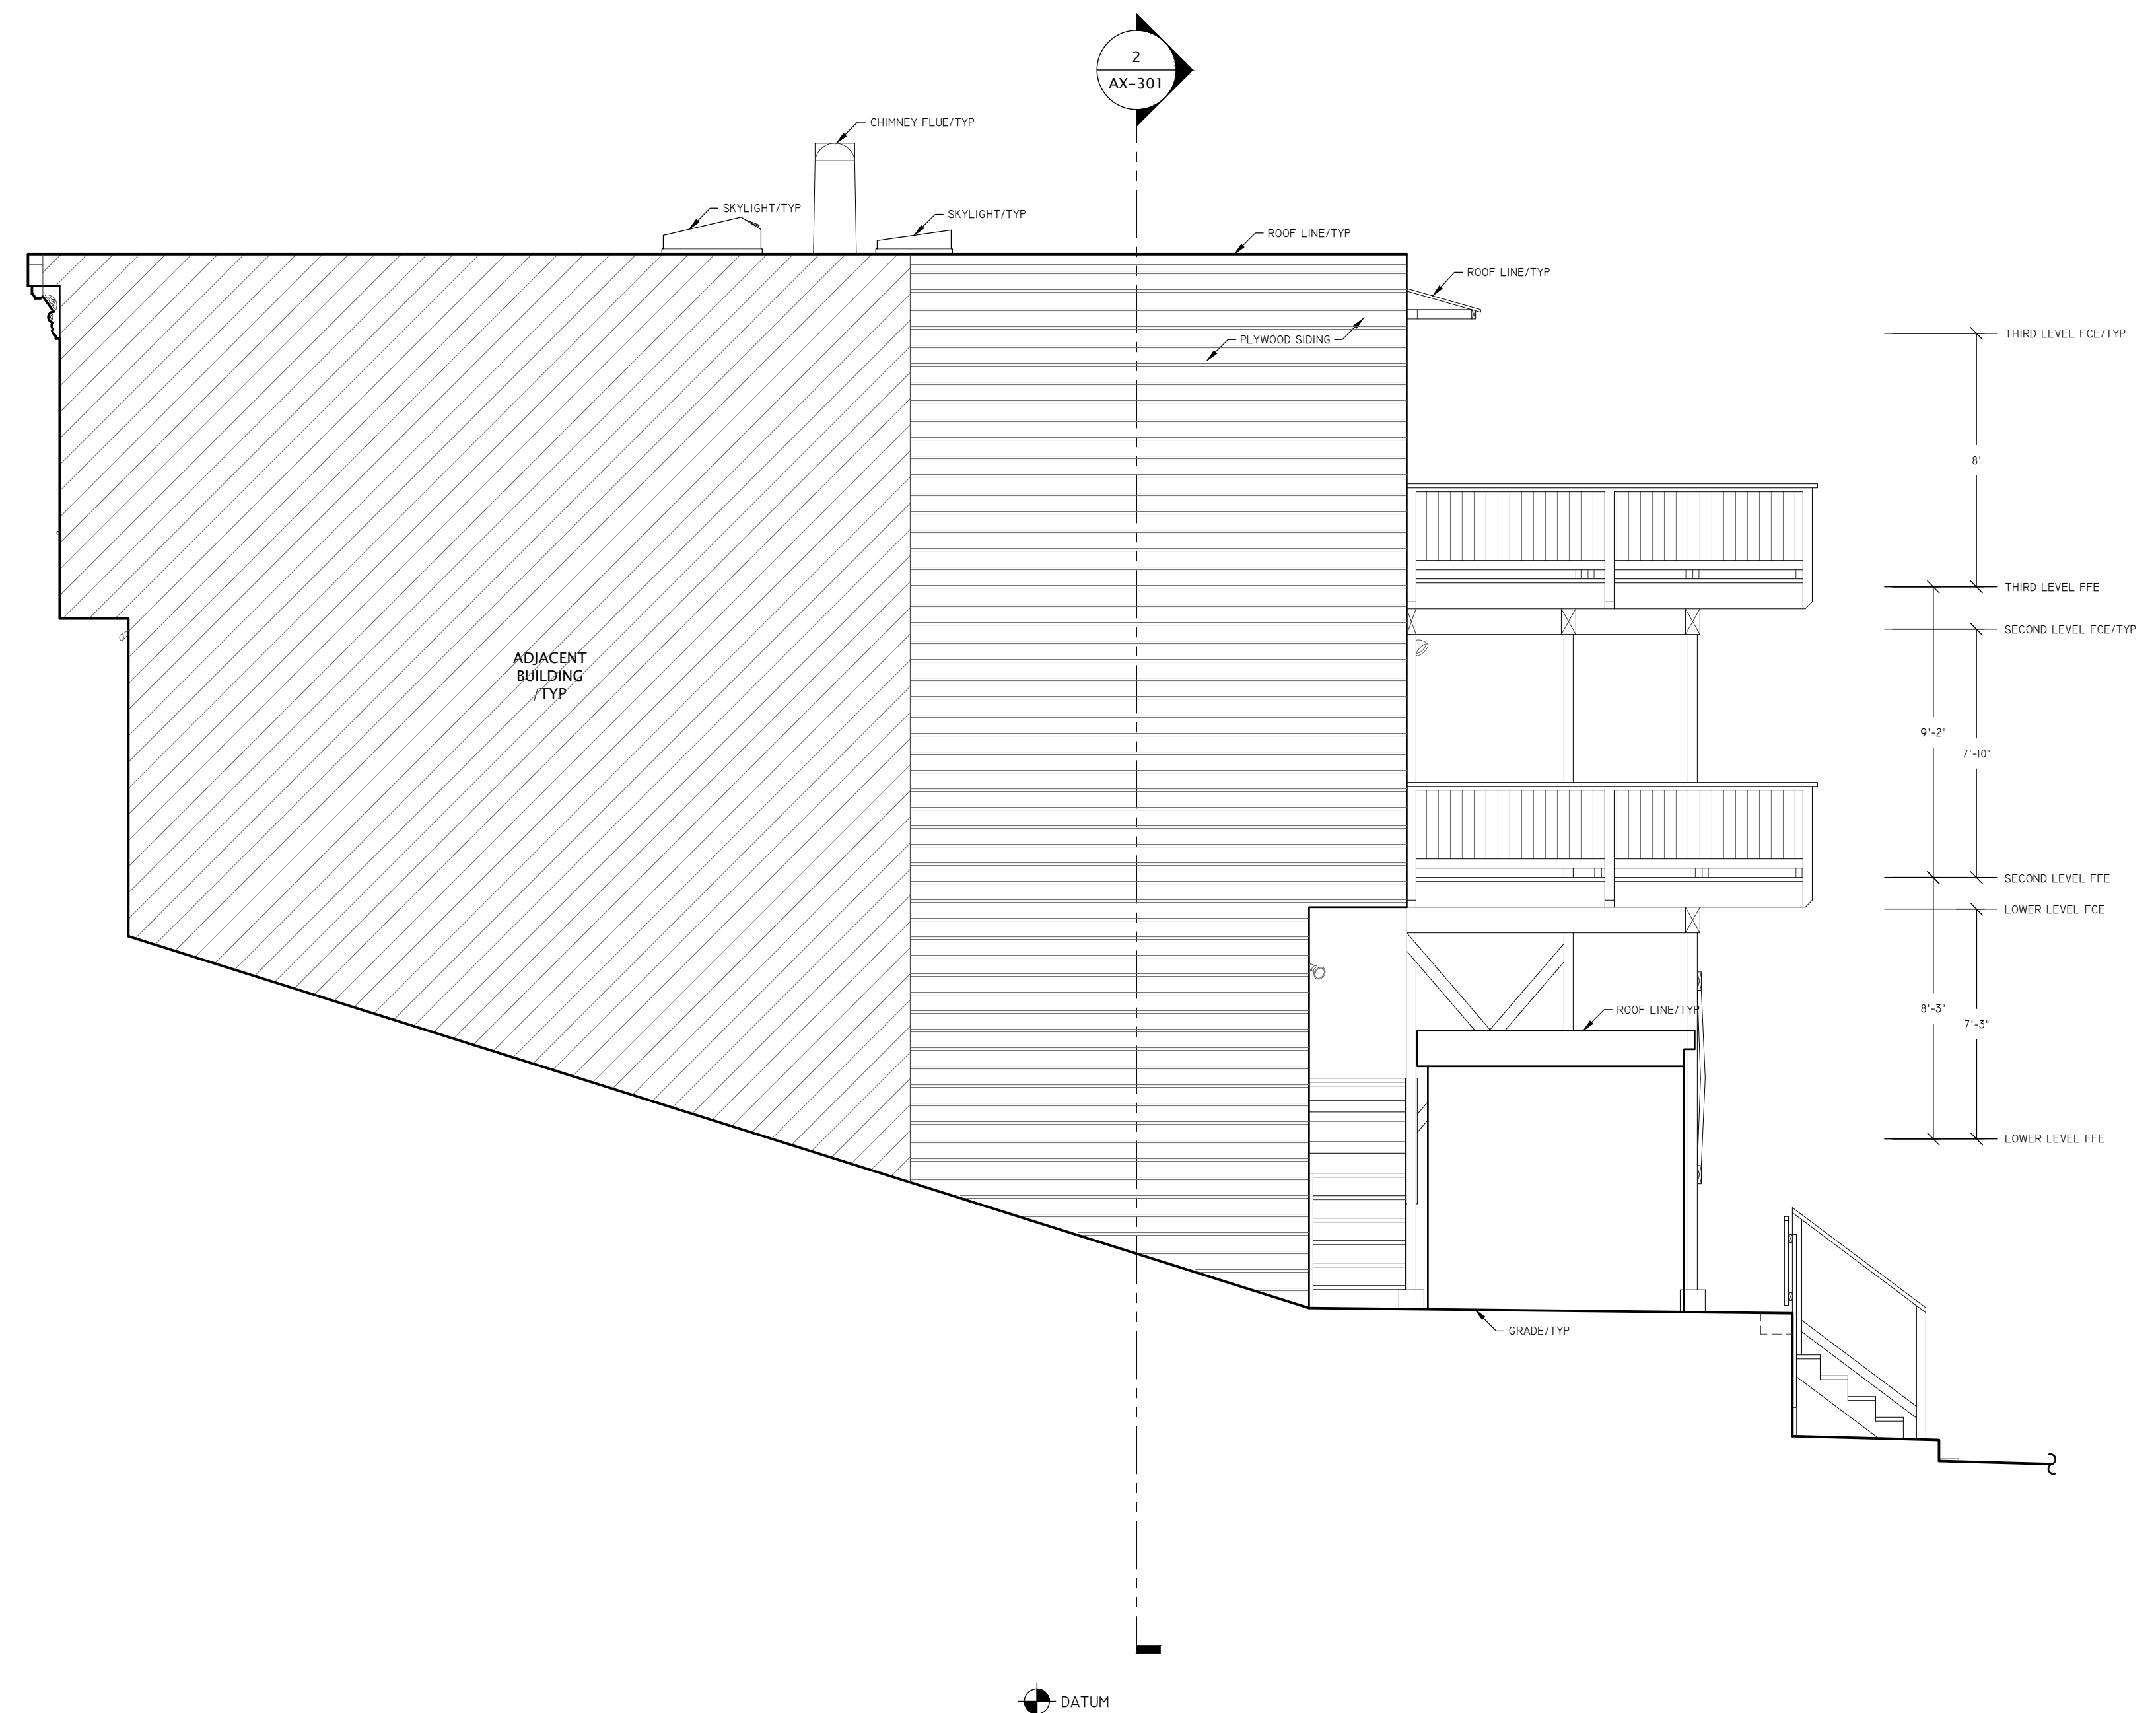

② EXISTING WEST ELEVATION

27 SATURN STREET
SAN FRANCISCO, CA 94114

THIS DRAWING IS A RECORD OF REAL PROPERTY THAT IS GENERALLY ACCEPTED TO BE SUITABLE FOR USE IN PLANNING, DESIGN, LEASE, AND GENERAL ASSET MANAGEMENT. IT SHOULD NOT BE USED TO DETERMINE EXACT MEASUREMENTS OF SPACES OR ARTIFACTS FOUND HEREIN FOR ANY PURPOSE.

EXTERIOR ELEMENTS HAVE BEEN MEASURED AND DRAFTED FOR REFERENCE ONLY - THIS IS NOT A SURVEY.




EXISTING EXTERIOR ELEVATIONS


REF: 27sf_City_SFD
REV: 0
DRAWN BY: MV
AUDITED BY: JK

SHEET SIZE: 24x36
SCALE: 1/4"=1'-0"
FIELD MEASURE:
10/7/19

AX-202
3 OF 4

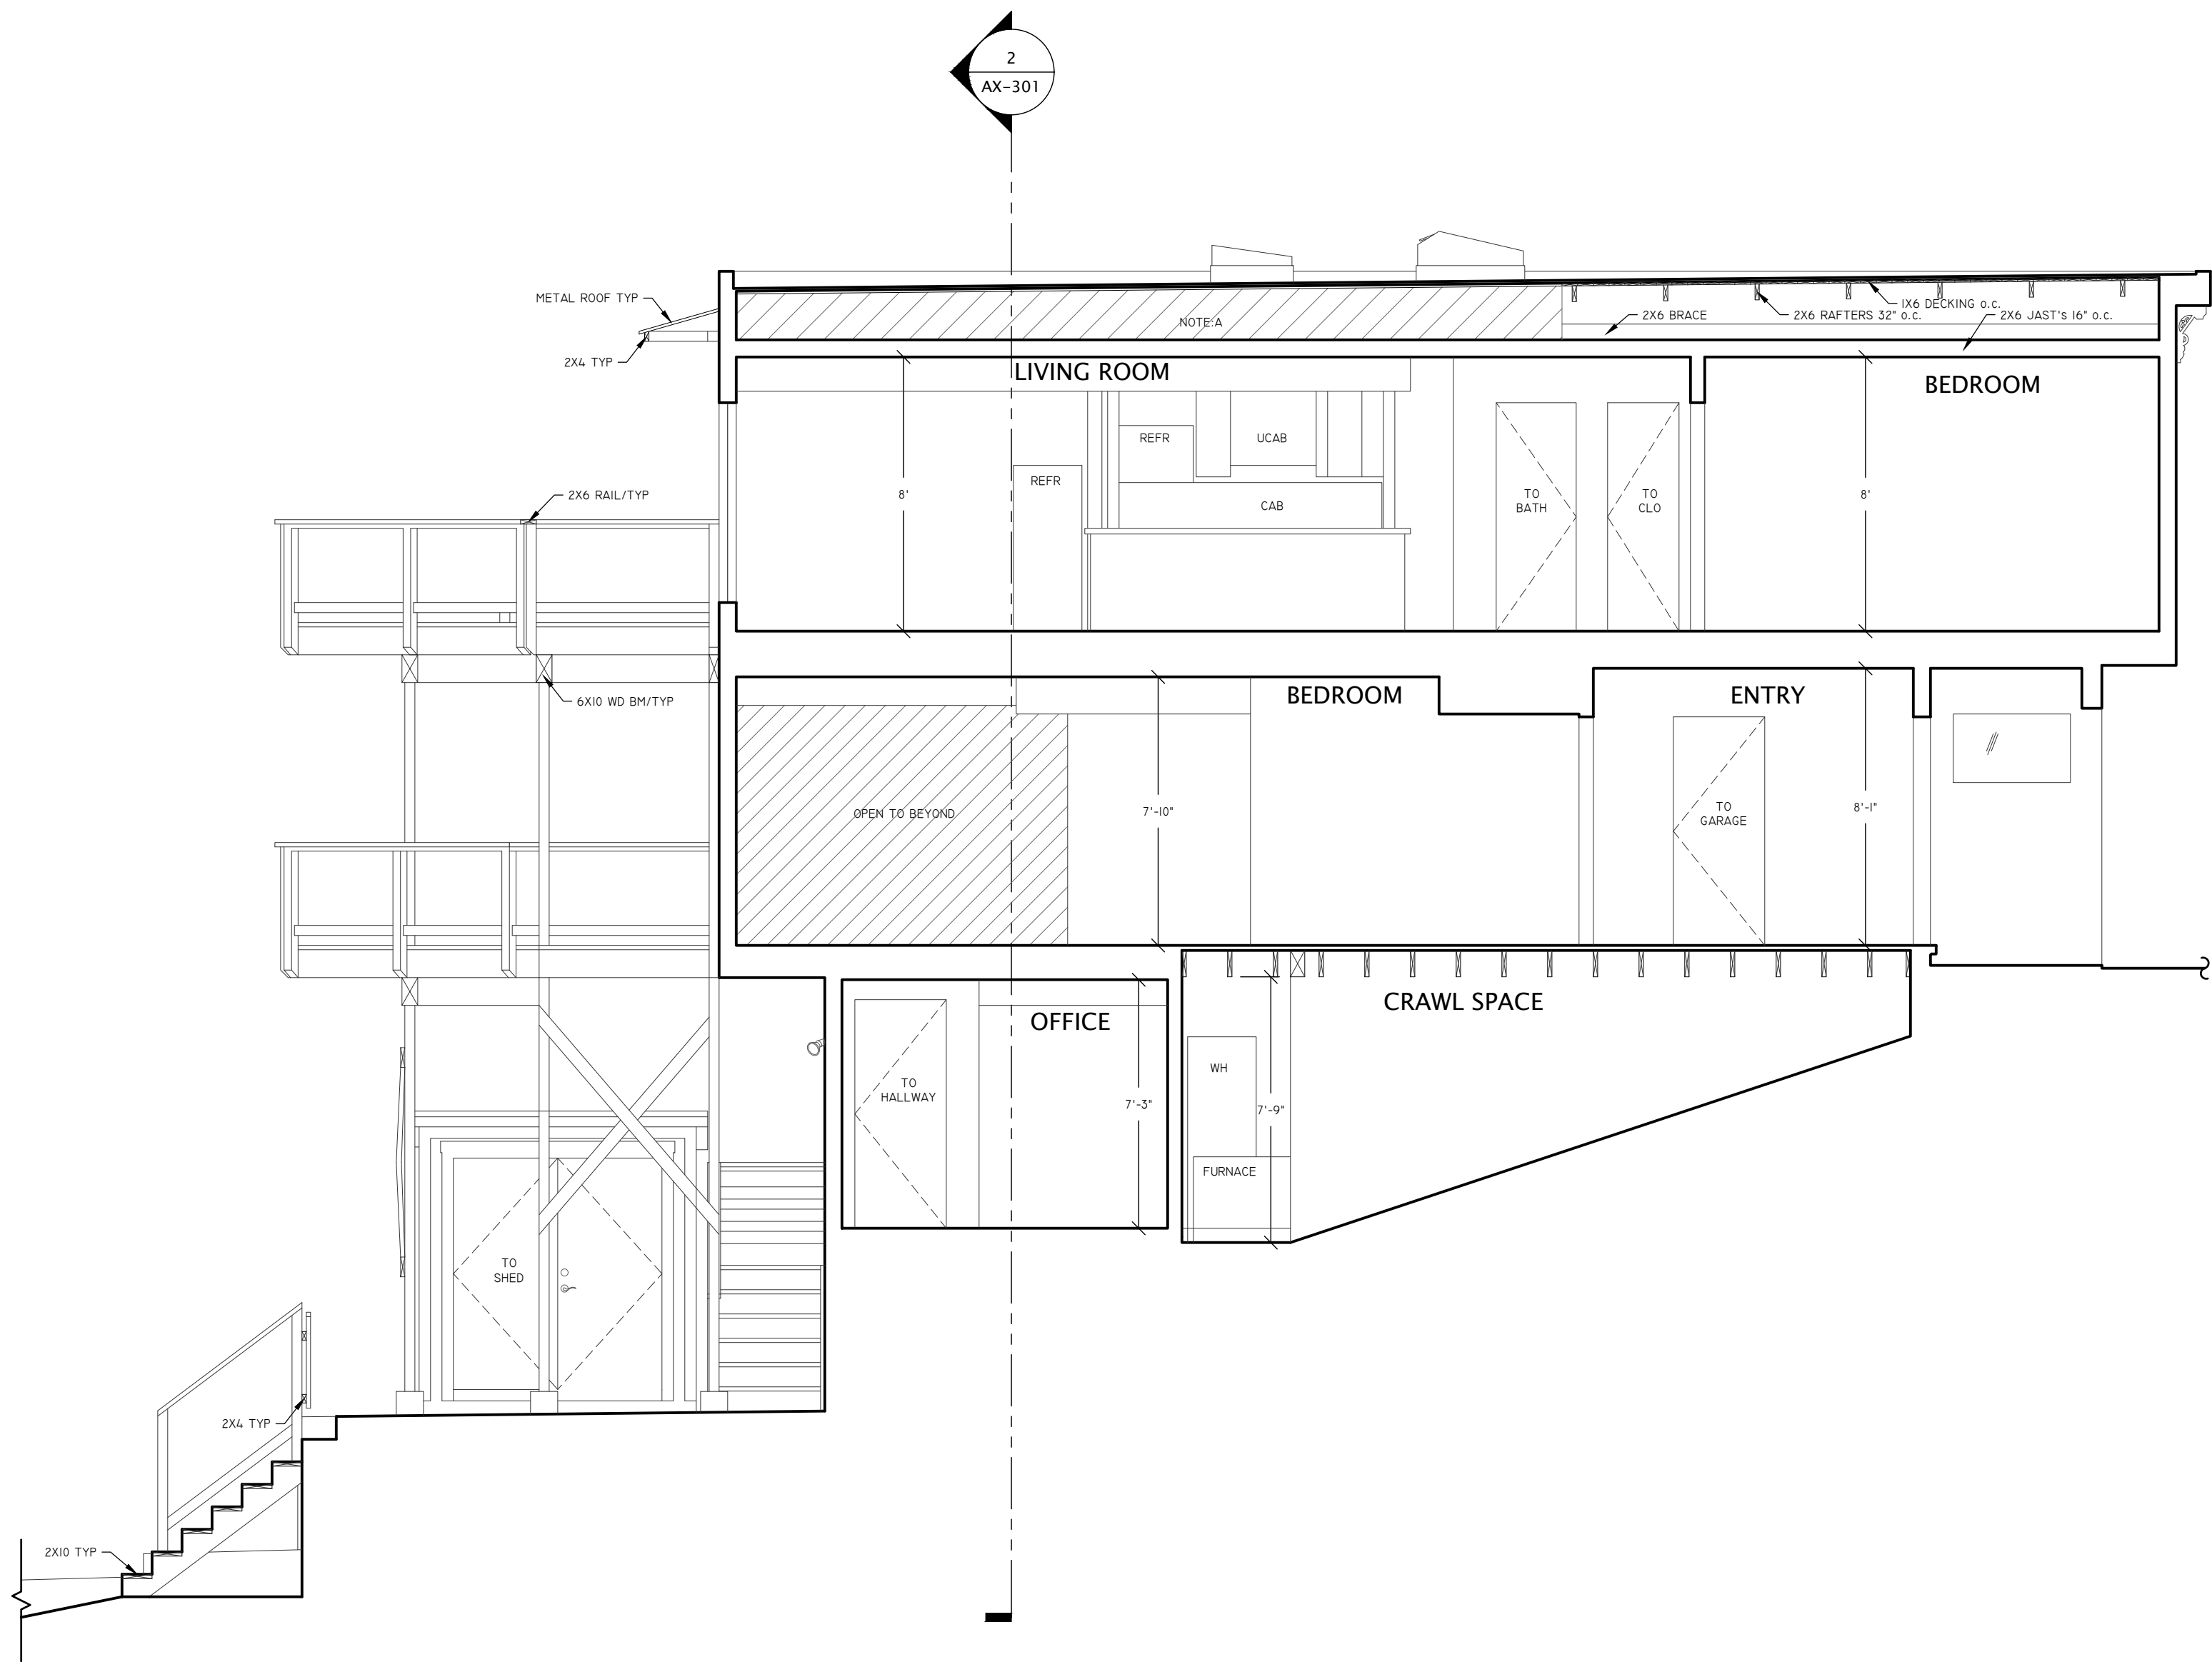

1 EXISTING LONGITUDINAL SECTION

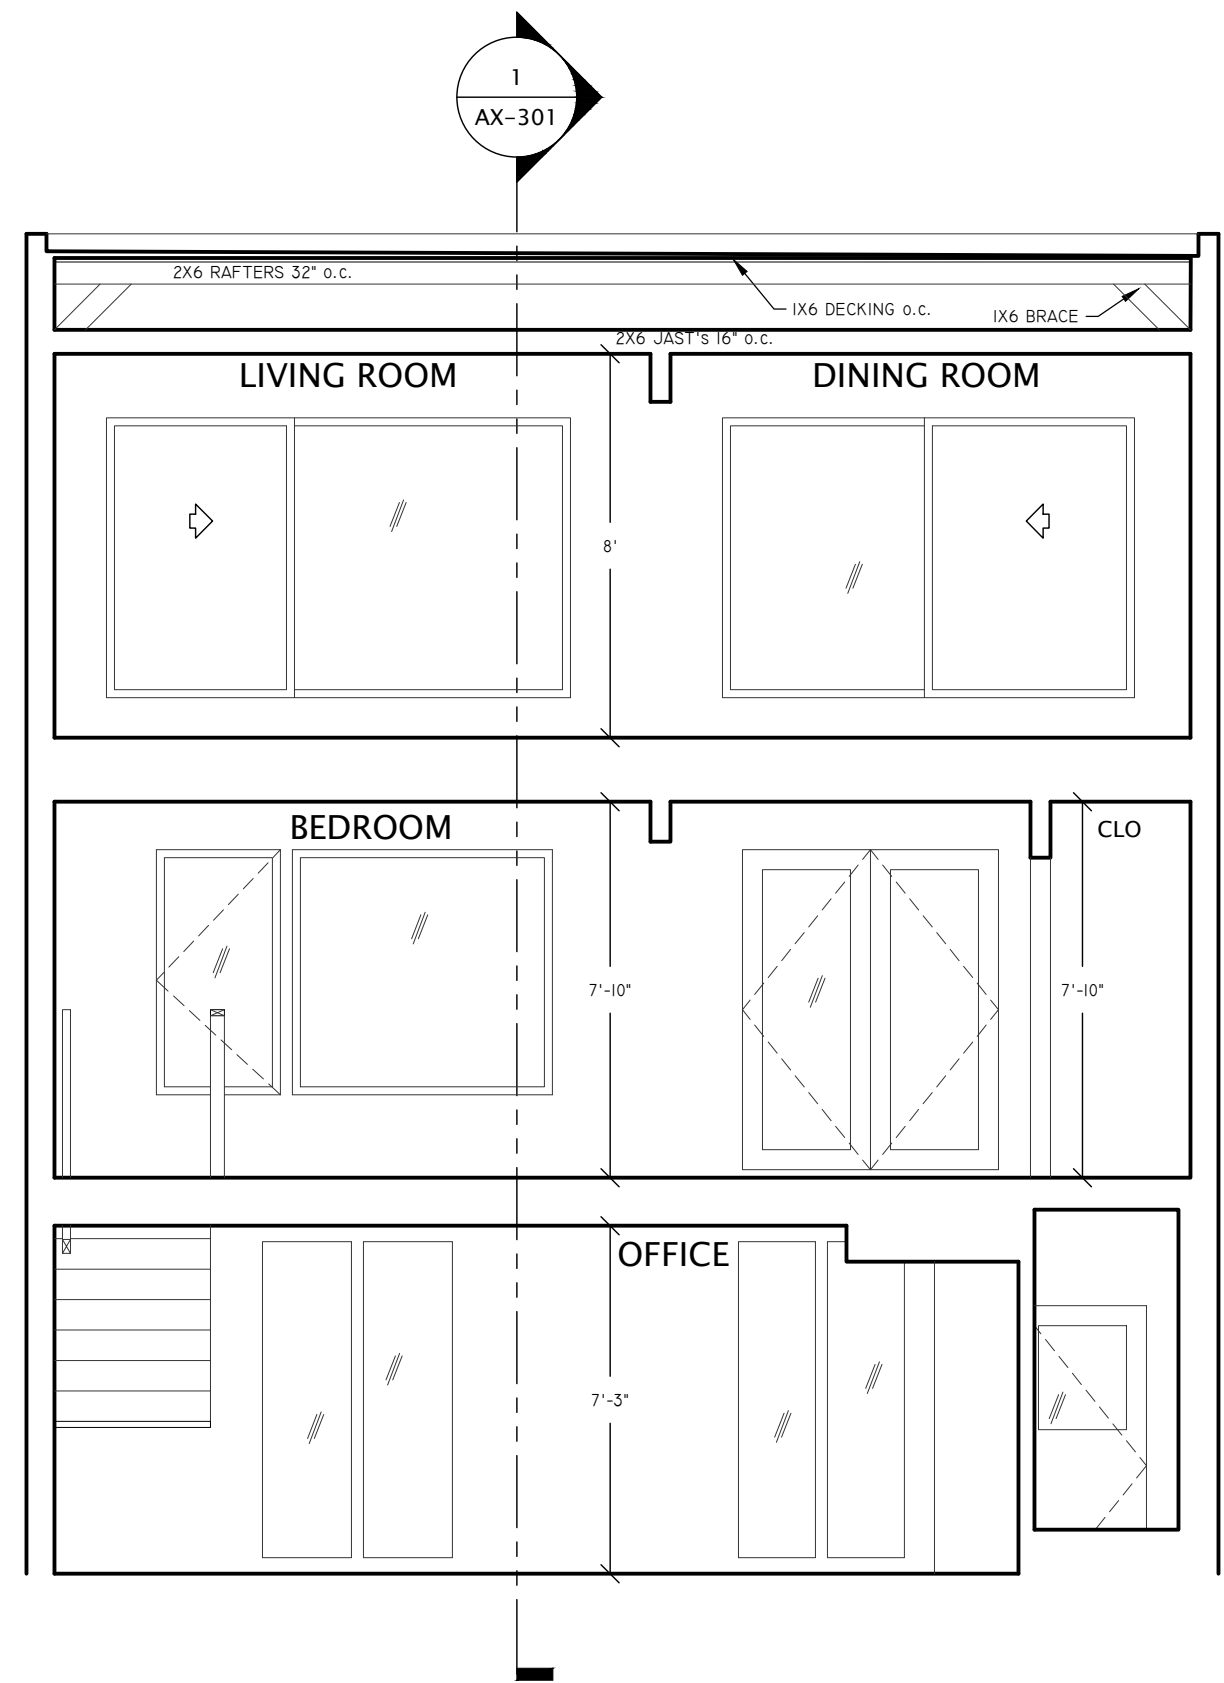

2 EXISTING CROSS SECTION

NOTE A:
THIS AREA NOT ACCESSIBLE AT TIME OF DATA ACQUISITION,
AREA NOT MEASURED.

27 SATURN STREET SAN FRANCISCO, CA 94114		
THIS DRAWING IS A RECORD OF REAL PROPERTY THAT IS GENERALLY ACCEPTED TO BE SUITABLE FOR USE IN PLANNING, DESIGN, LEASE, AND GENERAL ASSET MANAGEMENT. IT SHOULD NOT BE USED TO DETERMINE EXACT MEASUREMENTS OF SPACES OR ARTIFACTS FOUND HEREIN FOR ANY PURPOSE.		
 RED BRIDGE DESIGN SAN FRANCISCO REDBRIDGEDESIGN.COM		
EXISTING BUILDING SECTIONS		
REF: 27sf_City_SFD REV: 0 DRAWN BY: MV AUDITED BY: JK	SHEET SIZE: 24x36 SCALE: 1/4"=1'-0" FIELD MEASURE: 10/7/19	AX-301 4 OF 4