



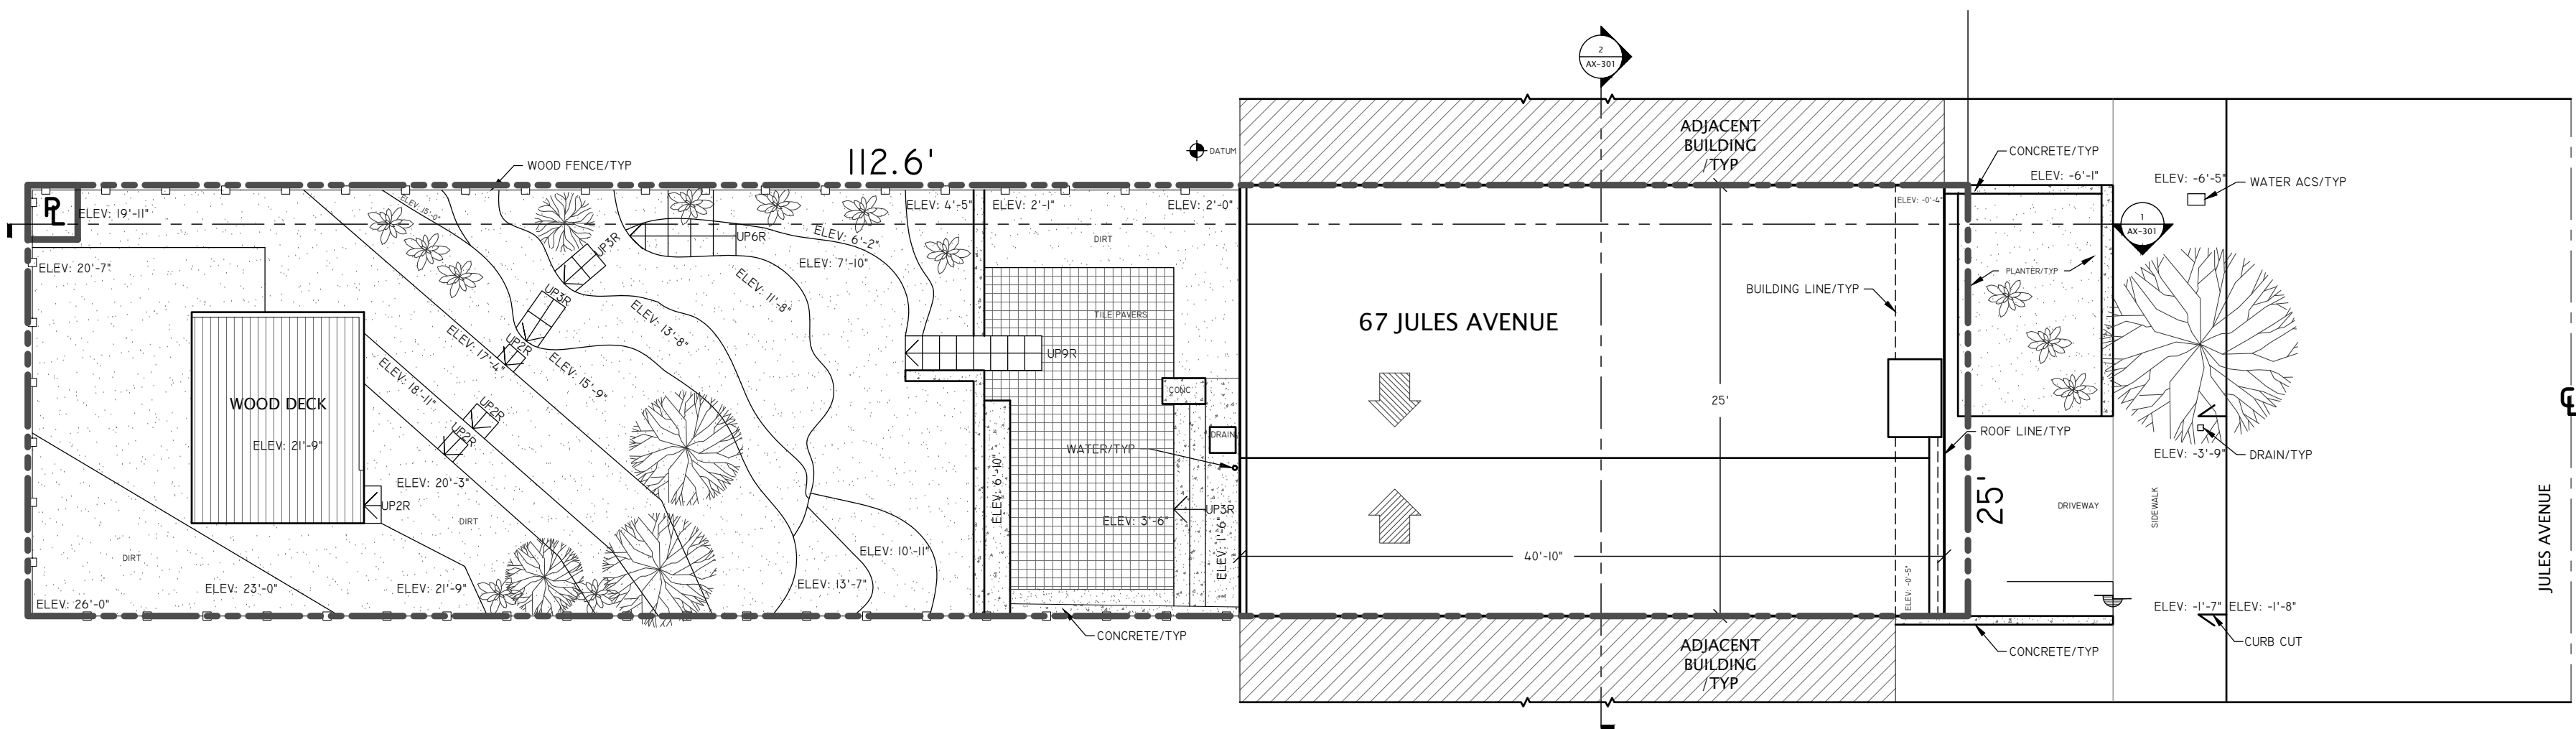

1 EXISTING LANDSCAPE SURVEY
2,815 SQFT (0.065 ACRE) SITE PLAN

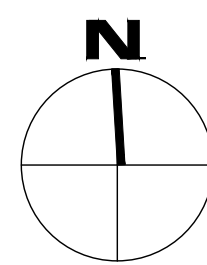

1.) THIS IS NOT A LAND SURVEY, PROPERTY LINES ARE NOT DETERMINED.
2.) PROPERTY LINES ARE COPIED FROM TAX ASSESSOR'S MAP. PLACEMENT ASSUMED.

67 CAYUGA STREET
SAN FRANCISCO, CA 94108

THIS DRAWING IS A RECORD OF REAL PROPERTY THAT IS GENERALLY ACCEPTED TO BE SUITABLE FOR USE IN PLANNING, DESIGN, LEASE, AND GENERAL ASSET MANAGEMENT. IT SHOULD NOT BE USED TO DETERMINE EXACT MEASUREMENTS OF SPACES OR ARTIFACTS FOUND HEREIN FOR ANY PURPOSE.
EXTERIOR ELEMENTS HAVE BEEN MEASURED AND DRAFTED FOR REFERENCE ONLY - THIS IS NOT A SURVEY.




EXISTING LANDSCAPE SURVEY


REF: 67sf_City_SFD
REV: 0
DRAWN BY: MV
AUDITED BY: JK

SHEET SIZE: 24x36
SCALE: 1/8"=1'-0"
FIELD MEASURE:
5/1/19

AX-101
1 OF 7

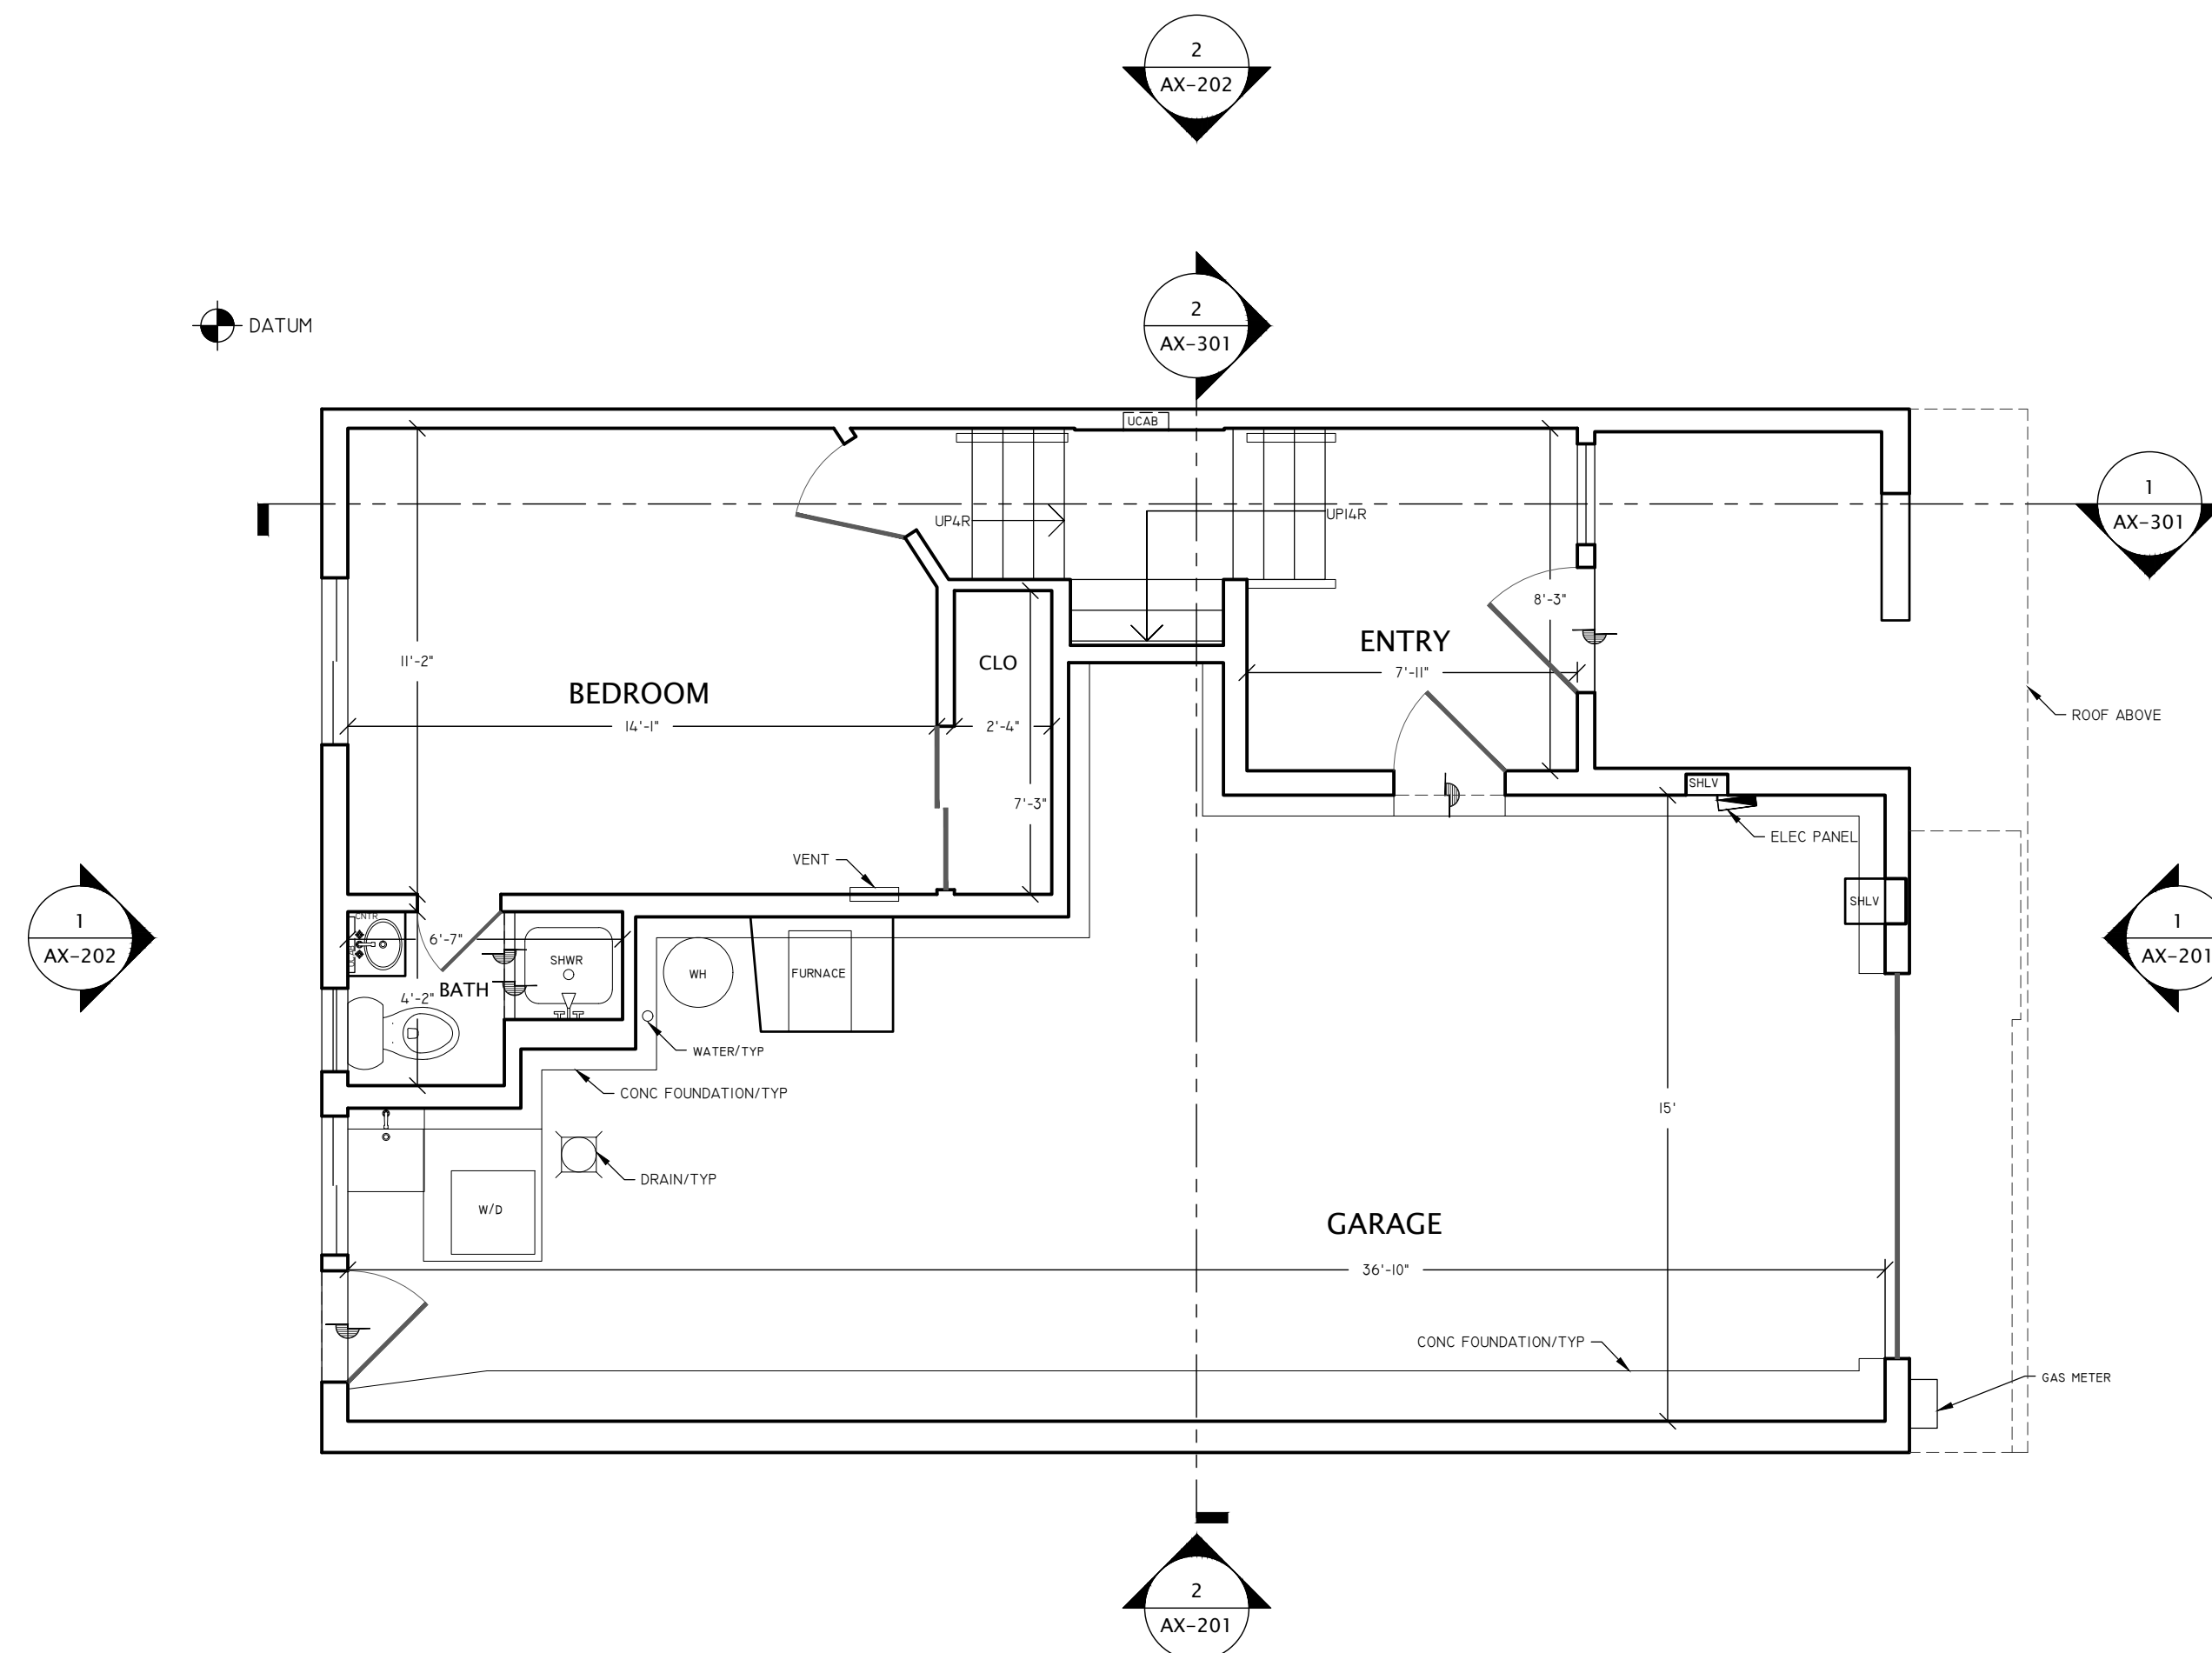

1 EXISTING ENTRY LEVEL FLOOR PLAN
891 SQFT GROSS MEASURED AREA
60 SQFT MEASURED EXTERIOR SURFACES

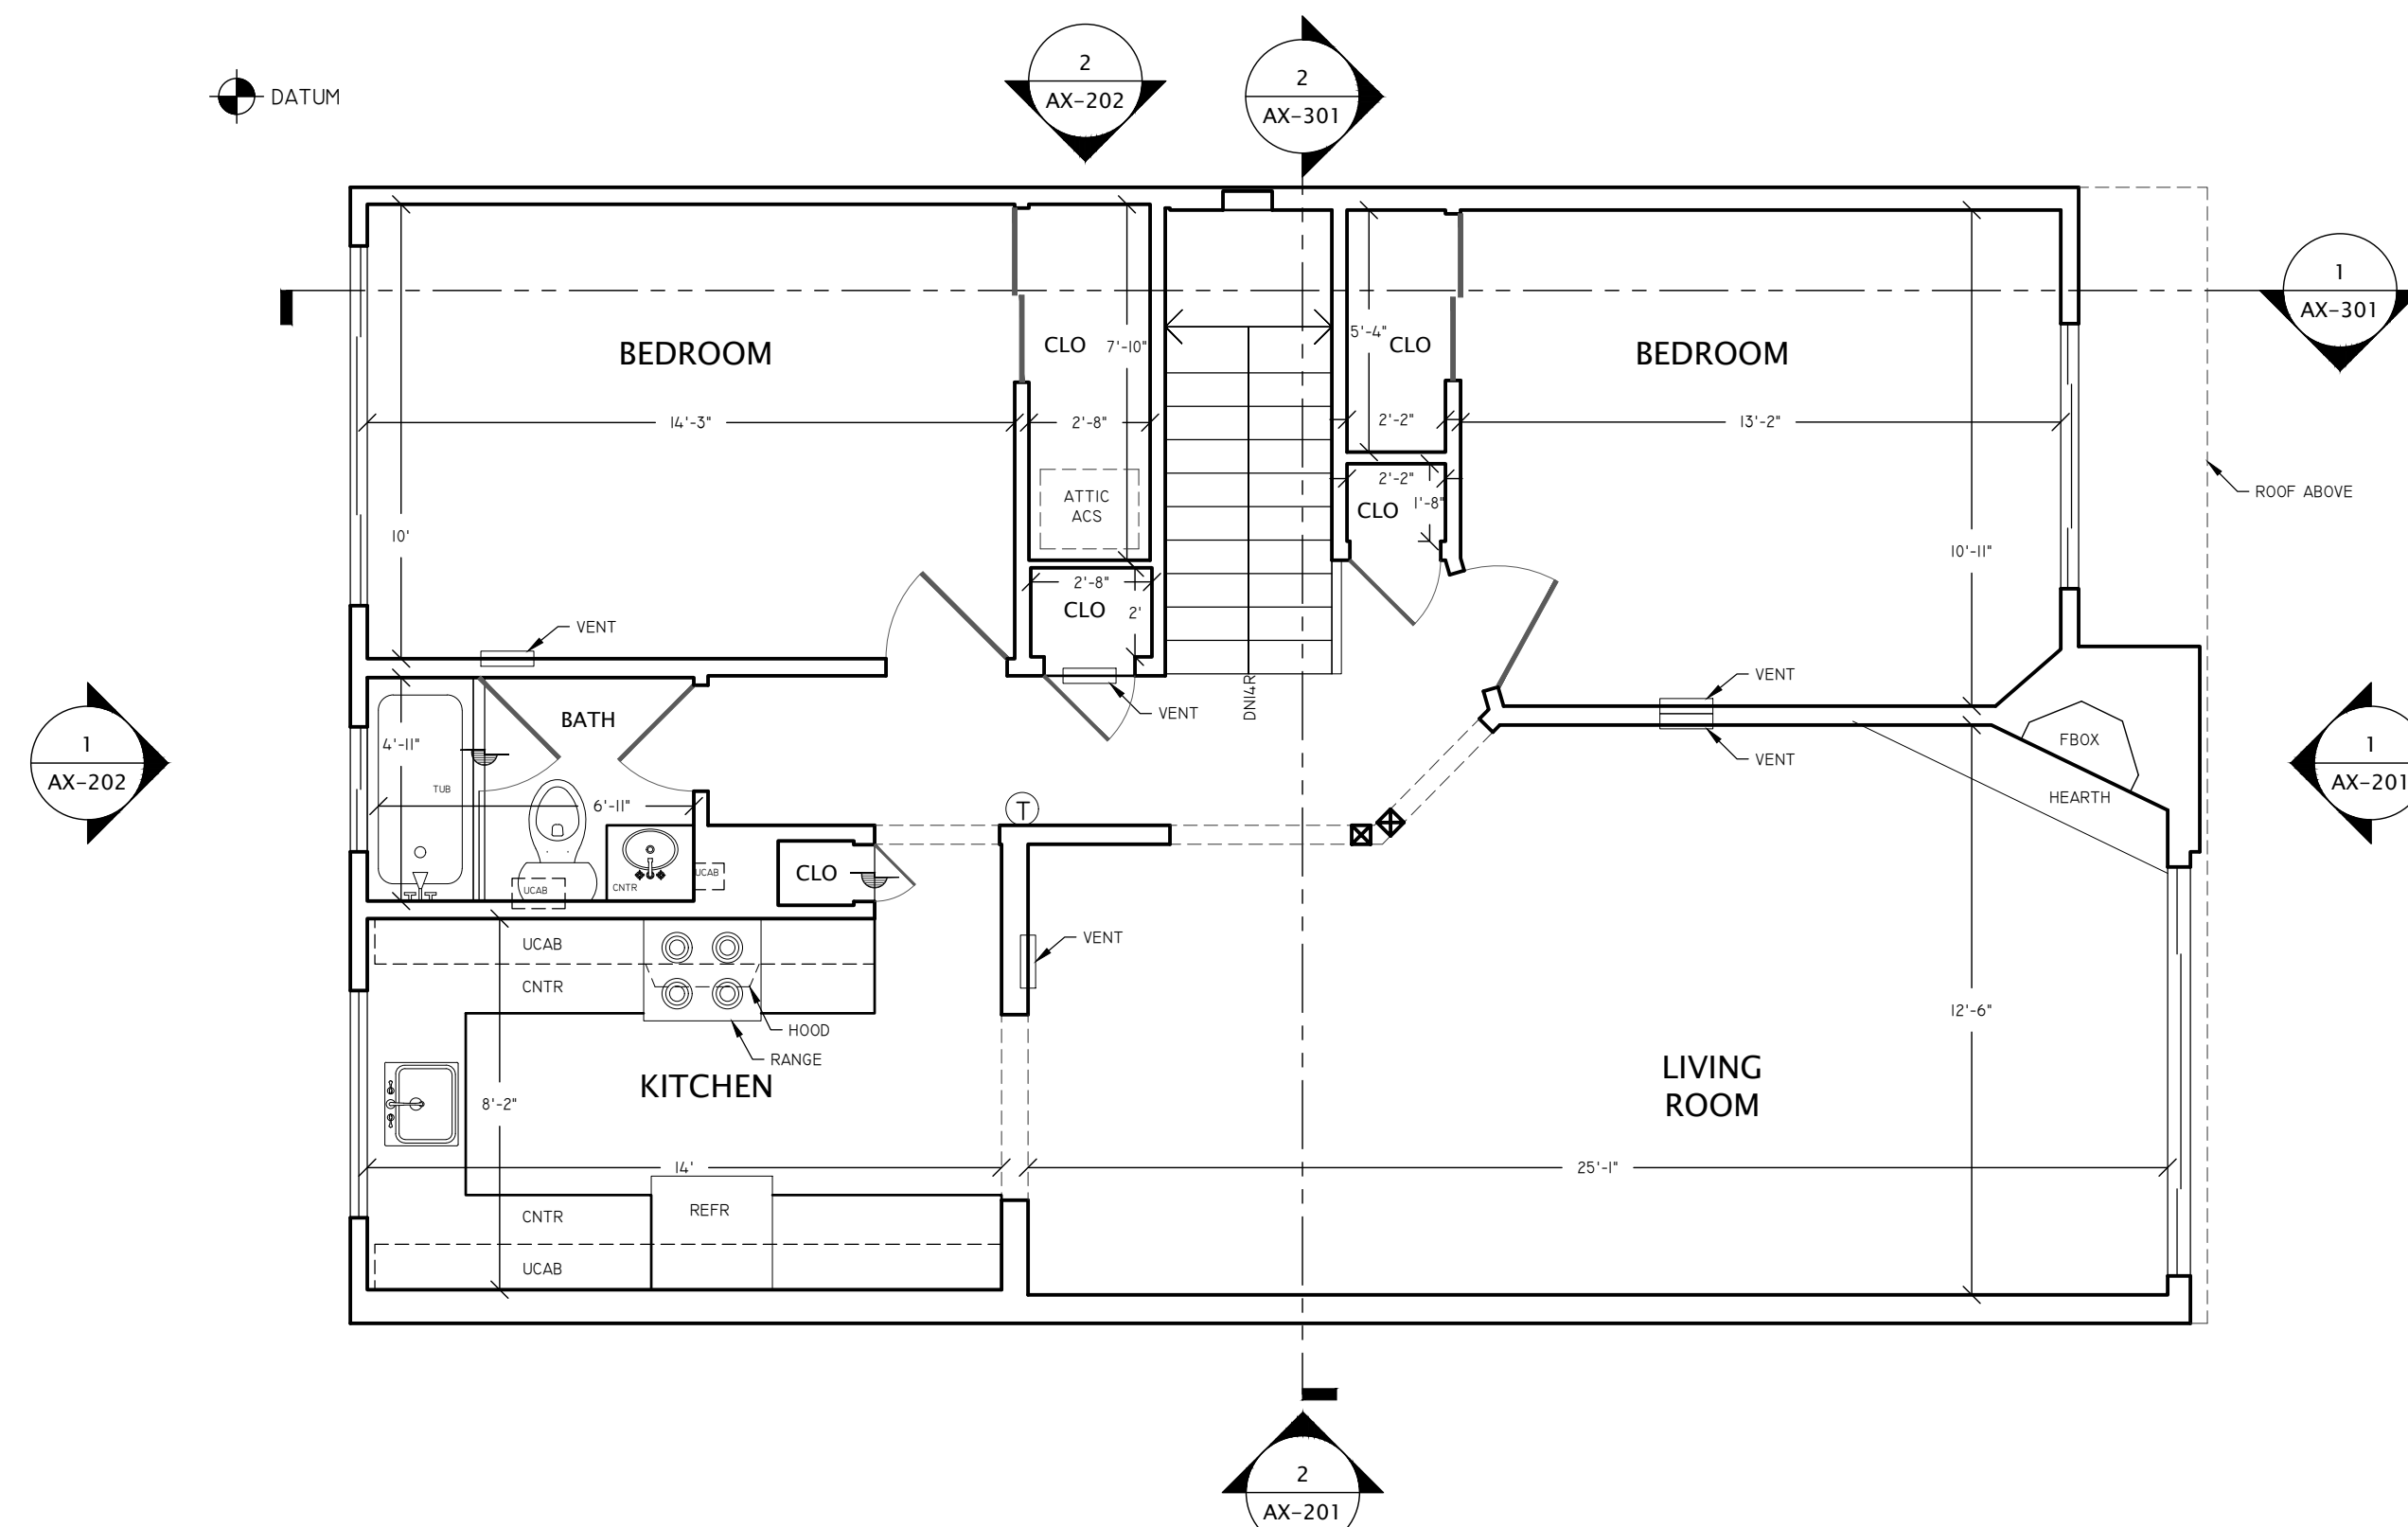



2 EXISTING SECOND LEVEL FLOOR PLAN
989 SQFT GROSS MEASURED AREA

LEGEND	
①	THERMOSTAT


67 CAYUGA STREET SAN FRANCISCO, CA 94108		
THIS DRAWING IS A RECORD OF REAL PROPERTY THAT IS GENERALLY ACCEPTED TO BE SUITABLE FOR USE IN PLANNING, DESIGN, LEASE, AND GENERAL ASSET MANAGEMENT. IT SHOULD NOT BE USED TO DETERMINE EXACT MEASUREMENTS OF SPACES OR ARTIFACTS FOUND HEREIN FOR ANY PURPOSE. EXTERIOR ELEMENTS HAVE BEEN MEASURED AND DRAFTED FOR REFERENCE ONLY - THIS IS NOT A SURVEY.		 RED BRIDGE DESIGN SAN FRANCISCO REDBRIDGEDESIGN.COM
EXISTING FLOOR PLAN		
REF: 67sf_City_SFD REV: 0 DRAWN BY: MV AUDITED BY: JK	SHEET SIZE: 24x36 SCALE: 1/4"=1'-0" FIELD MEASURE: 5/1/19	AX-102 2 OF 7

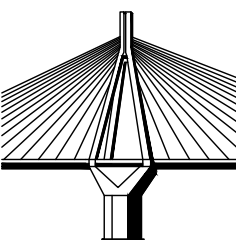

67 CAYUGA STREET SAN FRANCISCO, CA 94108		
THIS DRAWING IS A RECORD OF REAL PROPERTY THAT IS GENERALLY ACCEPTED TO BE SUITABLE FOR USE IN PLANNING, DESIGN, LEASE, AND GENERAL ASSET MANAGEMENT. IT SHOULD NOT BE USED TO DETERMINE EXACT MEASUREMENTS OF SPACES OR ARTIFACTS FOUND HEREIN FOR ANY PURPOSE. EXTERIOR ELEMENTS HAVE BEEN MEASURED AND DRAFTED FOR REFERENCE ONLY – THIS IS NOT A SURVEY.	 RED BRIDGE DESIGN SAN FRANCISCO REDBRIDGEDSIGN.COM	
EXISTING REFLECTED CEILING PLAN		
REV: 67sf_City_SF.D REV. 0 DRAWN BY: MV AUDITED BY: JK	SHEET SIZE: 24x36 SCALE: 1/4"=1'-0" FIELD MEASURE: 5/1/19	AX-103 3 OF 7

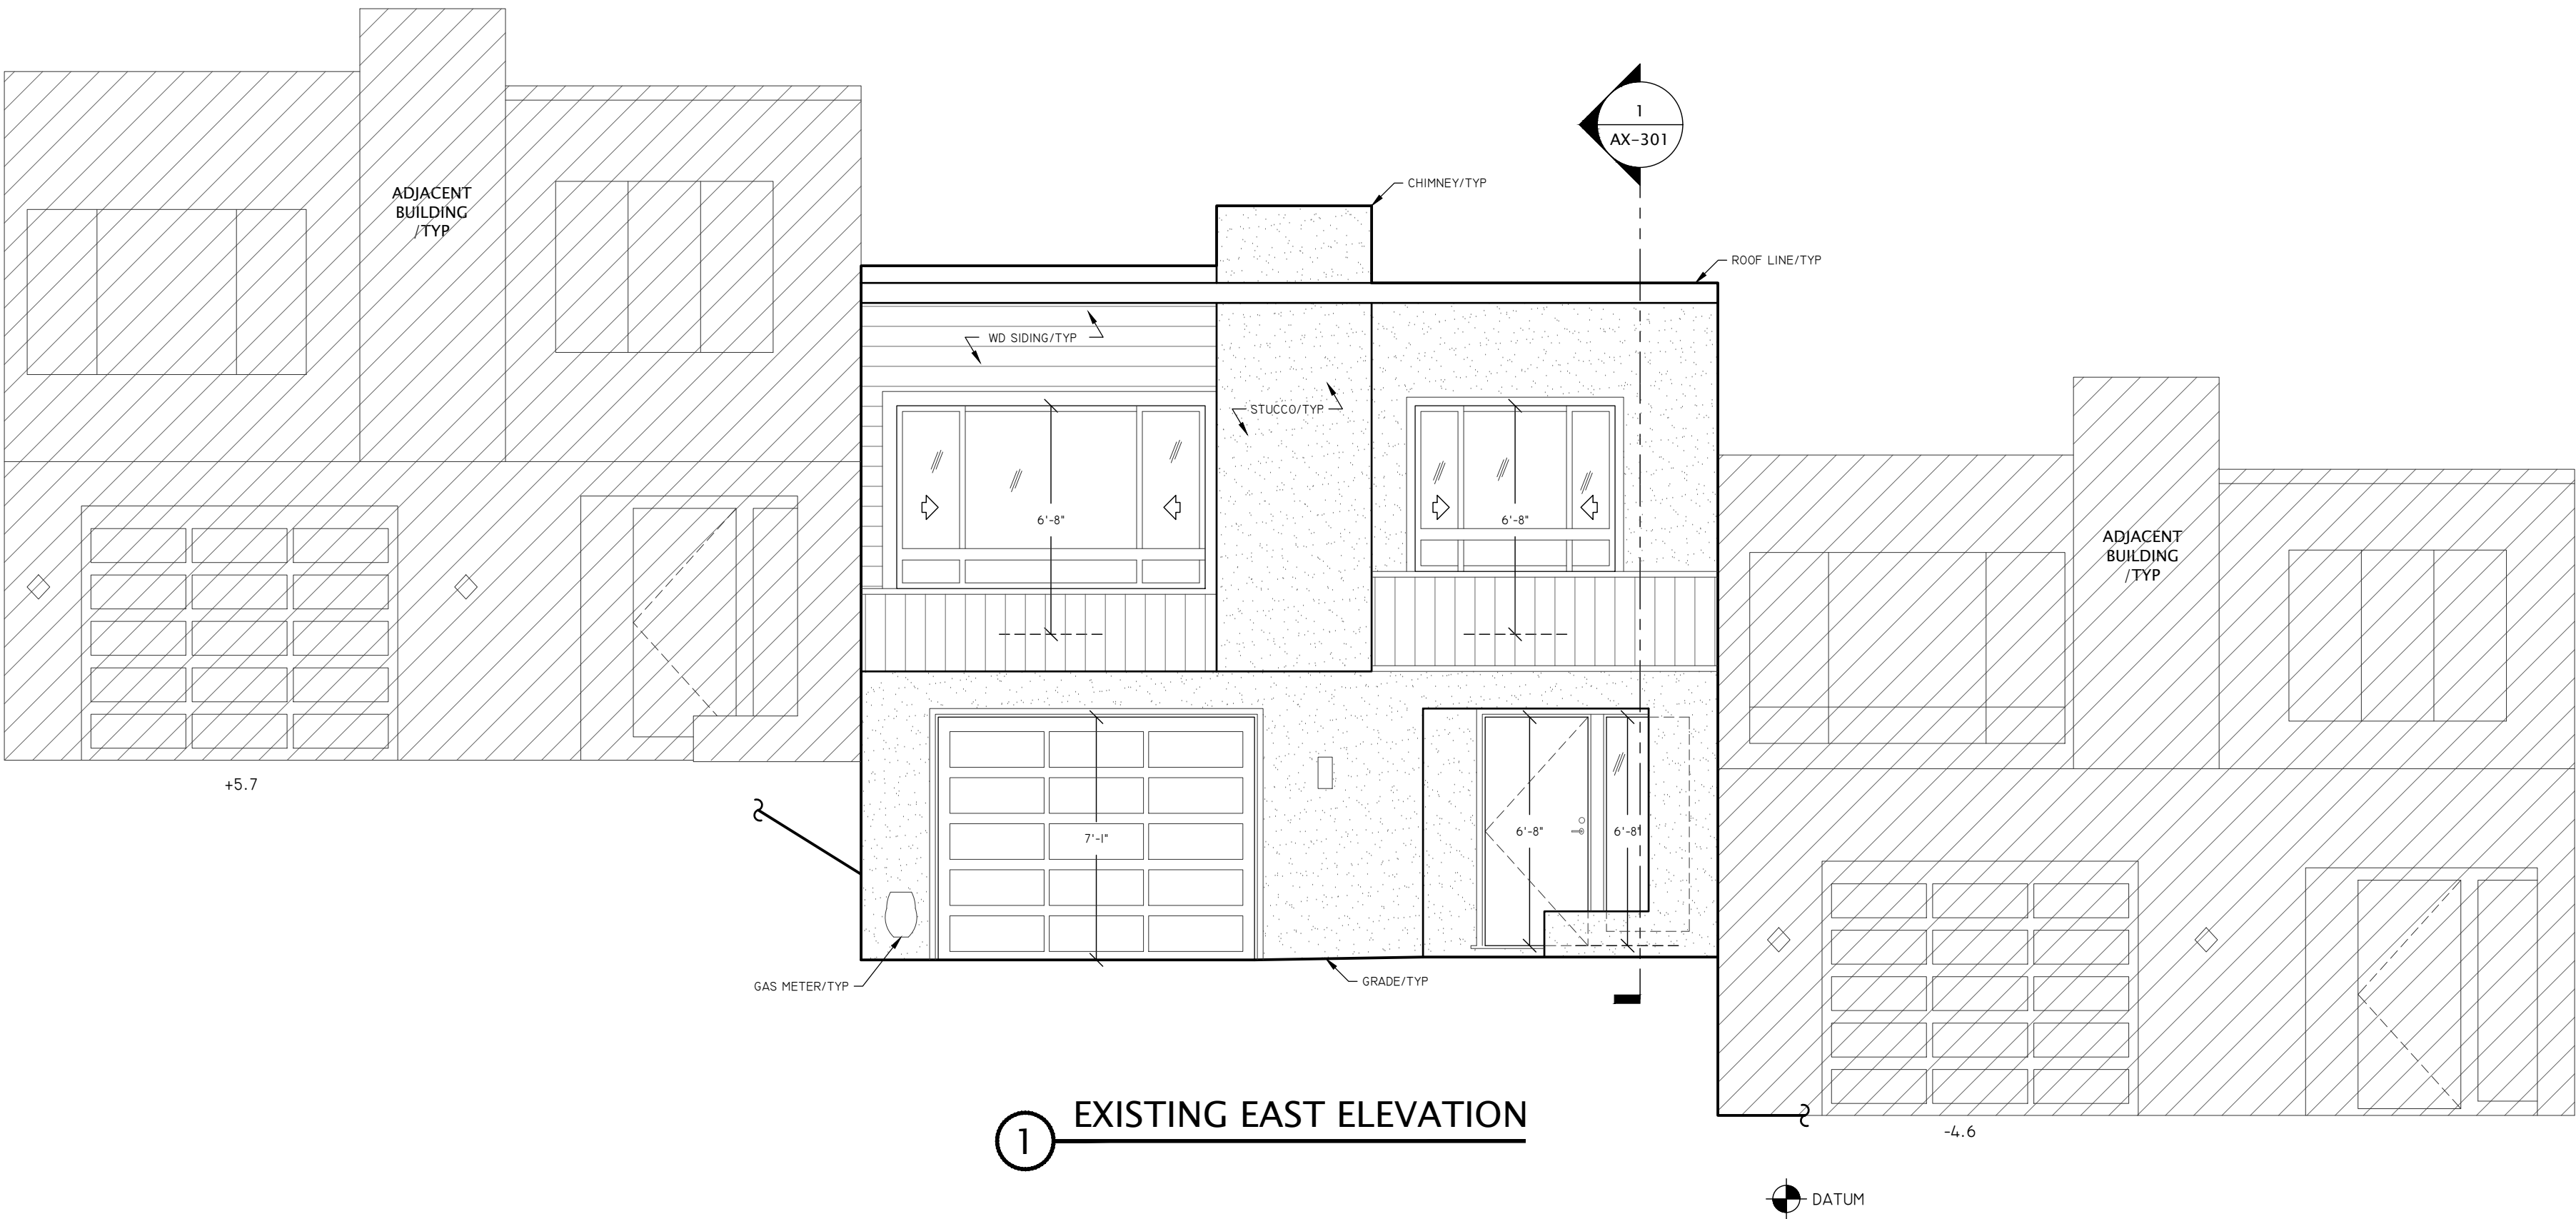


1 EXISTING EAST ELEVATION

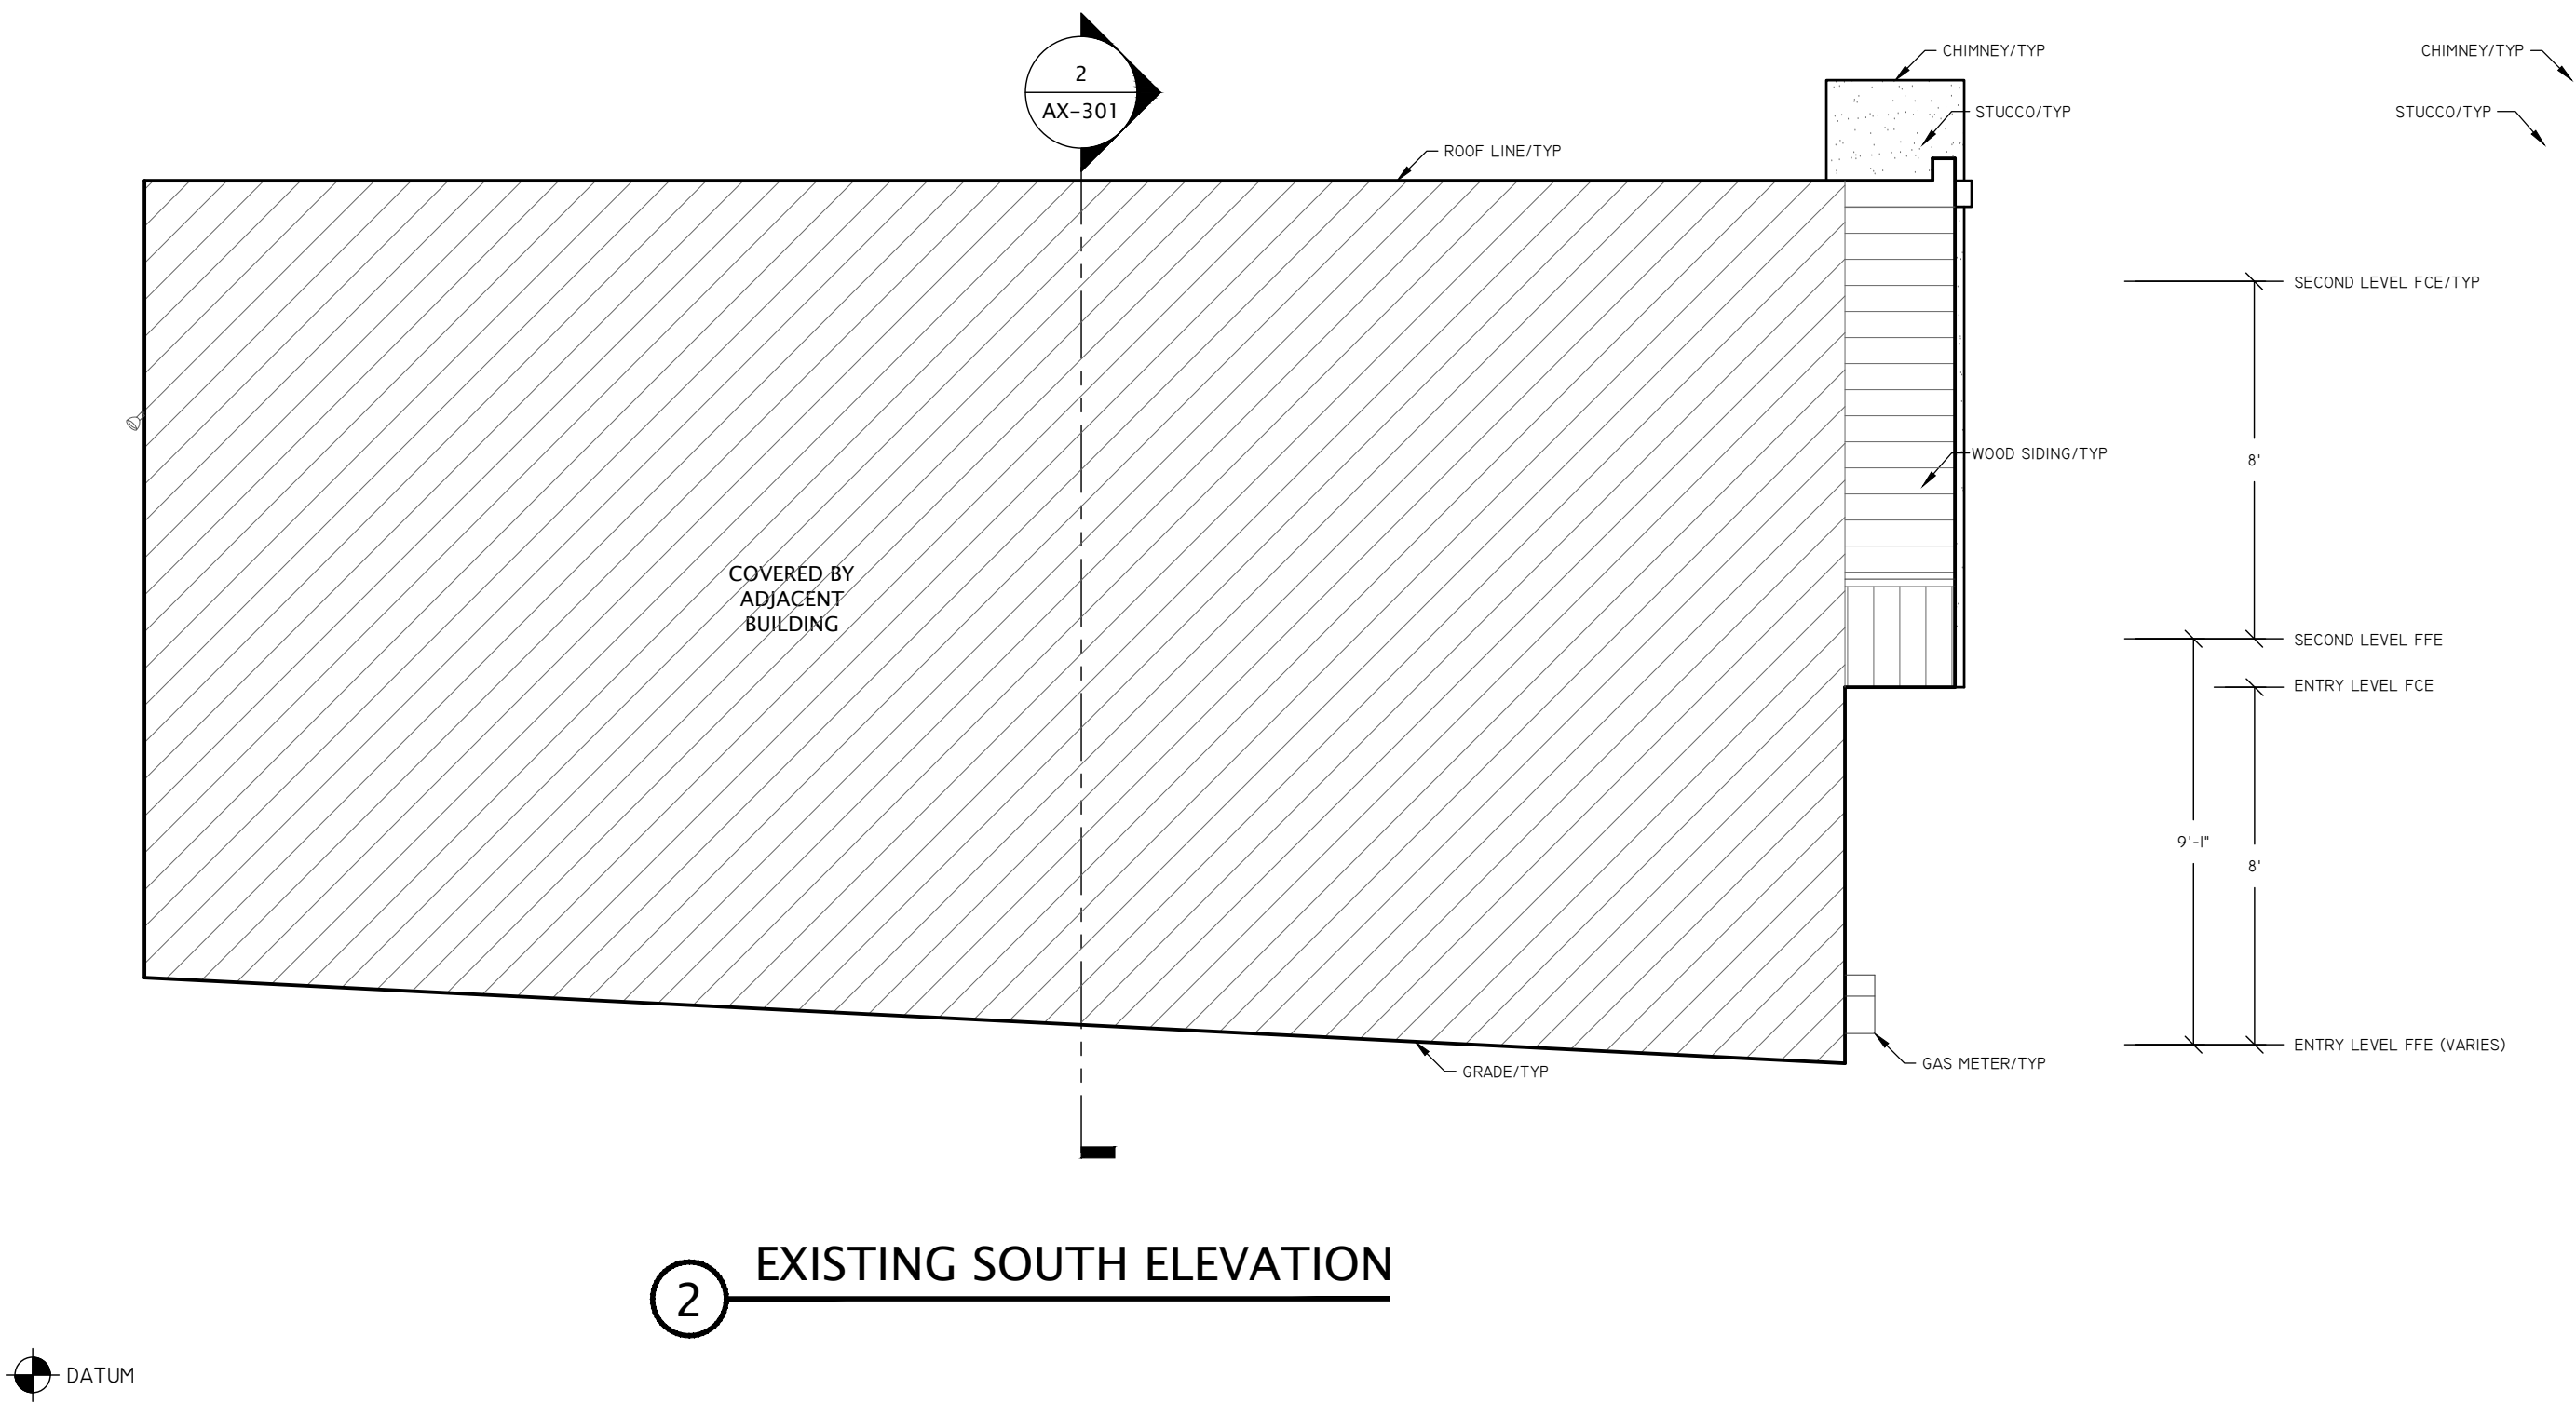


2 EXISTING SOUTH ELEVATION



67 CAYUGA STREET SAN FRANCISCO, CA 94108		
THIS DRAWING IS A RECORD OF REAL PROPERTY THAT IS GENERALLY ACCEPTED TO BE SUITABLE FOR USE IN PLANNING, DESIGN, LEASE, AND GENERAL ASSET MANAGEMENT. IT SHOULD NOT BE USED TO DETERMINE EXACT MEASUREMENTS OF SPACES OR ARTIFACTS FOUND HEREIN FOR ANY PURPOSE.		
EXTERIOR ELEMENTS HAVE BEEN MEASURED AND DRAFTED FOR REFERENCE ONLY - THIS IS NOT A SURVEY.		
 RED BRIDGE DESIGN SAN FRANCISCO REDBRIDGEDESIGN.COM		
EXISTING EXTERIOR ELEVATIONS		
REF: 67sf_City_SFD REV: 0 DRAWN BY: MV AUDITED BY: JK	SHEET SIZE: 24x36 SCALE: 1/4"=1'-0" FIELD MEASURE: 5/1/19	AX-201 4 OF 7

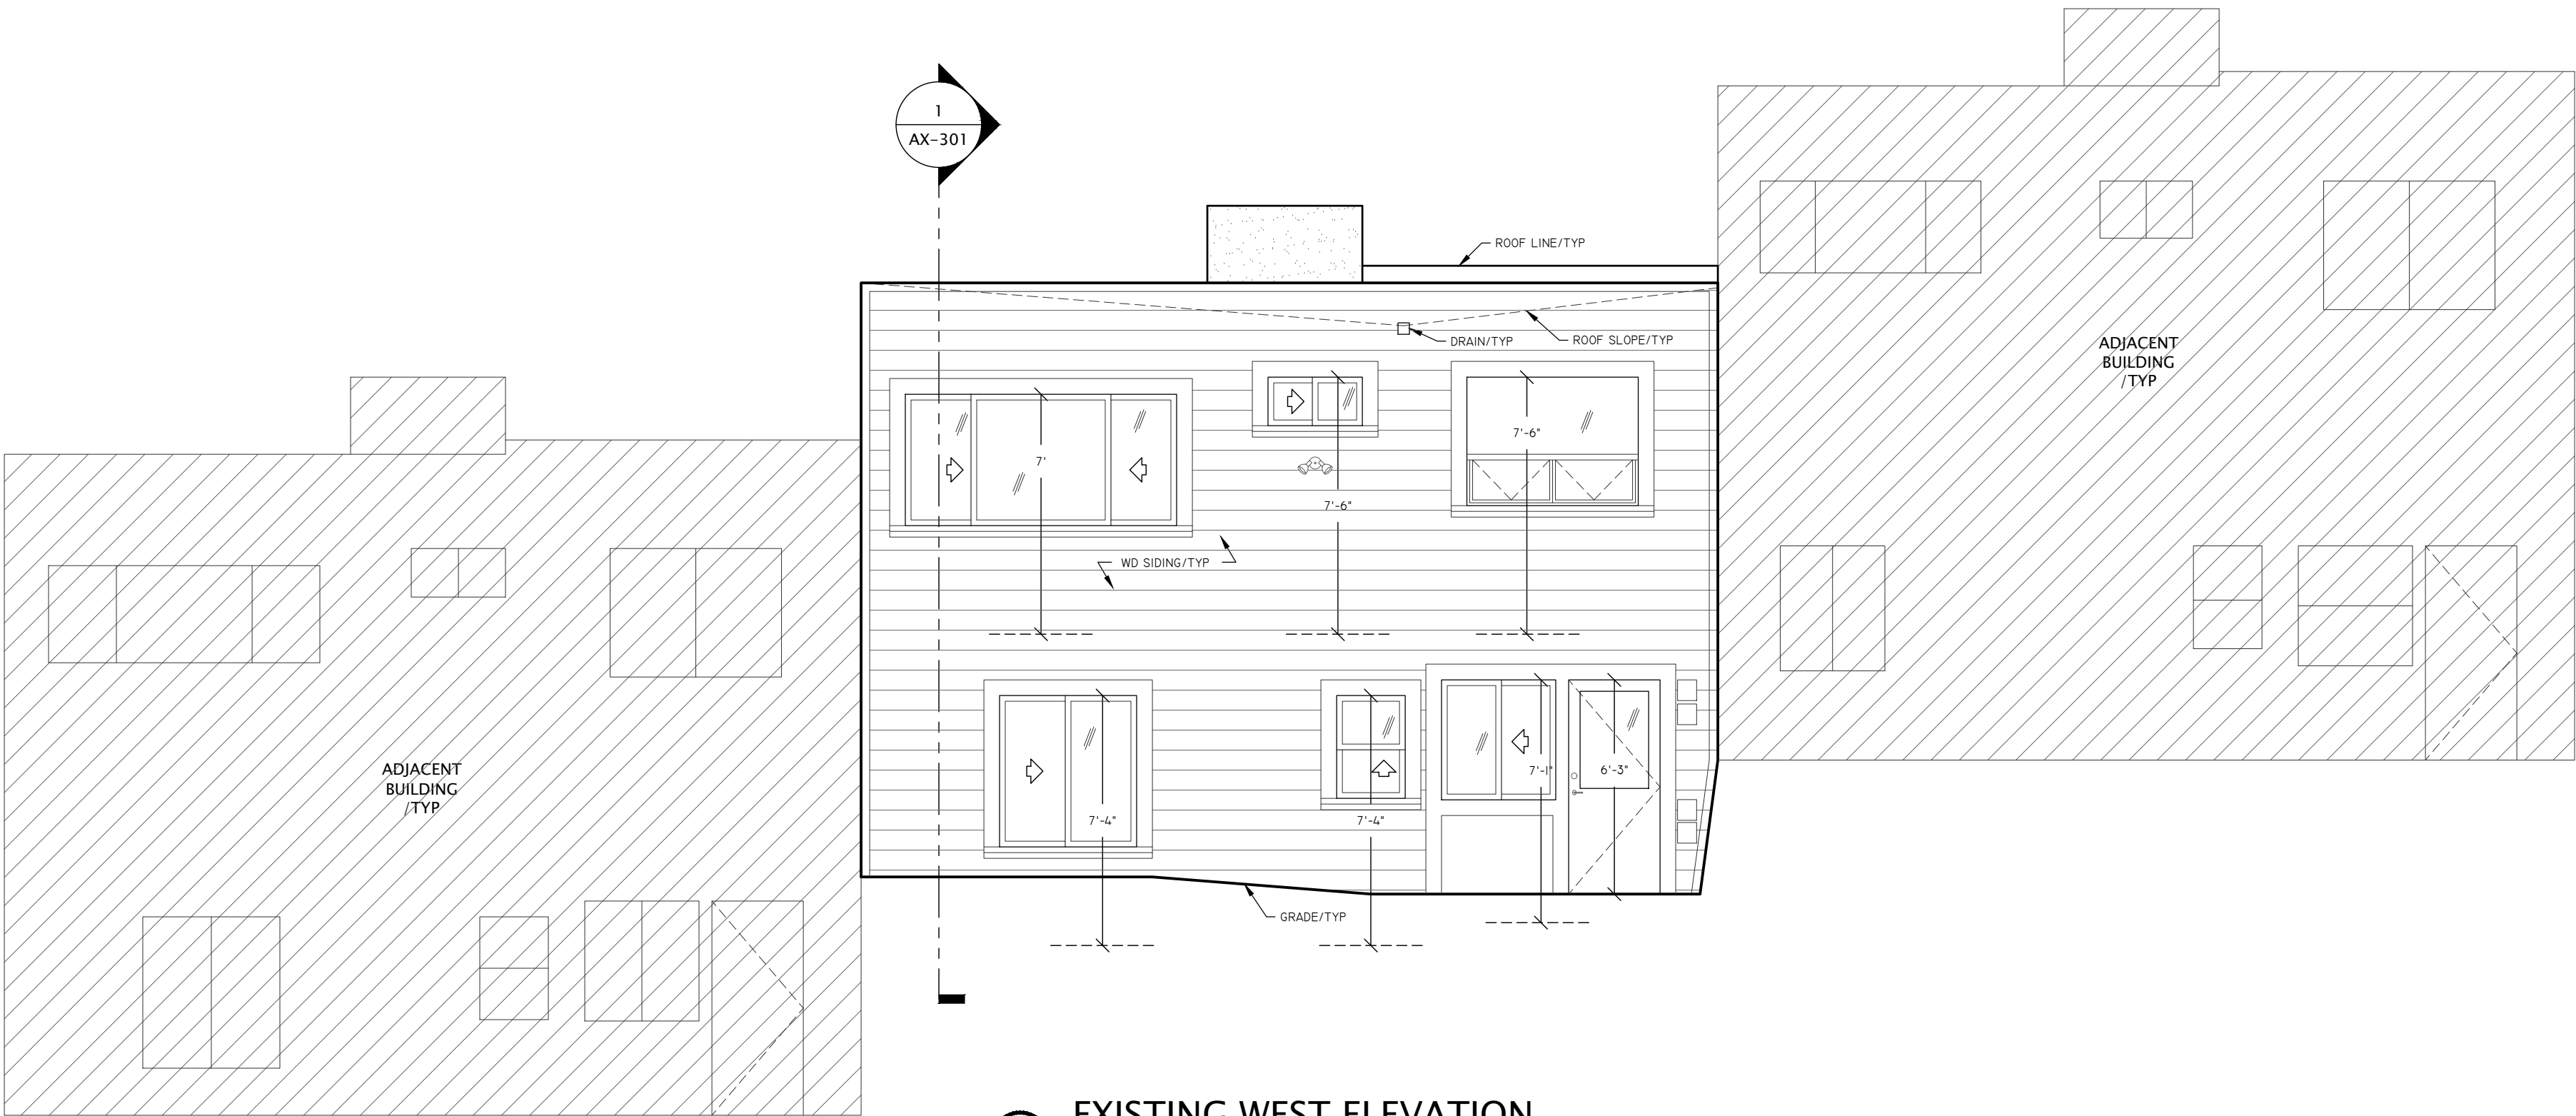


1 EXISTING WEST ELEVATION

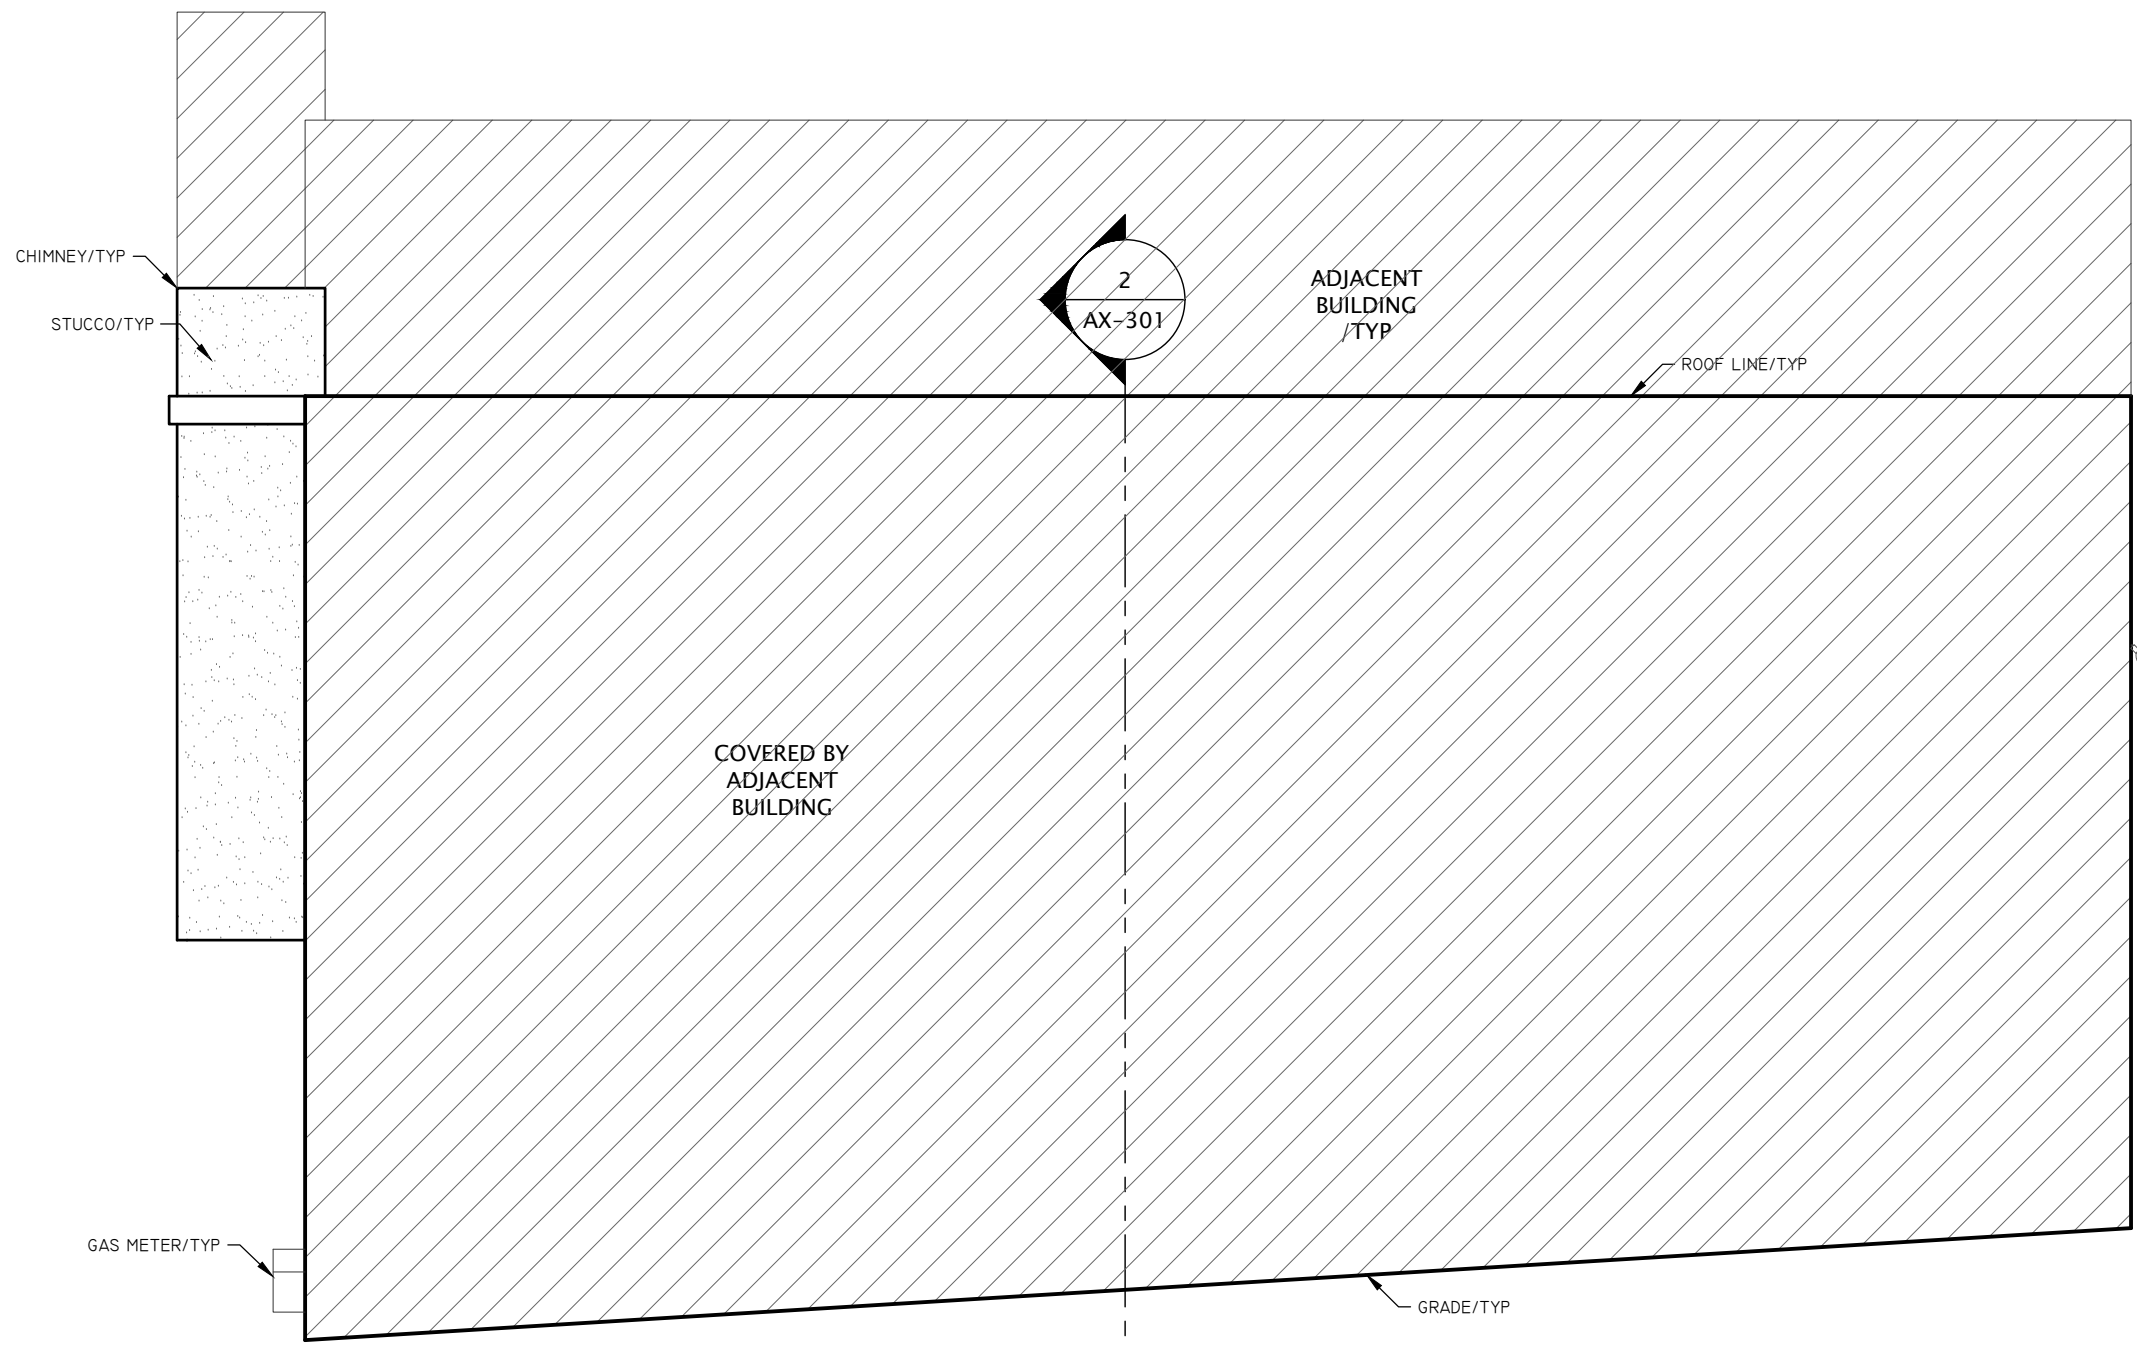


2 EXISTING NORTH ELEVATION

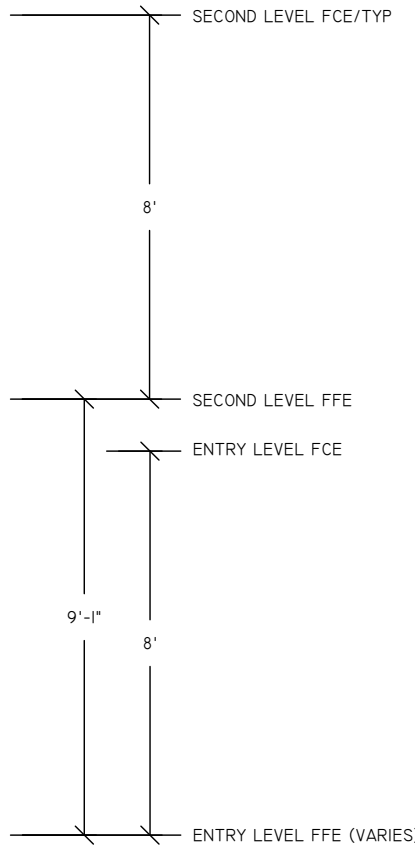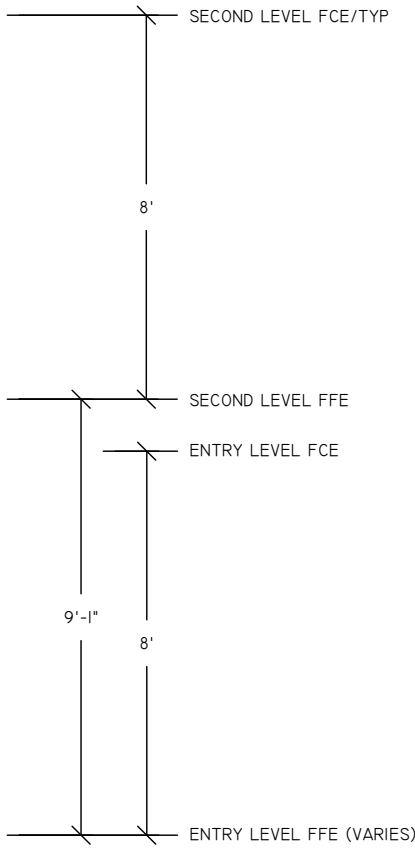

67 CAYUGA STREET SAN FRANCISCO, CA 94108		
THIS DRAWING IS A RECORD OF REAL PROPERTY THAT IS GENERALLY ACCEPTED TO BE SUITABLE FOR USE IN PLANNING, DESIGN, LEASE, AND GENERAL ASSET MANAGEMENT. IT SHOULD NOT BE USED TO DETERMINE EXACT MEASUREMENTS OF SPACES OR ARTIFACTS FOUND HEREIN FOR ANY PURPOSE. EXTERIOR ELEMENTS HAVE BEEN MEASURED AND DRAFTED FOR REFERENCE ONLY - THIS IS NOT A SURVEY.		
		
EXISTING EXTERIOR ELEVATIONS		
REF: 67sf_City_SFD REV: 0 DRAWN BY: MV AUDITED BY: JK	SHEET SIZE: 24x36 SCALE: 1/4"=1'-0" FIELD MEASURE: 5/1/19	AX-202 5 OF 7

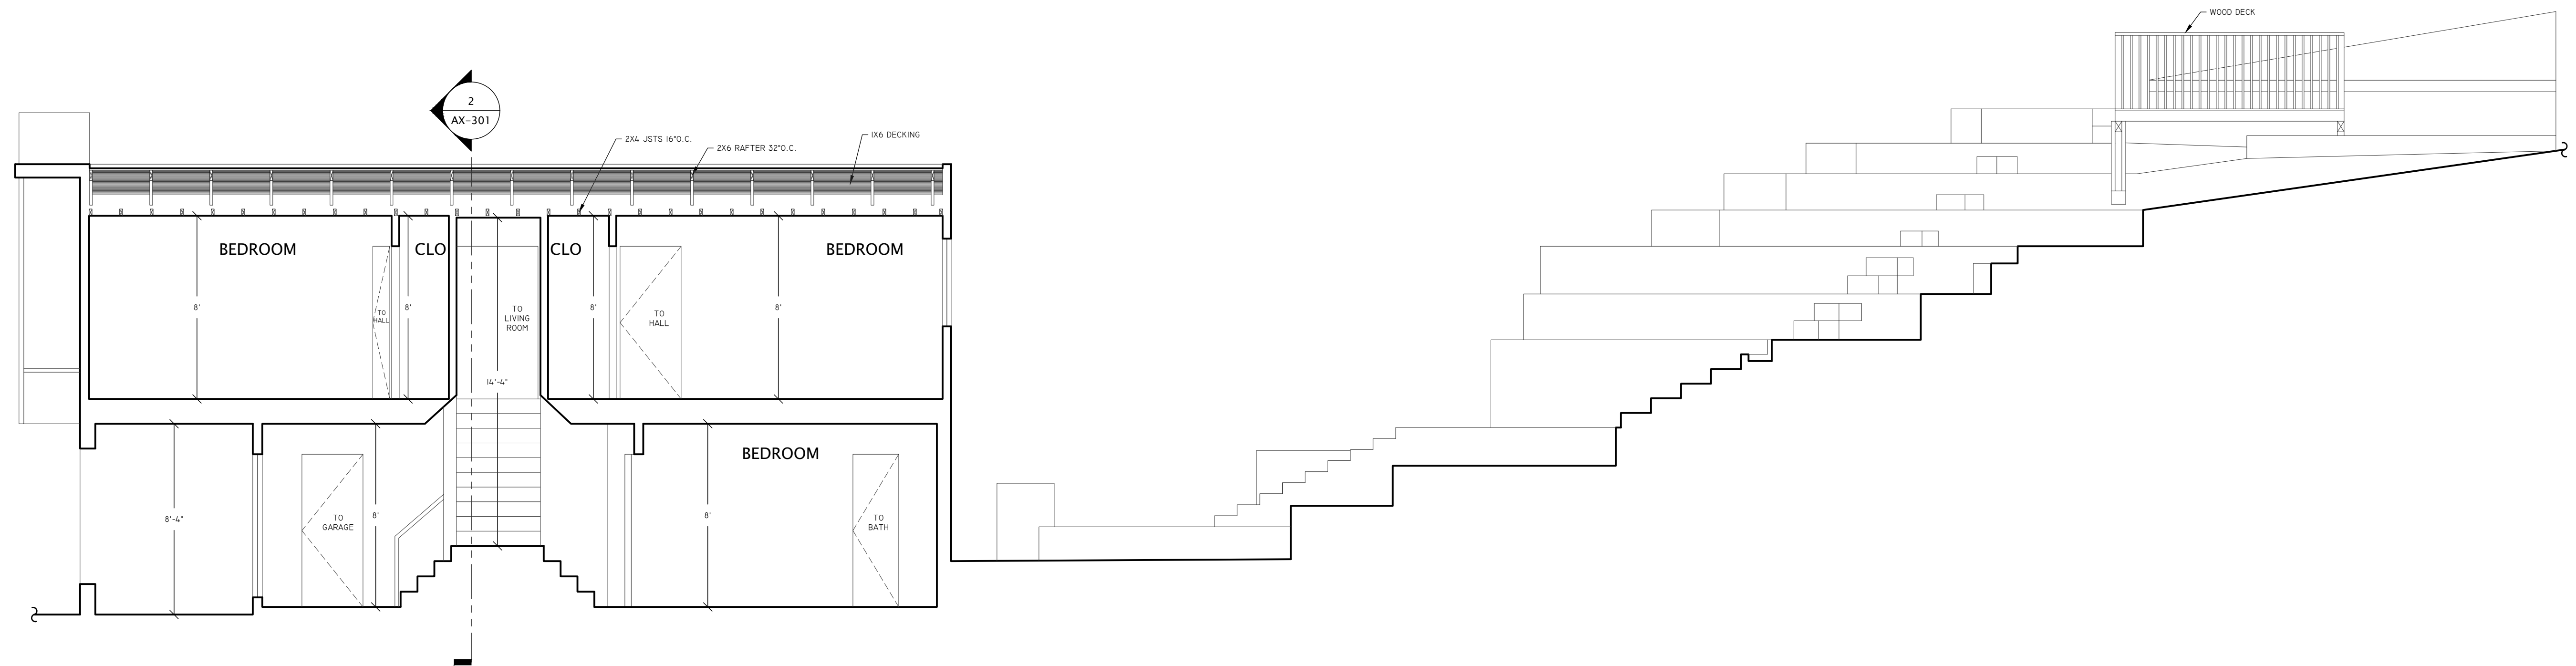

① EXISTING LONGITUDINAL SECTION

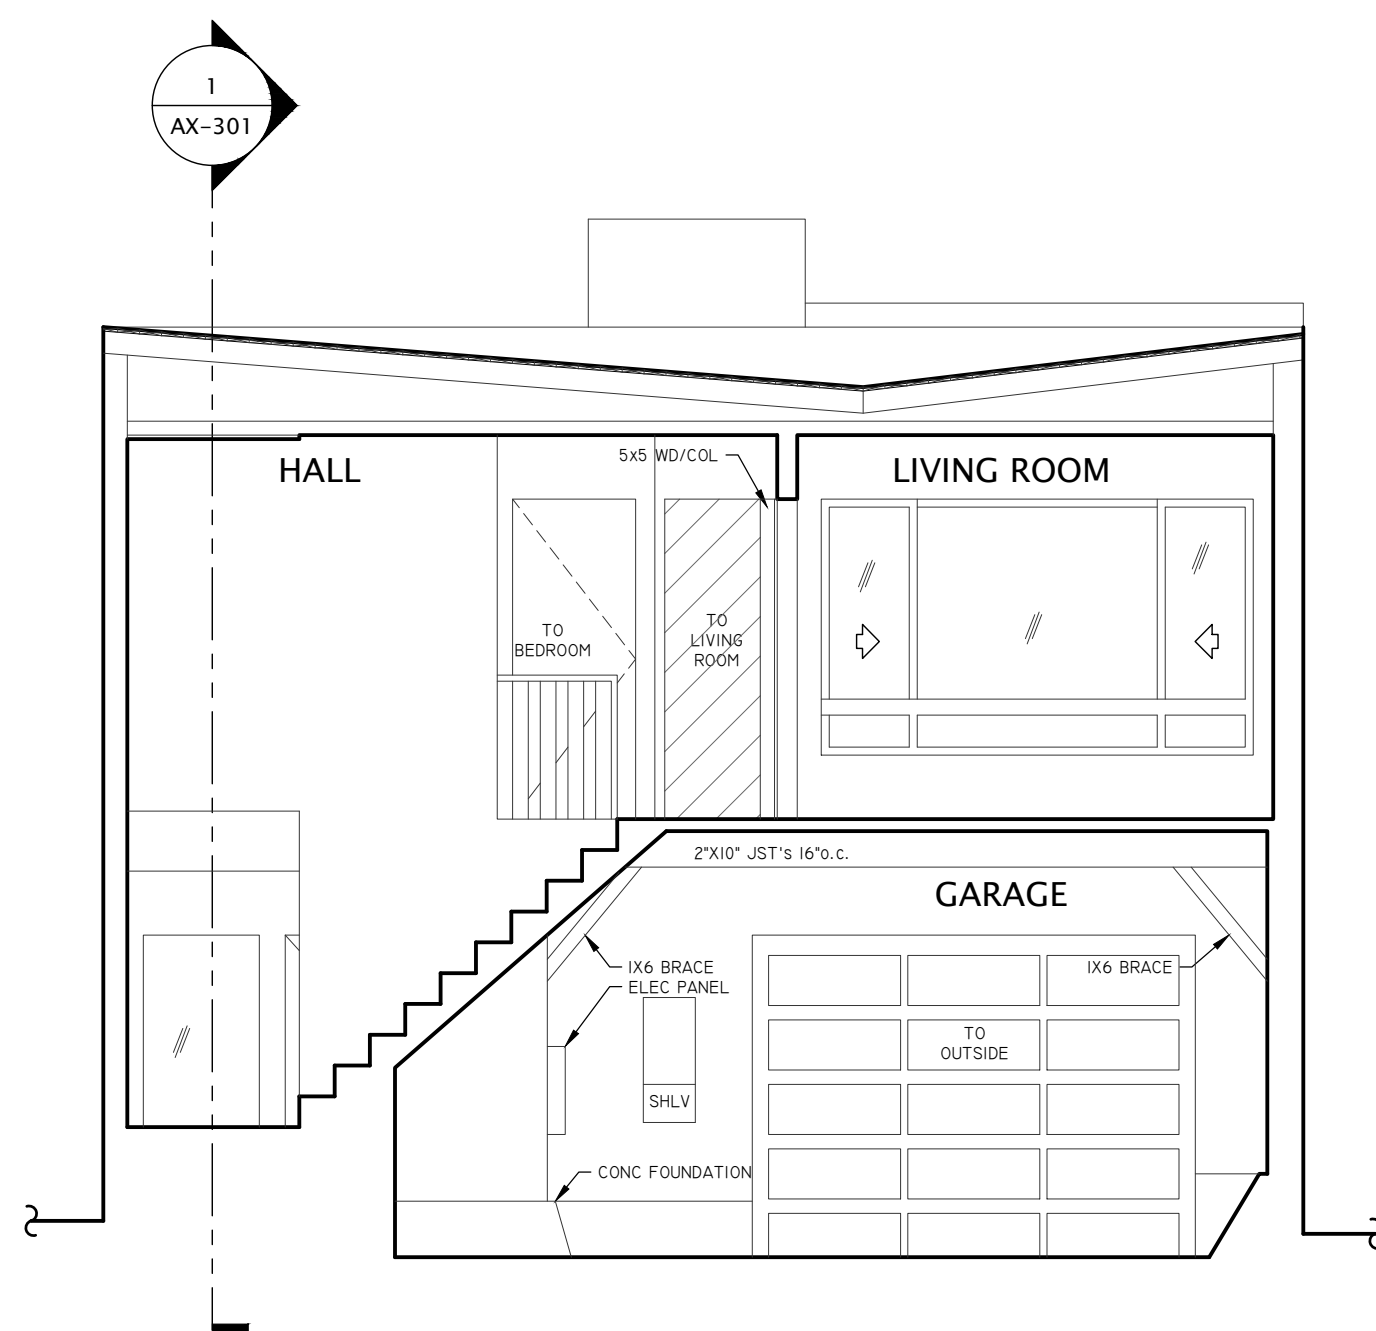

② EXISTING CROSS SECTION



67 CAYUGA STREET
SAN FRANCISCO, CA 94108

THIS DRAWING IS A RECORD OF REAL PROPERTY THAT IS GENERALLY ACCEPTED TO BE SUITABLE FOR USE IN PLANNING, DESIGN, LEASE, AND GENERAL ASSET MANAGEMENT. IT SHOULD NOT BE USED TO DETERMINE EXACT MEASUREMENTS OF SPACES OR ARTIFACTS FOUND HEREIN FOR ANY PURPOSE.
EXTERIOR ELEMENTS HAVE BEEN MEASURED AND DRAFTED FOR REFERENCE ONLY - THIS IS NOT A SURVEY.




EXISTING BUILDING SECTIONS


REF: 67sf_City_SFD
REV: 0
DRAWN BY: MV
AUDITED BY: JK

SHEET SIZE: 24x36
SCALE: 1/4"=1'-0"
FIELD MEASURE:
5/1/19

AX-301
6 OF 7

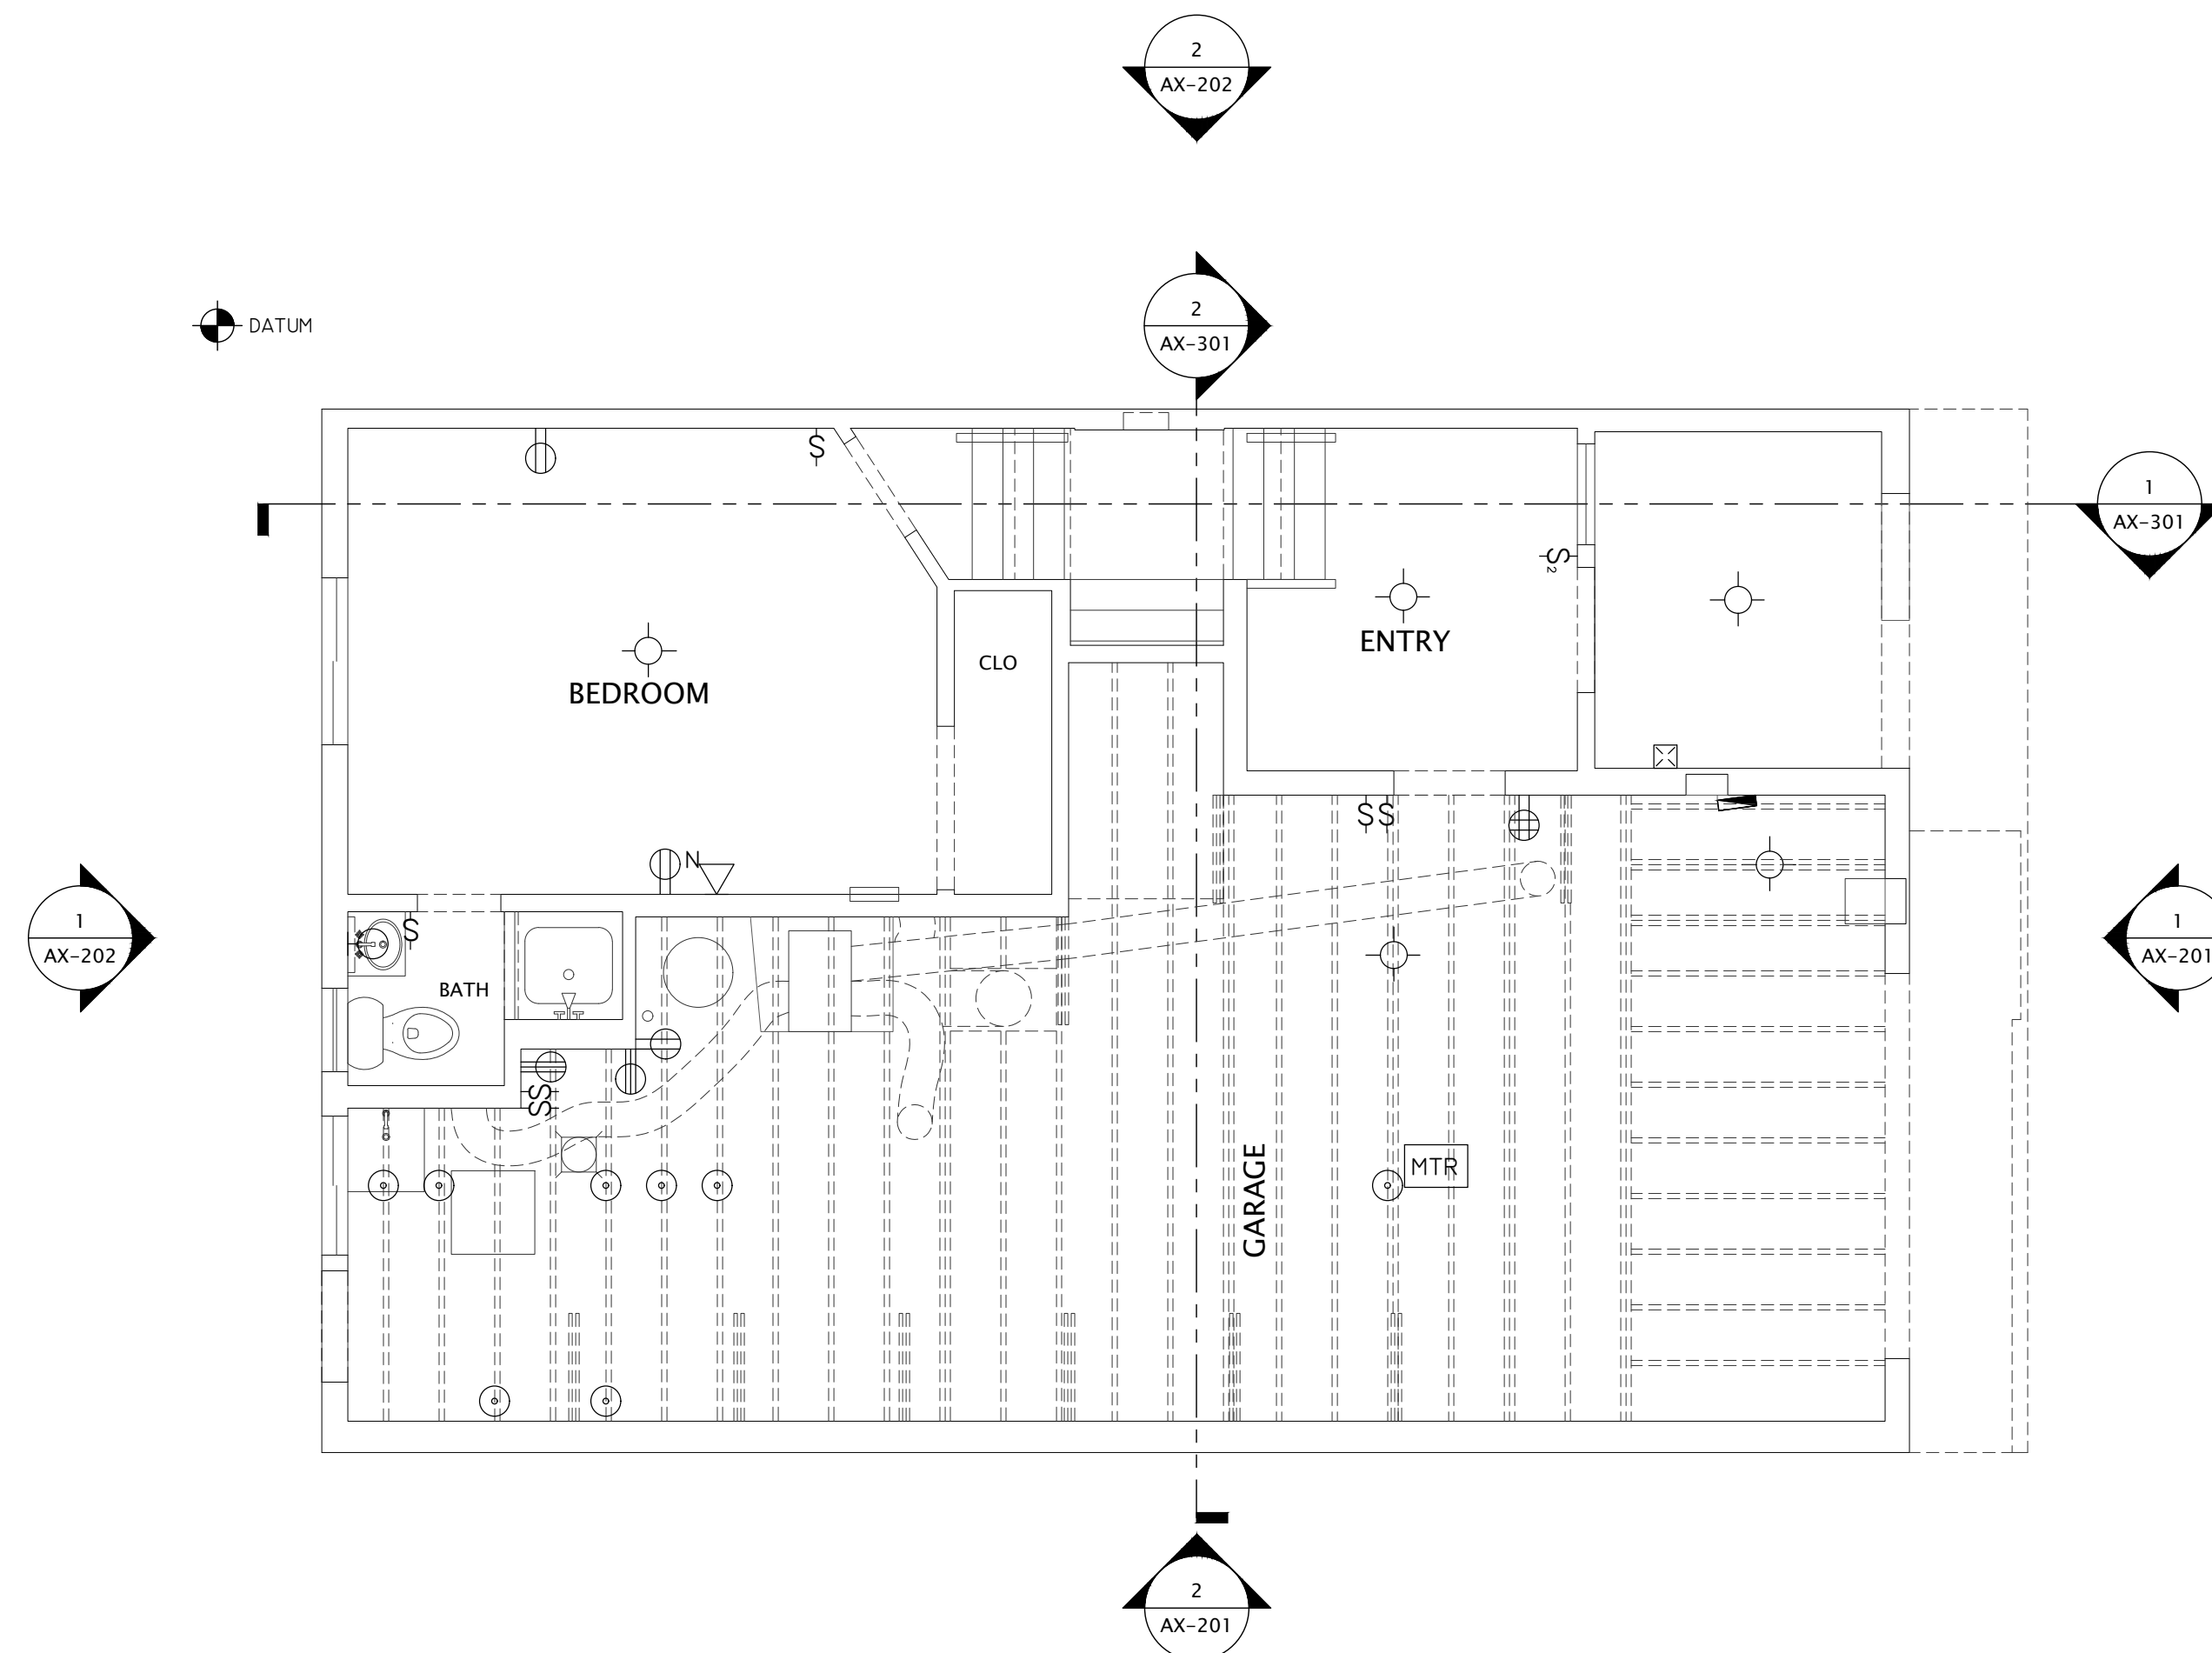

1 EXISTING ENTRY LEVEL ELECTRICAL & LIGHTING PLAN

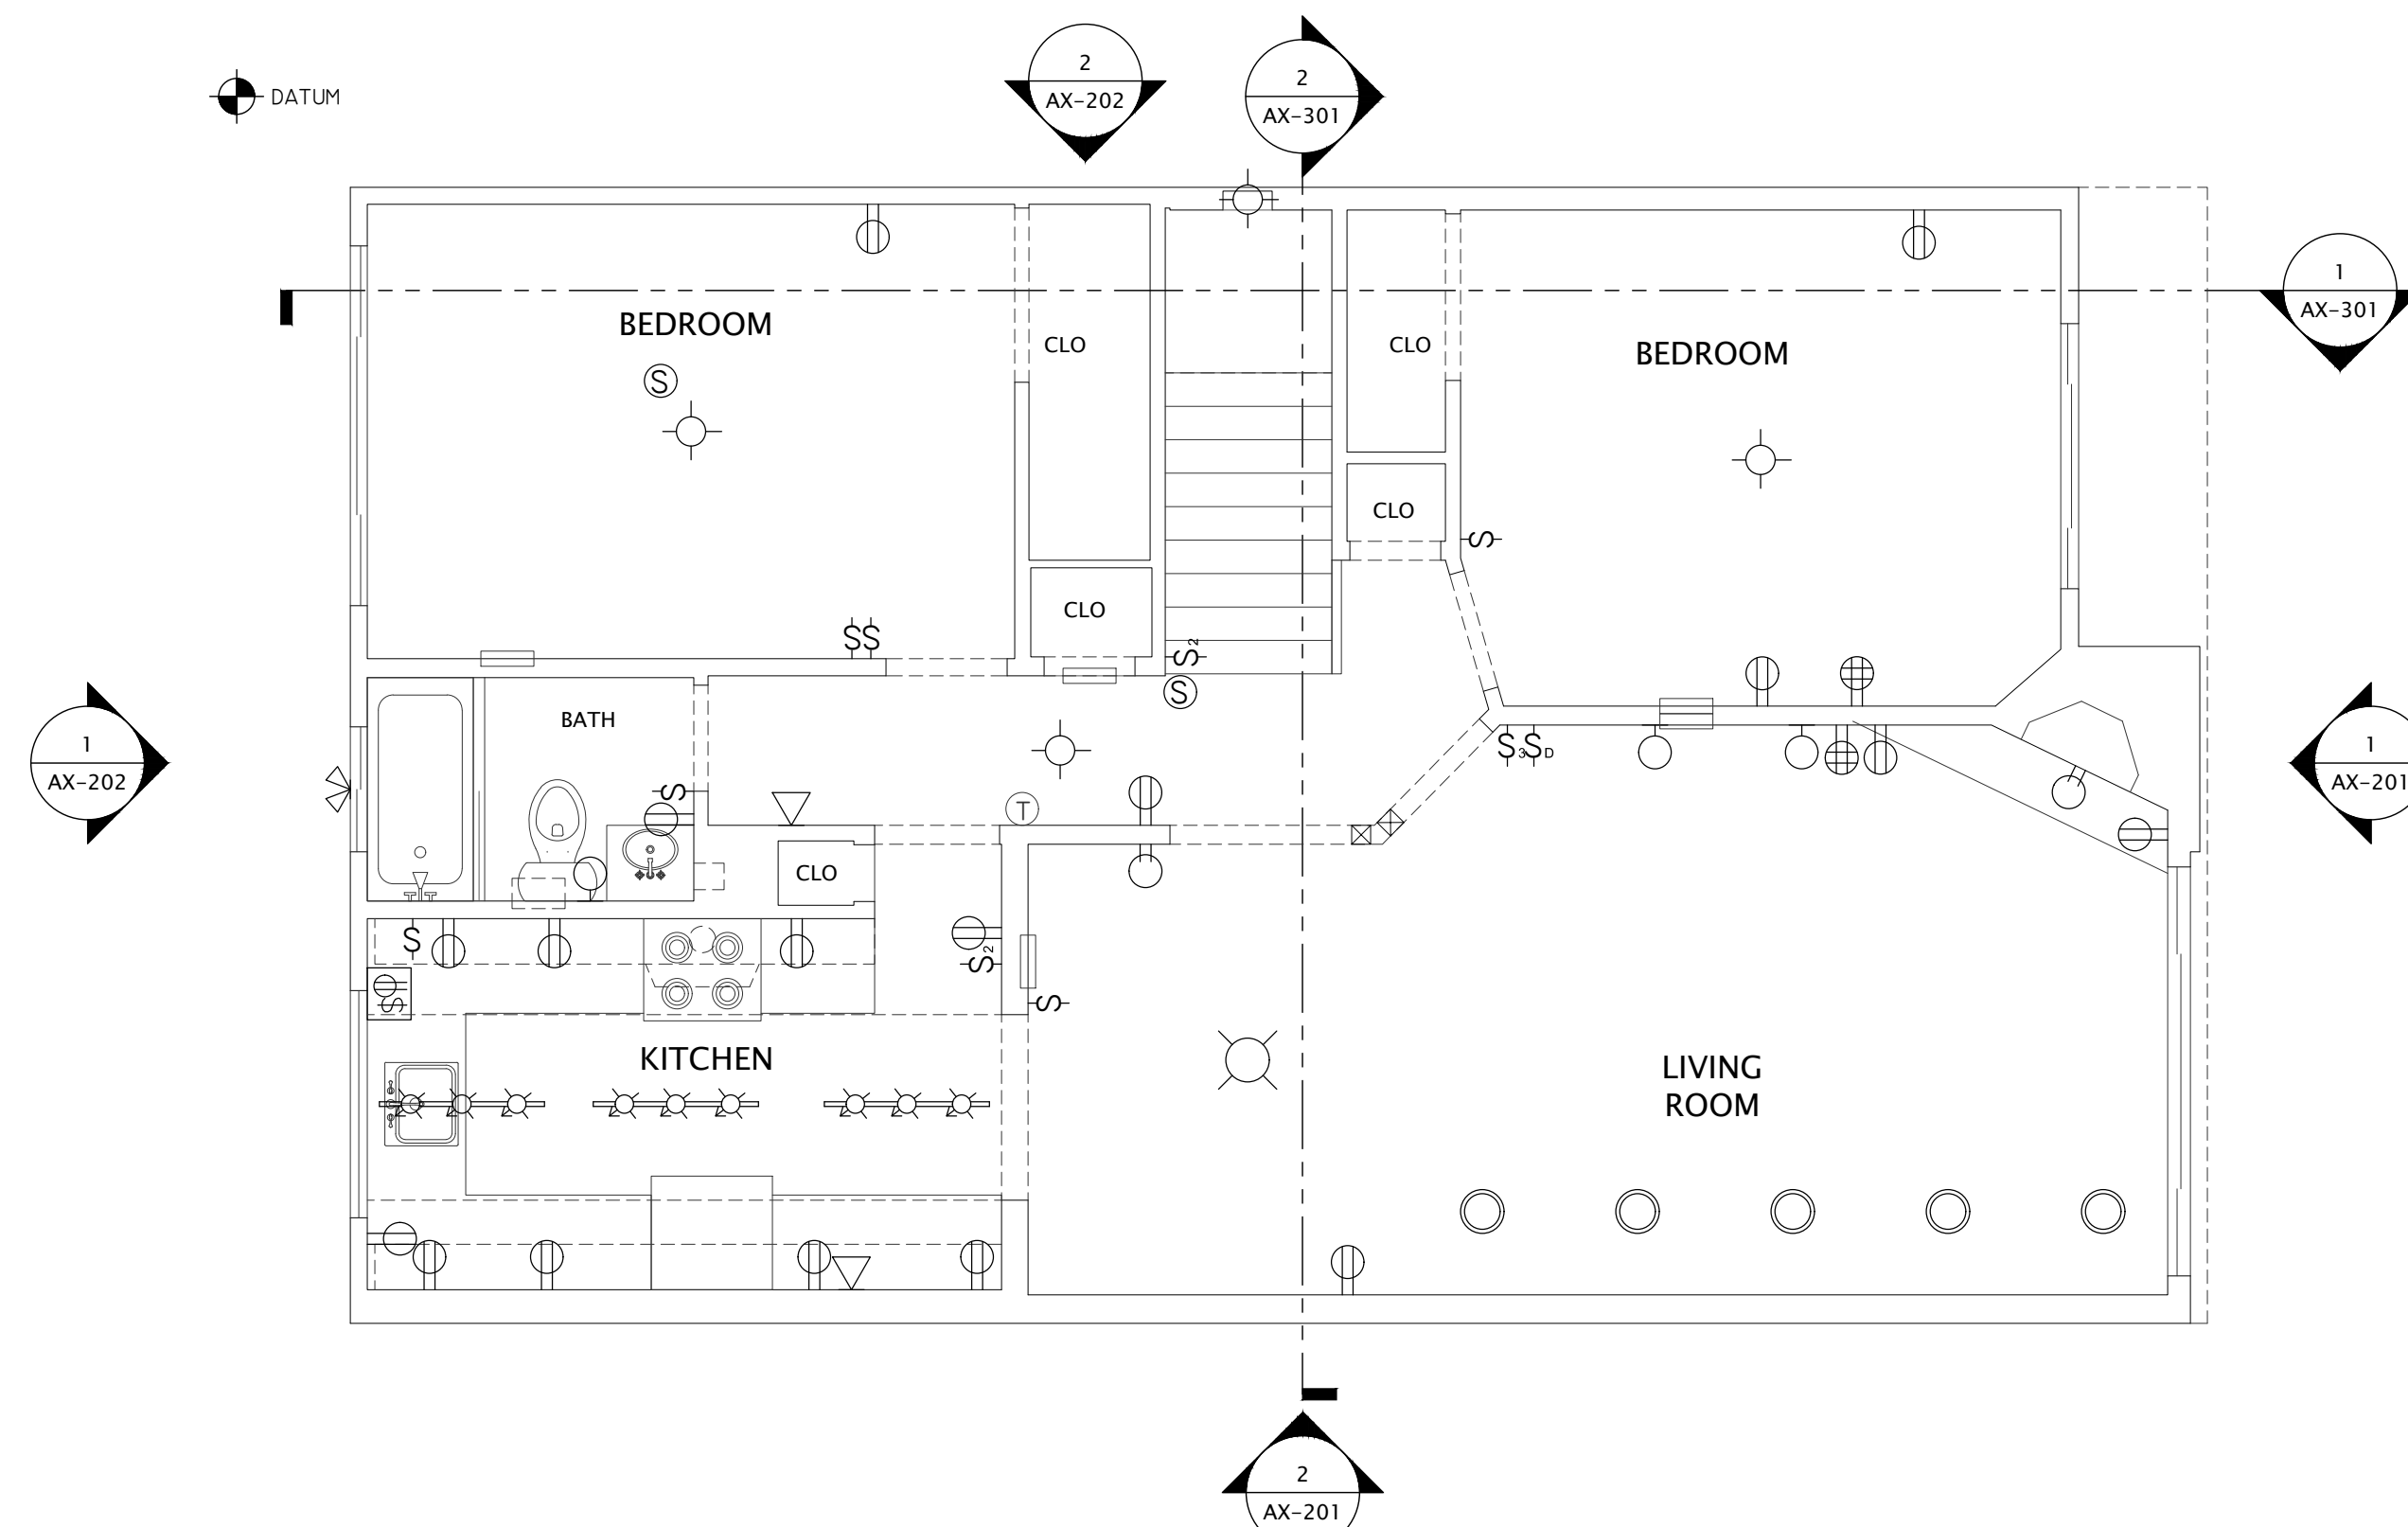

2 EXISTING SECOND LEVEL ELECTRICAL & LIGHTING PLAN

LEGEND	
⌘ ⌘ ⌘ ⌘	SWITCH, ⌘ = TWO GANG, ETC
⌘	DIMMER SWITCH
⊕	RECEPTACLE
⊕	QUAD RECEPTACLE
⊕	220 RECEPTACLE
⊕	FLOOR RECEPTACLE
⊕	FACE PLATE/JUNCTION BOX
⊕	RECEPTACLE/SWITCH UNIT
⊕	RECESSED LIGHTING
⊕	SURFACE/CLG MOUNT
⊕	WALL MOUNT
⊕	HANGING LIGHT
⊕	TRACK LIGHTING
⊕	FLOOD LIGHT
⊕	PHONE JACK
⊕	SMOKE DETECTOR
⊕	THERMOSTAT
⊕	GARAGE MOTOR
⊕	GARAGE MOTOR

67 CAYUGA STREET
SAN FRANCISCO, CA 94108

THIS DRAWING IS A RECORD OF REAL PROPERTY THAT IS GENERALLY ACCEPTED TO BE SUITABLE FOR USE IN PLANNING, DESIGN, LEASE, AND GENERAL ASSET MANAGEMENT. IT SHOULD NOT BE USED TO DETERMINE EXACT MEASUREMENTS OF SPACES OR ARTIFACTS FOUND HEREIN FOR ANY PURPOSE.

EXTERIOR ELEMENTS HAVE BEEN MEASURED AND DRAFTED FOR REFERENCE ONLY - THIS IS NOT A SURVEY.



RED BRIDGE DESIGN
SAN FRANCISCO
REDBRIDGEDESIGN.COM

EXISTING ELECTRICAL & LIGHTING PLAN

REF: 67sf_City_SFD
REV: 0
DRAWN BY: MV
AUDITED BY: JK

SHEET SIZE: 24x36
SCALE: 1/4"=1'-0"
FIELD MEASURE:
5/1/19

EX-101
7 OF 7