



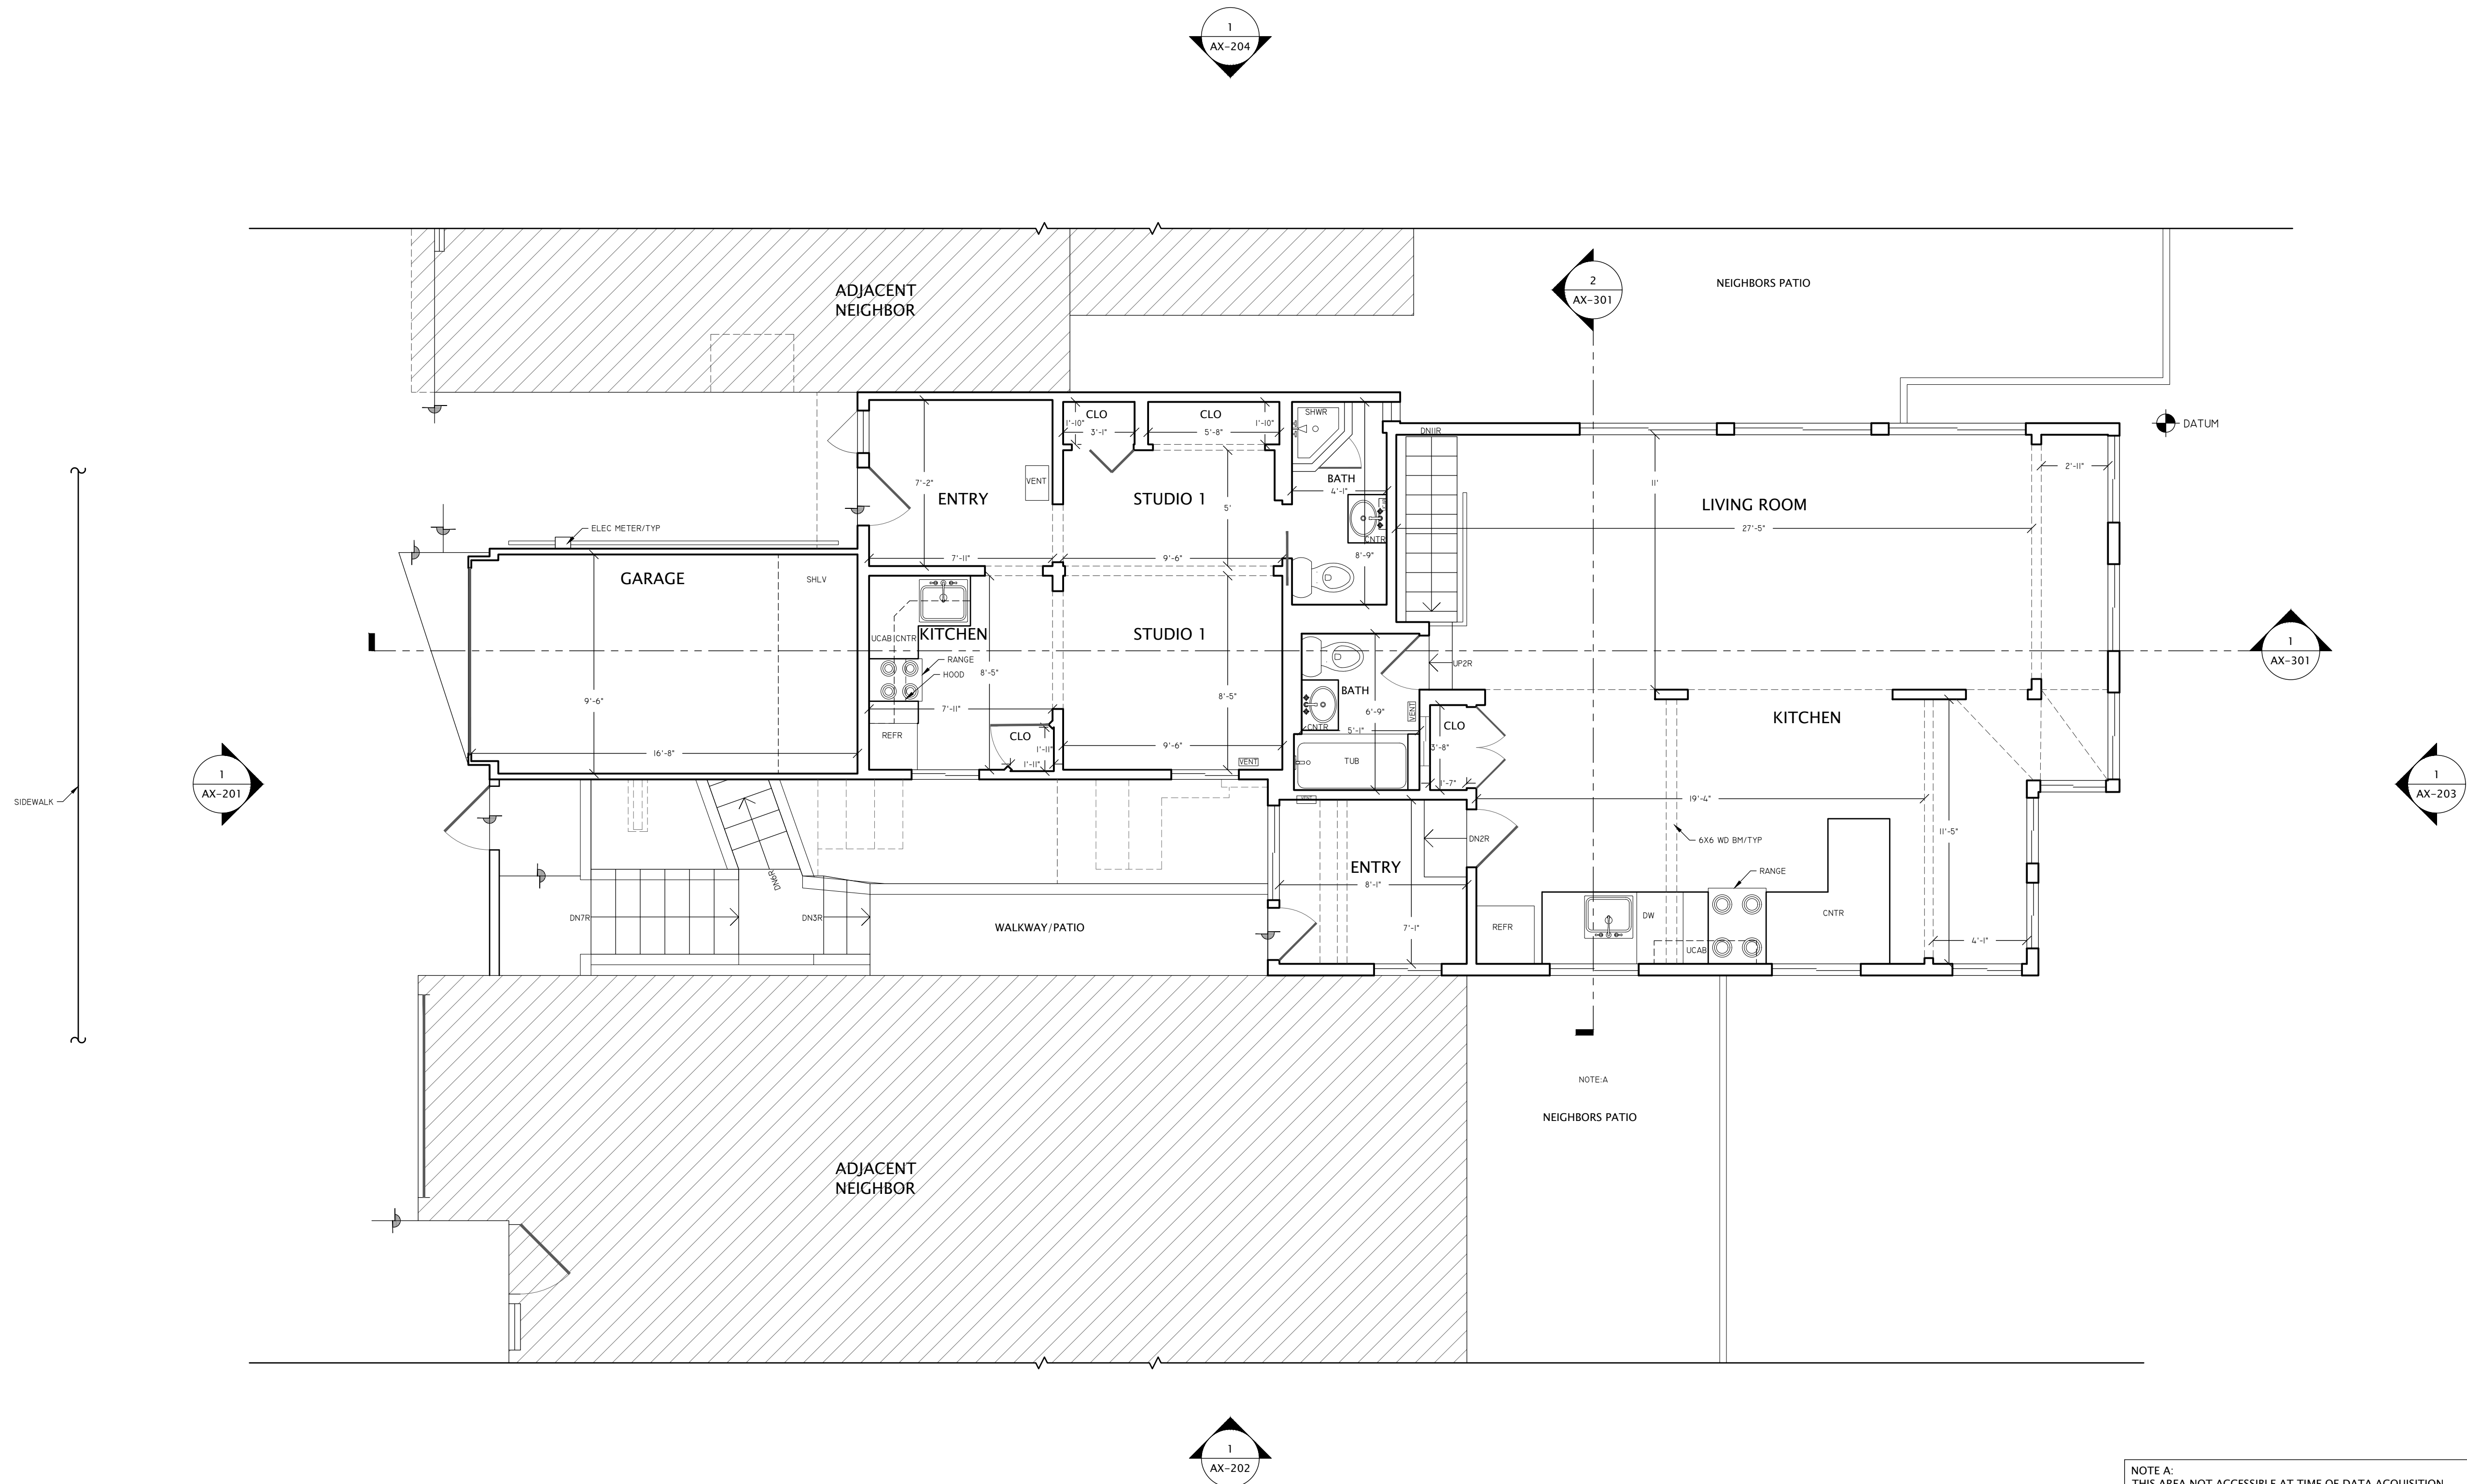

1 EXISTING ENTRY LEVEL FLOOR PLAN
1,318 SQFT GROSS MEASURED AREA
284 SQFT MEASURED EXTERIOR SURFACES

NOTE A:
THIS AREA NOT ACCESSIBLE AT TIME OF DATA ACQUISITION,
AREA NOT MEASURED.

697 RHODE ISLAND STREET SAN FRANCISCO, CA 94107		
THIS DRAWING IS A RECORD OF REAL PROPERTY THAT IS GENERALLY ACCEPTED TO BE SUITABLE FOR USE IN PLANNING, DESIGN, LEASE, AND GENERAL ASSET MANAGEMENT. IT SHOULD NOT BE USED TO DETERMINE EXACT MEASUREMENTS OF SPACES OR ARTIFACTS FOUND HEREIN FOR ANY PURPOSE.		
 RED BRIDGE DESIGN SAN FRANCISCO REDBRIDGEDESIGN.COM		
EXISTING FLOOR PLAN		
REF: 697sf_City_SFD REV: 0 DRAWN BY: MV AUDITED BY: JK	SHEET SIZE: 24x36 SCALE: 1/4"=1'-0" FIELD MEASURE: 4/10/20	AX-101 1 OF 7

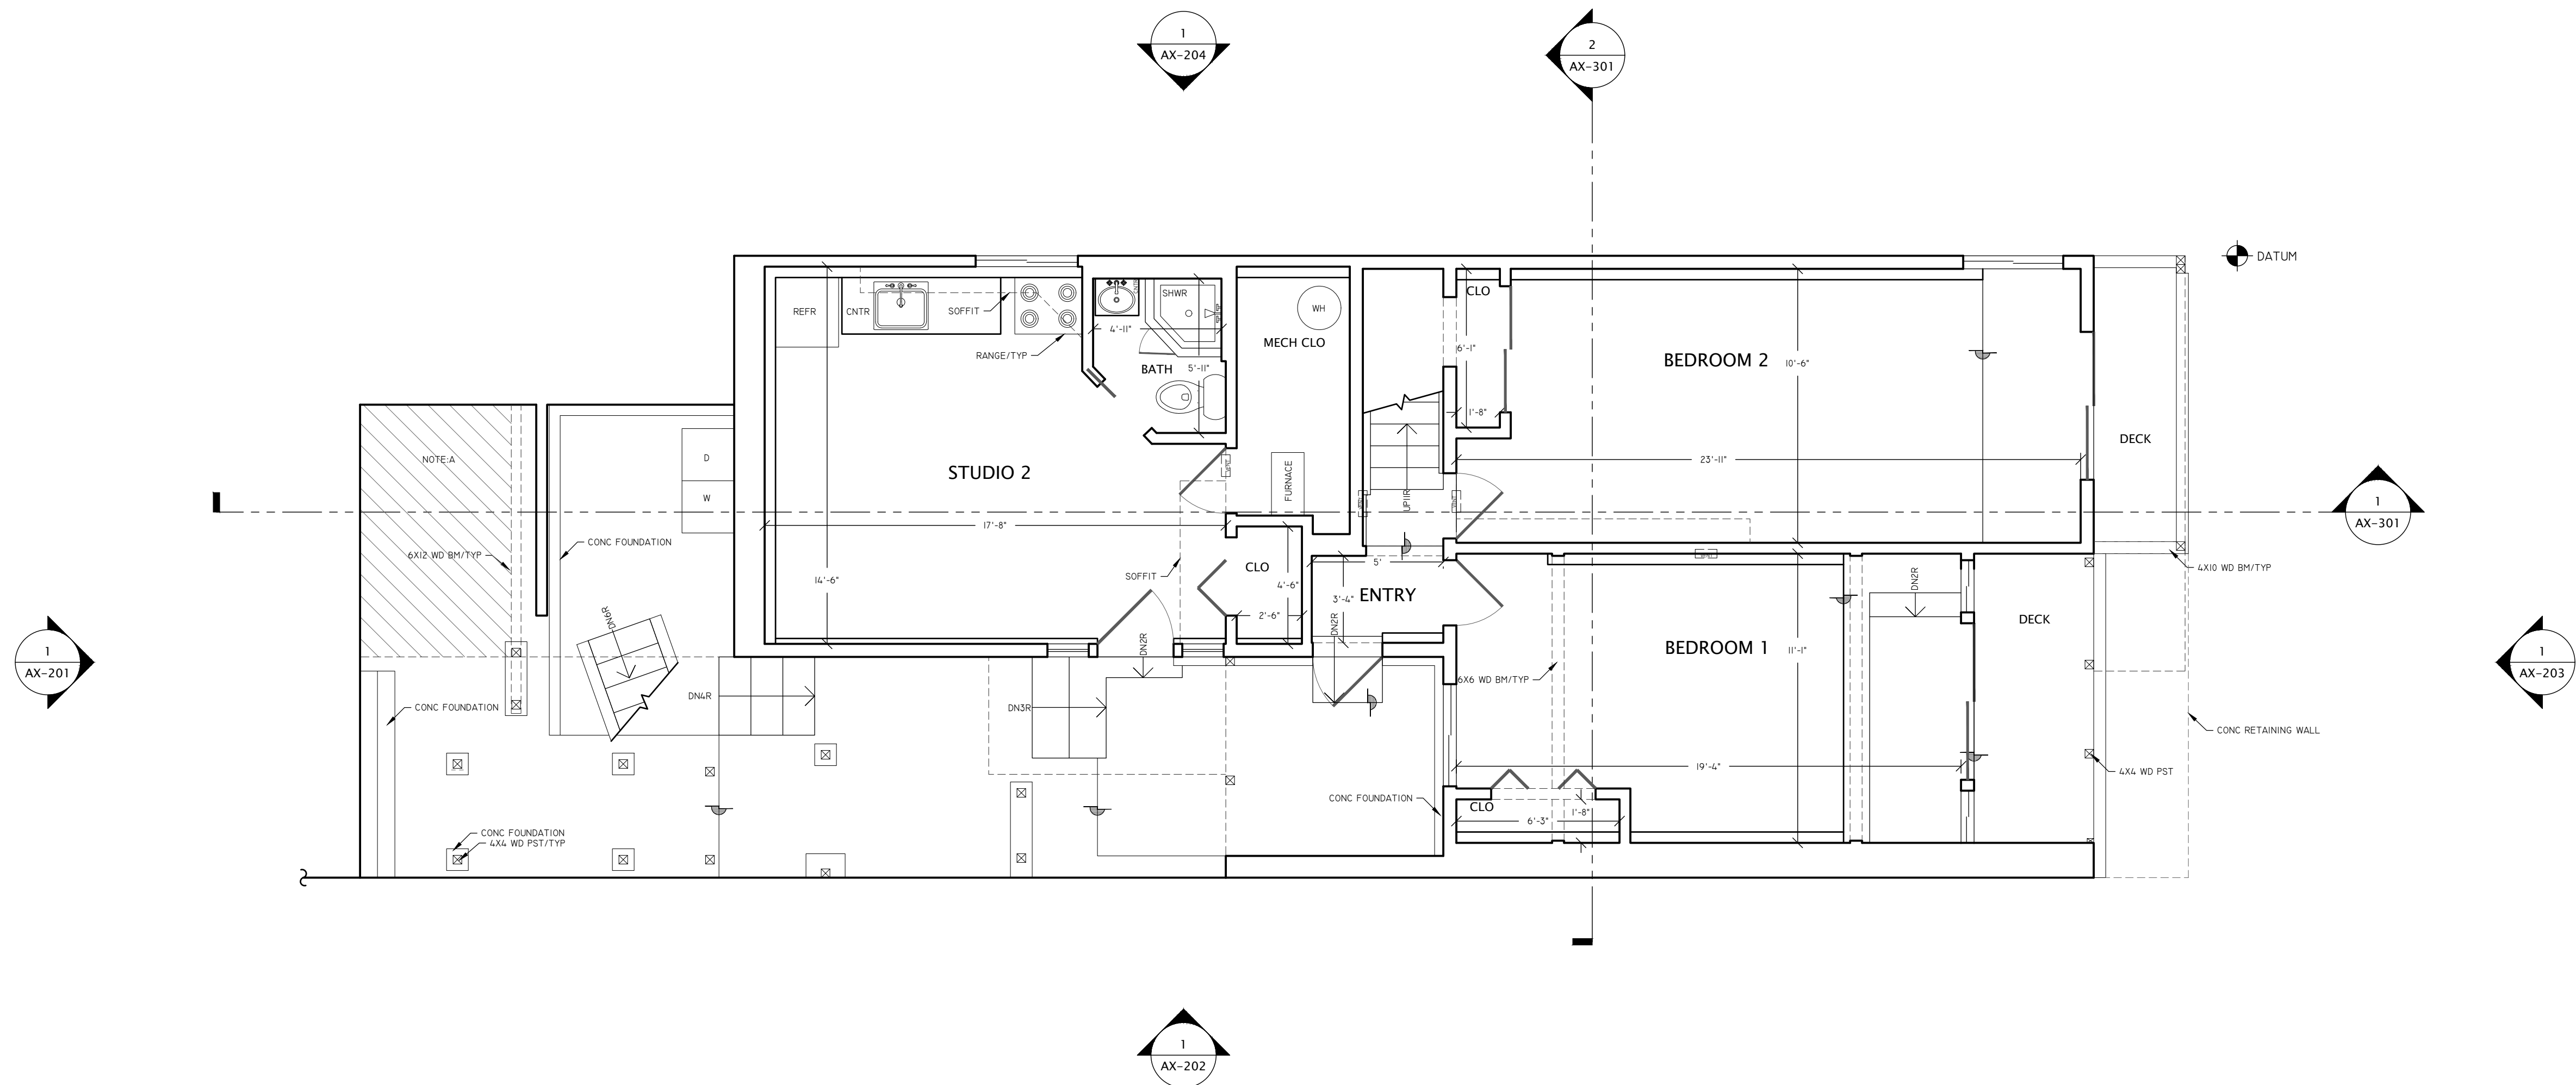

1 EXISTING LOWER LEVEL FLOOR PLAN
968 SQFT GROSS MEASURED AREA
581 SQFT MEASURED EXTERIOR SURFACES

NOTE A:
THIS AREA NOT ACCESSIBLE AT TIME OF DATA ACQUISITION,
AREA NOT MEASURED.

697 RHODE ISLAND STREET
SAN FRANCISCO, CA 94107

THIS DRAWING IS A RECORD OF REAL PROPERTY
THAT IS GENERALLY ACCEPTED TO BE SUITABLE
FOR USE IN PLANNING, DESIGN, LEASE, AND
GENERAL ASSET MANAGEMENT. IT SHOULD NOT BE
USED TO DETERMINE EXACT MEASUREMENTS OF
SPACES OR ARTIFACTS FOUND HEREIN FOR ANY
PURPOSE.
EXTERIOR ELEMENTS HAVE BEEN MEASURED AND
DRAFTED FOR REFERENCE ONLY - THIS IS NOT A
SURVEY.




EXISTING FLOOR PLAN


REF: 697sf_City_SFD
REV: 0
DRAWN BY: MV
AUDITED BY: JK

SHEET SIZE: 24x36
SCALE: 1/4"=1'-0"
FIELD MEASURE:
4/10/20


AX-102
2 OF 7

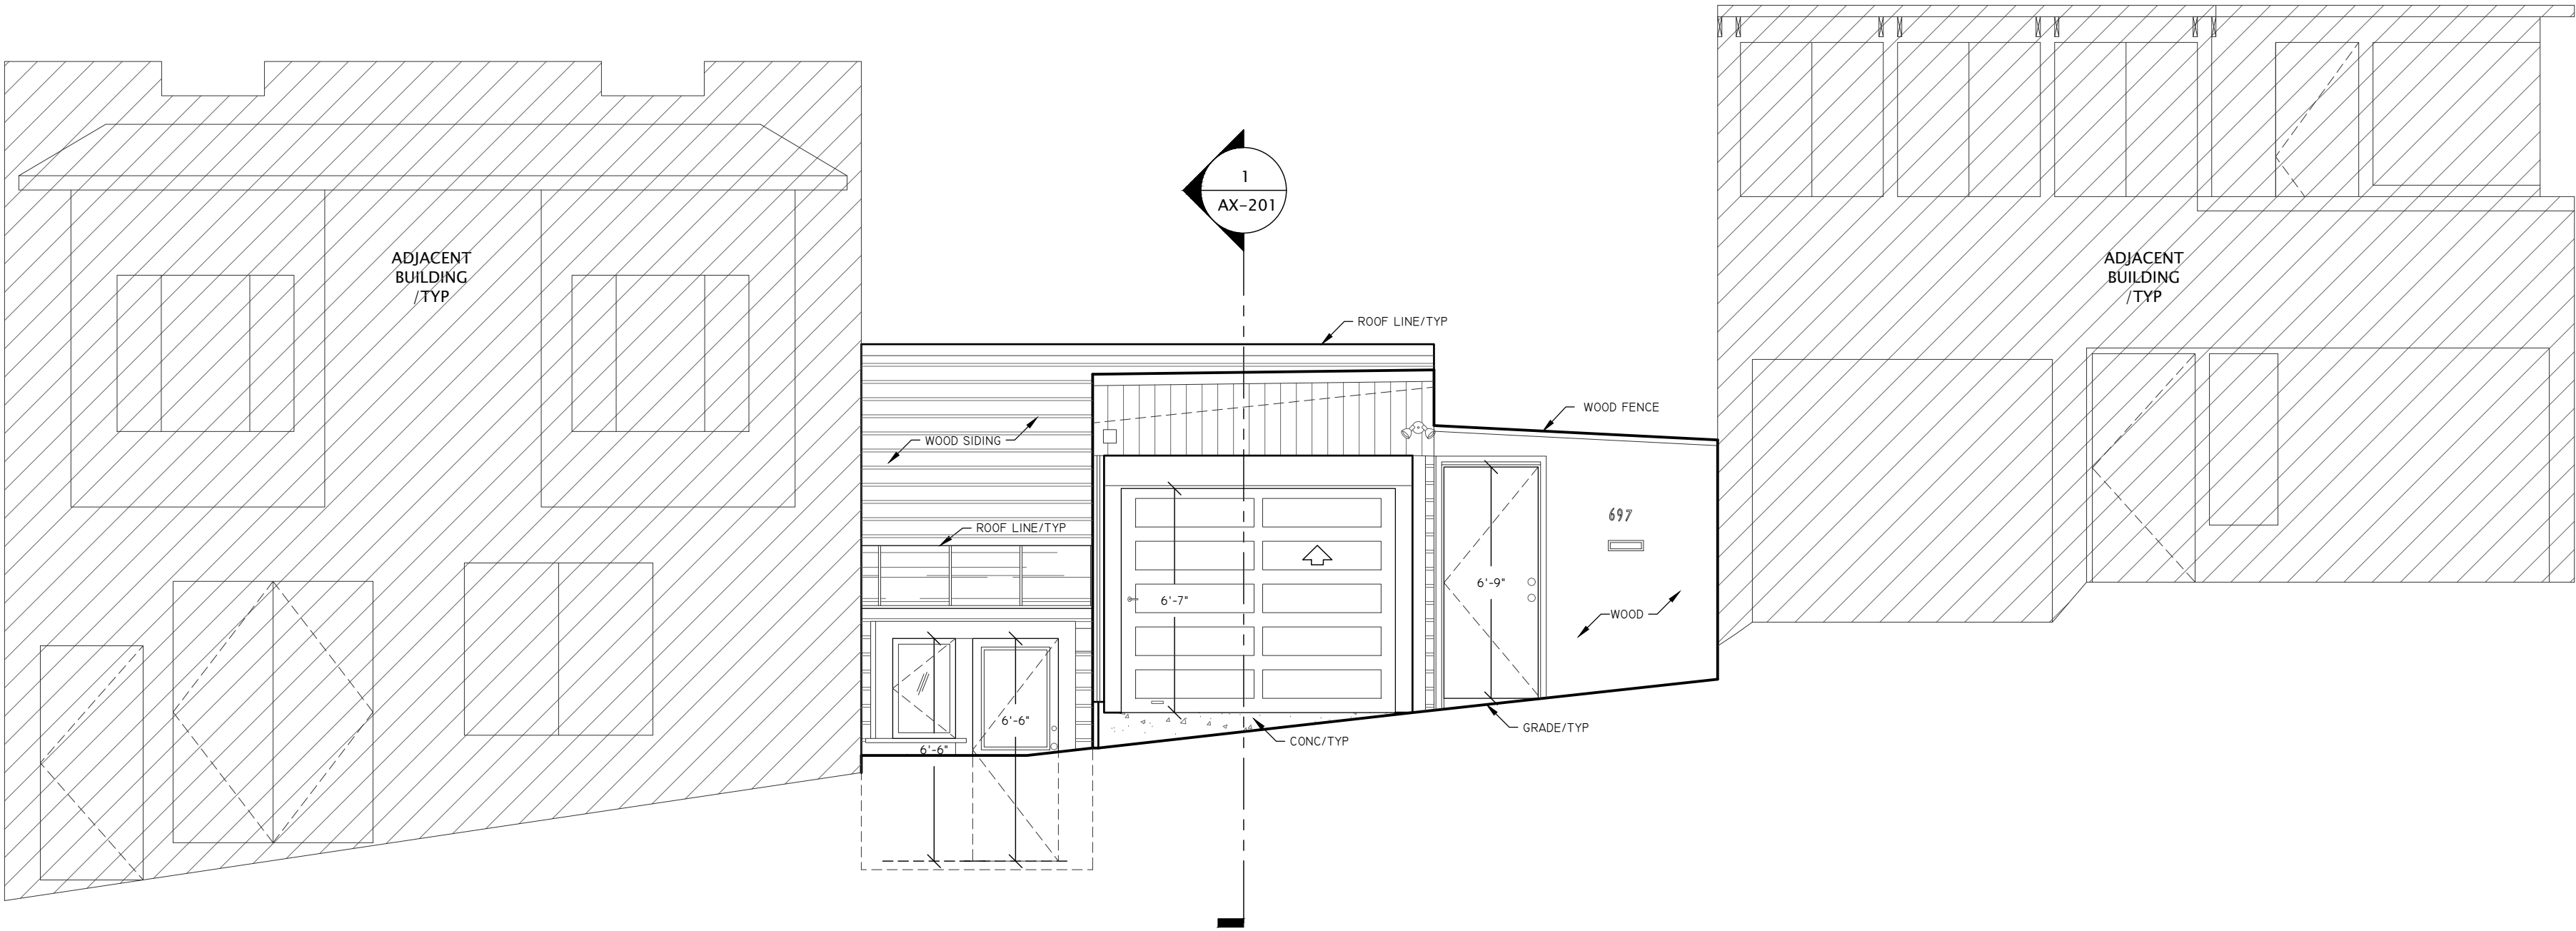

1 EXISTING WEST ELEVATION

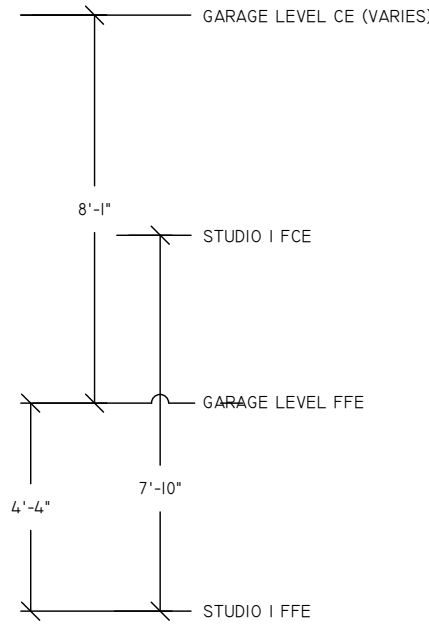

697 RHODE ISLAND STREET SAN FRANCISCO, CA 94107		
THIS DRAWING IS A RECORD OF REAL PROPERTY THAT IS GENERALLY ACCEPTED TO BE SUITABLE FOR USE IN PLANNING, DESIGN, LEASE, AND GENERAL ASSET MANAGEMENT. IT SHOULD NOT BE USED TO DETERMINE EXACT MEASUREMENTS OF SPACES OR ARTIFACTS FOUND HEREIN FOR ANY PURPOSE. EXTERIOR ELEMENTS HAVE BEEN MEASURED AND DRAFTED FOR REFERENCE ONLY - THIS IS NOT A SURVEY.	 RED BRIDGE DESIGN SAN FRANCISCO REDBRIDGEDESIGN.COM	
EXISTING EXTERIOR ELEVATIONS		
REF: 697sf_City_SFD REV: 0 DRAWN BY: MV AUDITED BY: JK	SHEET SIZE: 24x36 SCALE: 1/4"=1'-0" FIELD MEASURE: 4/10/20	AX-201 3 OF 7

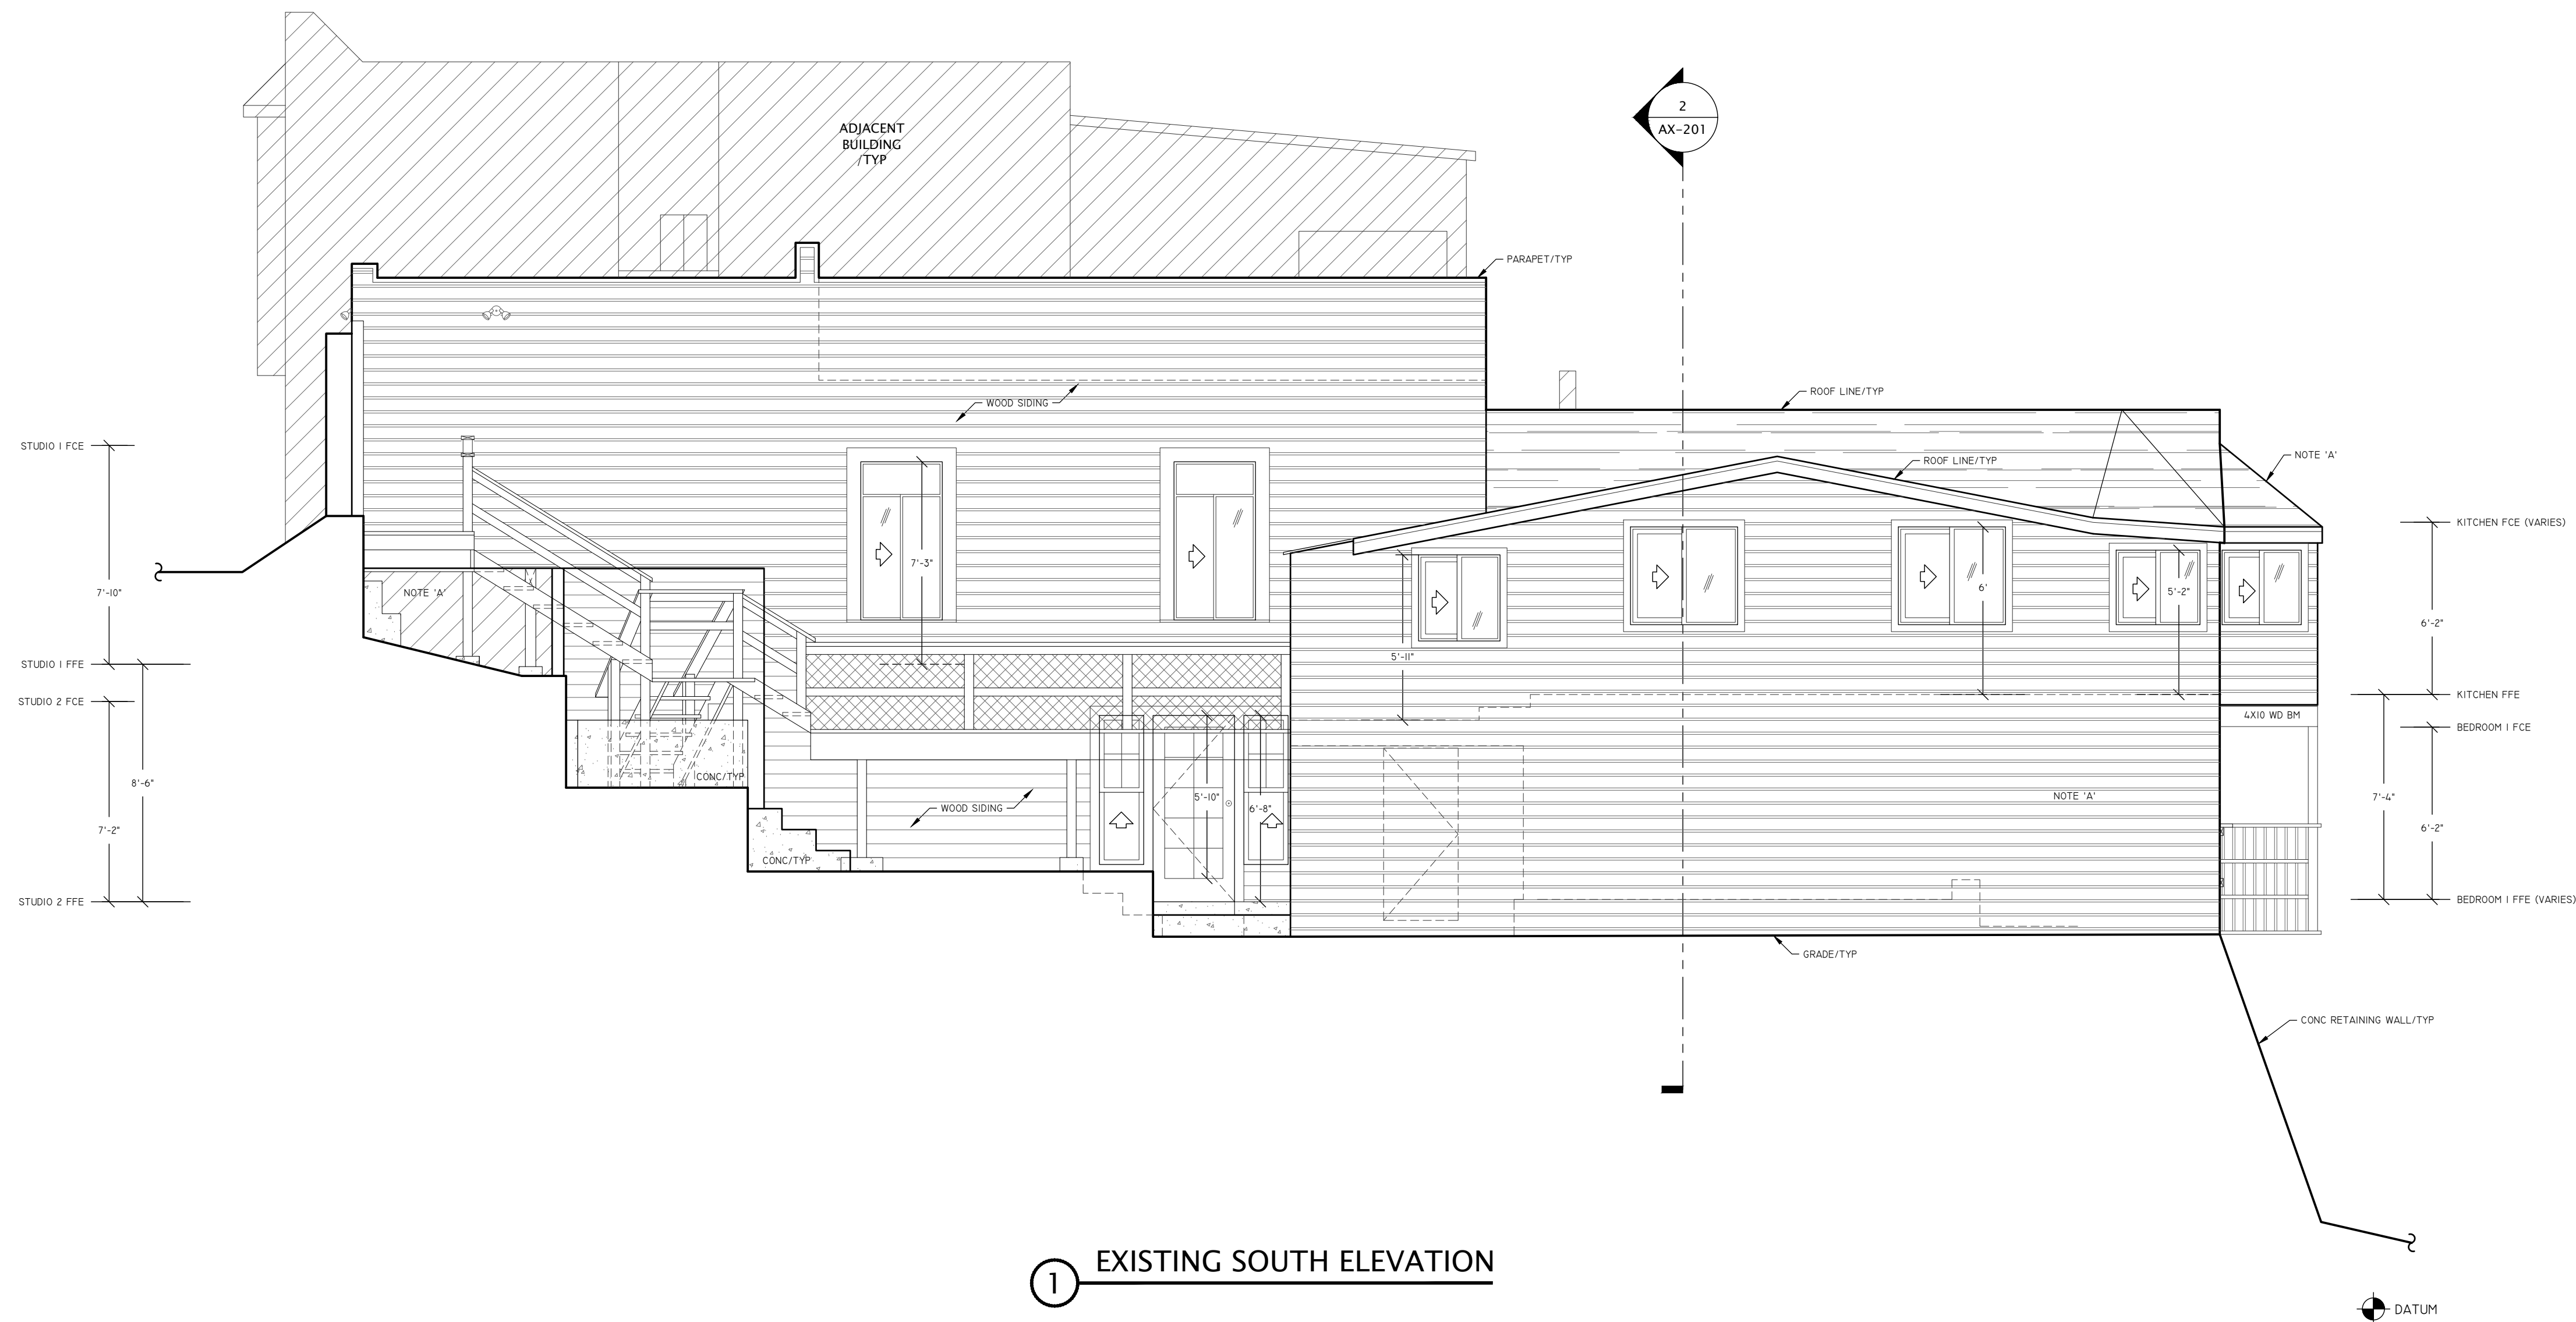


1 EXISTING SOUTH ELEVATION

NOTE A:
THIS AREA NOT ACCESSIBLE AT TIME OF DATA ACQUISITION,
AREA NOT MEASURED.

697 RHODE ISLAND STREET
SAN FRANCISCO, CA 94107

THIS DRAWING IS A RECORD OF REAL PROPERTY
THAT IS GENERALLY ACCEPTED TO BE SUITABLE
FOR USE IN PLANNING, DESIGN, LEASE, AND
GENERAL ASSET MANAGEMENT. IT SHOULD NOT BE
USED TO DETERMINE EXACT MEASUREMENTS OF
SPACES OR ARTIFACTS FOUND HEREIN FOR ANY
PURPOSE.
EXTERIOR ELEMENTS HAVE BEEN MEASURED AND
DRAFTED FOR REFERENCE ONLY - THIS IS NOT A
SURVEY.

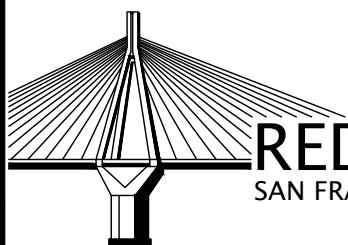

RED BRIDGE DESIGN
SAN FRANCISCO
REDBRIDGEDESIGN.COM

EXISTING EXTERIOR ELEVATIONS

REF: 697sf_City_SFD
REV: 0
DRAWN BY: MV
AUDITED BY: JK

SHEET SIZE: 24x36
SCALE: 1/4"=1'-0"
FIELD MEASURE:
4/10/20

AX-202
4 OF 7



NOTE A:
THIS AREA NOT ACCESSIBLE AT TIME OF DATA ACQUISITION,
AREA NOT MEASURED.

697 RHODE ISLAND STREET
SAN FRANCISCO, CA 94107

THIS DRAWING IS A RECORD OF REAL PROPERTY
THAT IS GENERALLY ACCEPTED TO BE SUITABLE
FOR USE IN PLANNING, DESIGN, LEASE, AND
GENERAL ASSET MANAGEMENT. IT SHOULD NOT BE
USED TO DETERMINE EXACT MEASUREMENTS OF
SPACES OR ARTIFACTS FOUND HEREIN FOR ANY
PURPOSE.
EXTERIOR ELEMENTS HAVE BEEN MEASURED AND
DRAFTED FOR REFERENCE ONLY - THIS IS NOT A
SURVEY.




EXISTING EXTERIOR ELEVATIONS

REF: 697sf_City_SFD
REV: 0
DRAWN BY: MV
AUDITED BY: JK

SHEET SIZE: 24x36
SCALE: 1/4"=1'-0"
FIELD MEASURE:
4/10/20

AX-203
5 OF 7

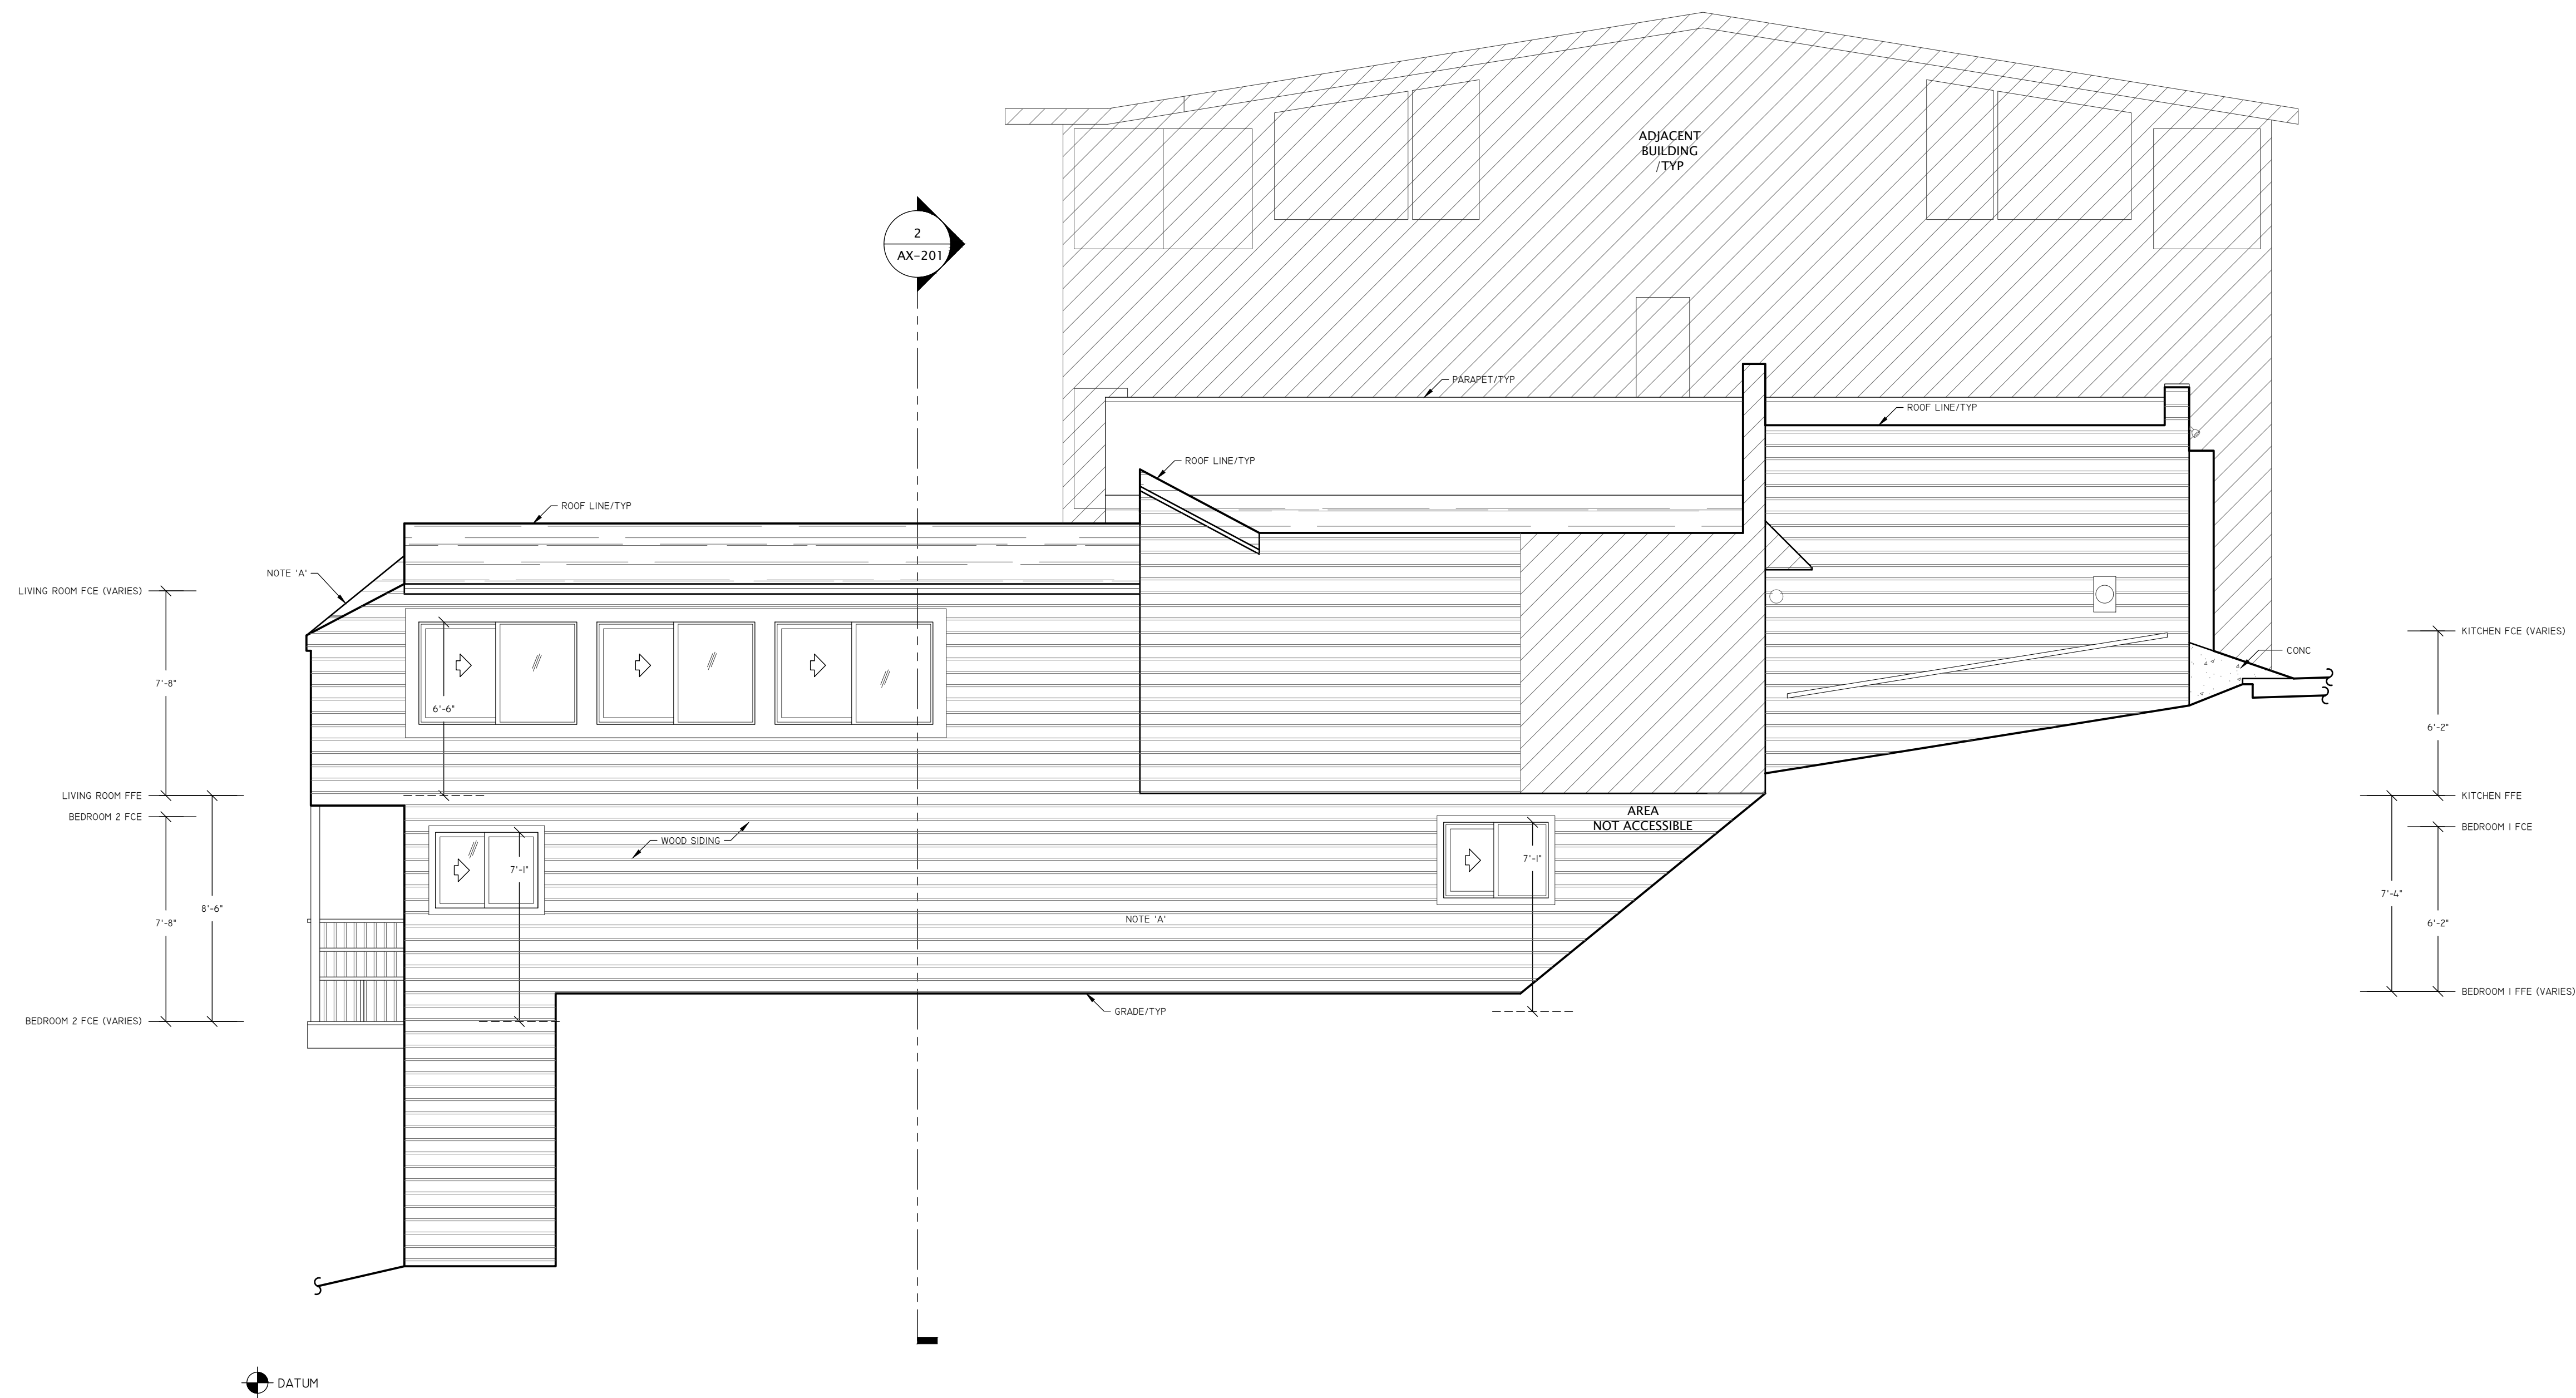

1 EXISTING NORTH ELEVATION

NOTE A:
THIS AREA NOT ACCESSIBLE AT TIME OF DATA ACQUISITION,
AREA NOT MEASURED.

697 RHODE ISLAND STREET
SAN FRANCISCO, CA 94107

THIS DRAWING IS A RECORD OF REAL PROPERTY
THAT IS GENERALLY ACCEPTED TO BE SUITABLE
FOR USE IN PLANNING, DESIGN, LEASE, AND
GENERAL ASSET MANAGEMENT. IT SHOULD NOT BE
USED TO DETERMINE EXACT MEASUREMENTS OF
SPACES OR ARTIFACTS FOUND HEREIN FOR ANY
PURPOSE.
EXTERIOR ELEMENTS HAVE BEEN MEASURED AND
DRAFTED FOR REFERENCE ONLY - THIS IS NOT A
SURVEY.




RED BRIDGE DESIGN
SAN FRANCISCO REDBRIDGEDSIGN.COM

EXISTING EXTERIOR ELEVATIONS


REF: 697sf_City_SFD
REV: 0
DRAWN BY: MV
AUDITED BY: JK

SHEET SIZE: 24x36
SCALE: 1/4"=1'-0"
FIELD MEASURE:
4/10/20

AX-204
6 OF 7

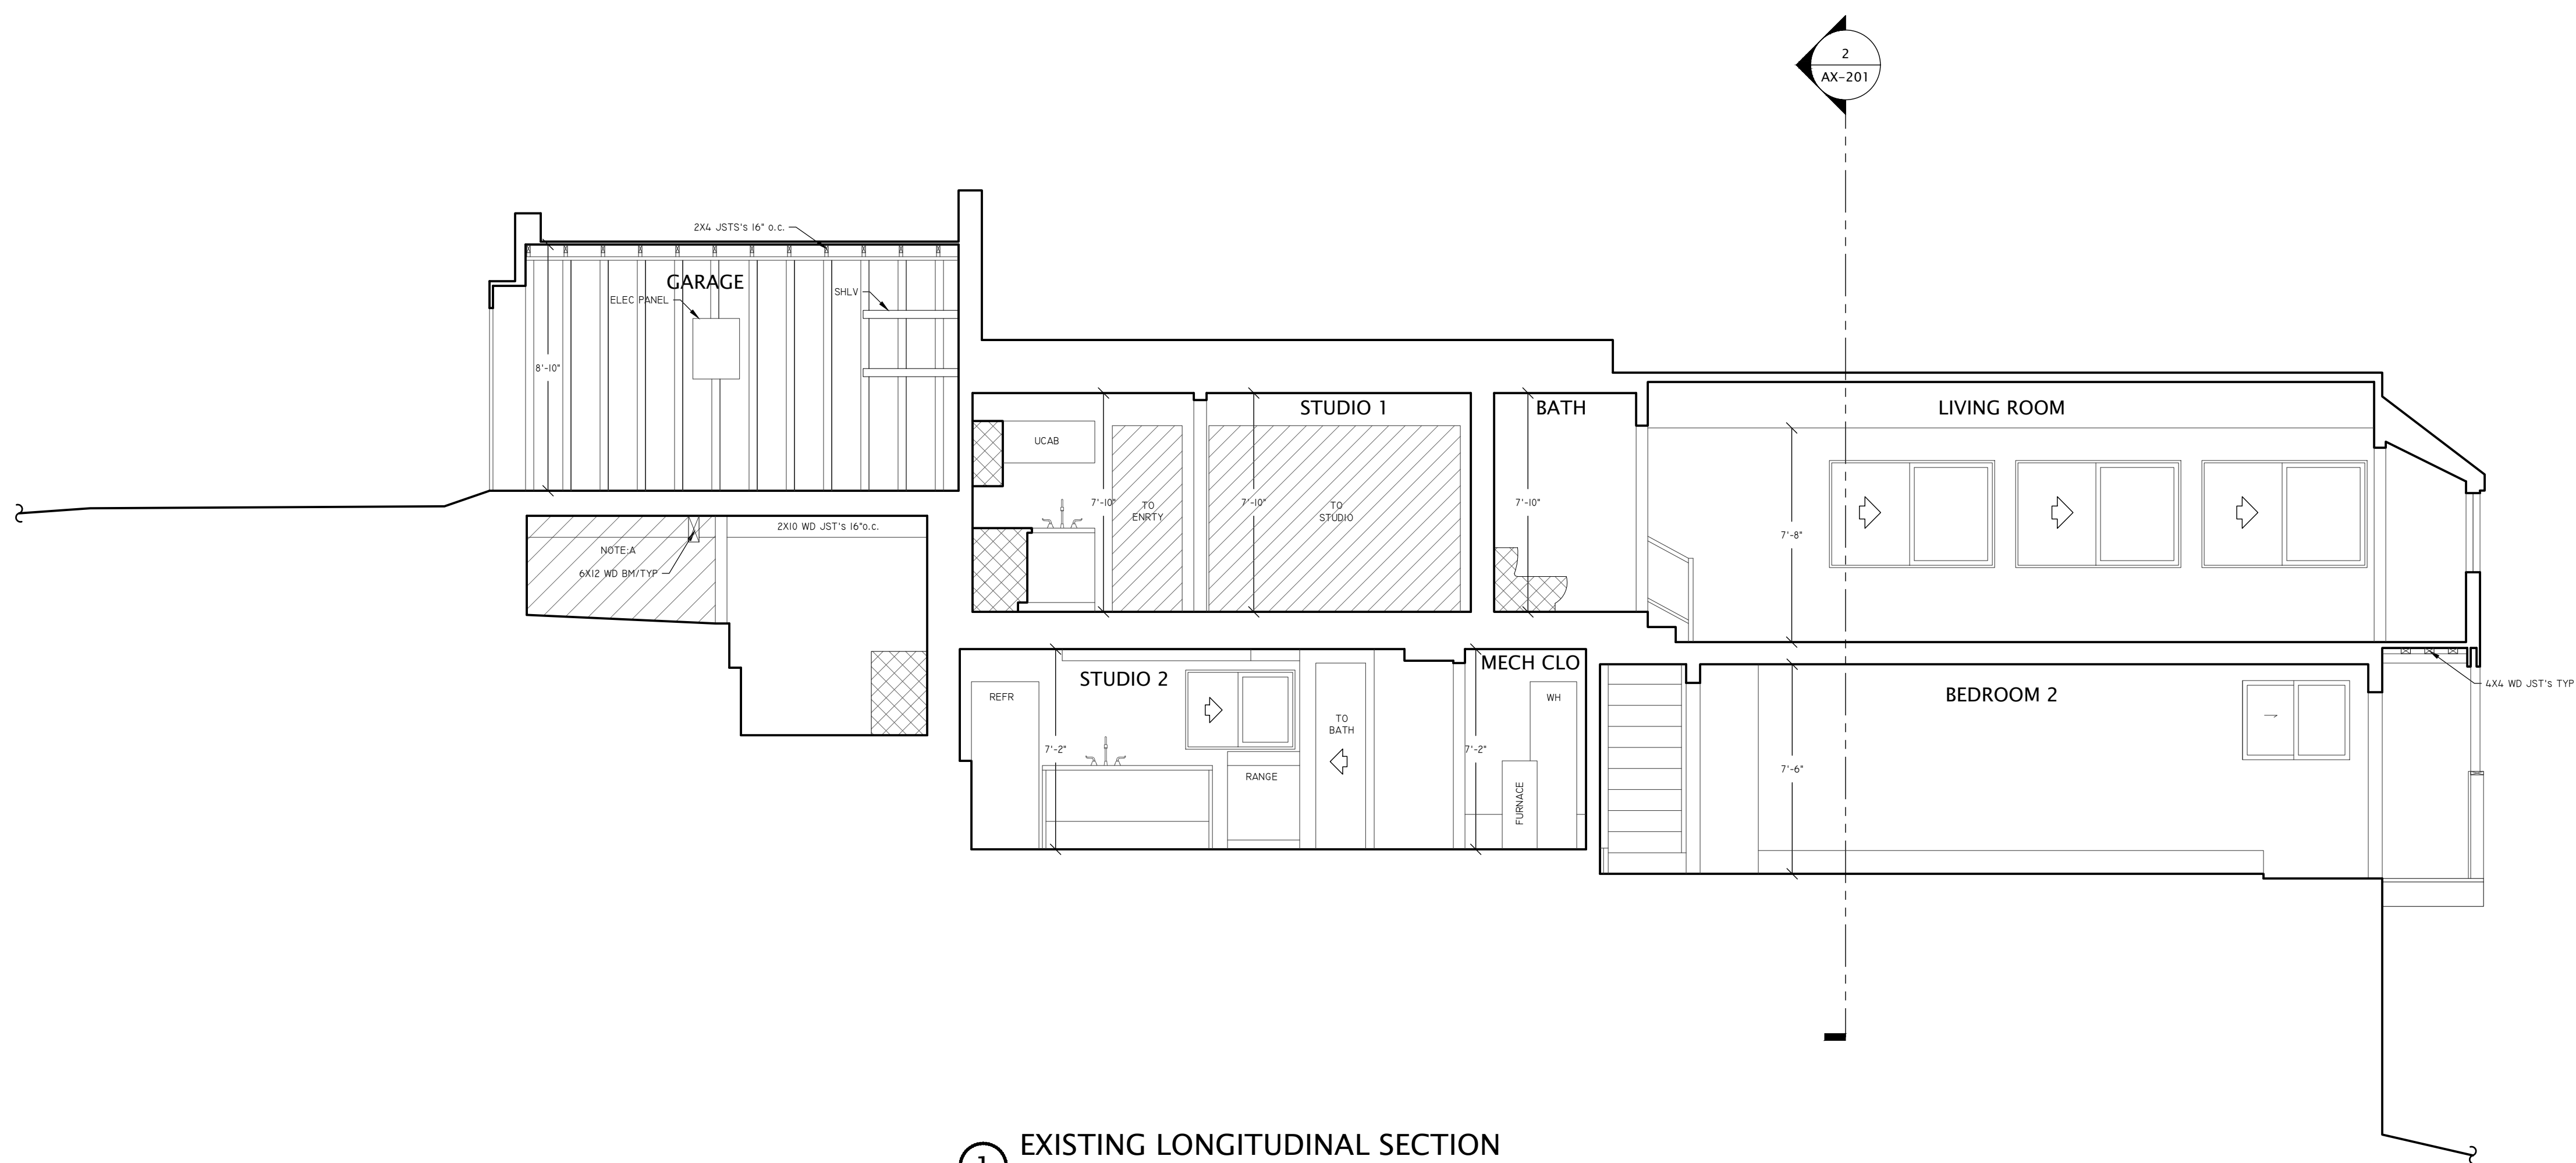

1 EXISTING LONGITUDINAL SECTION

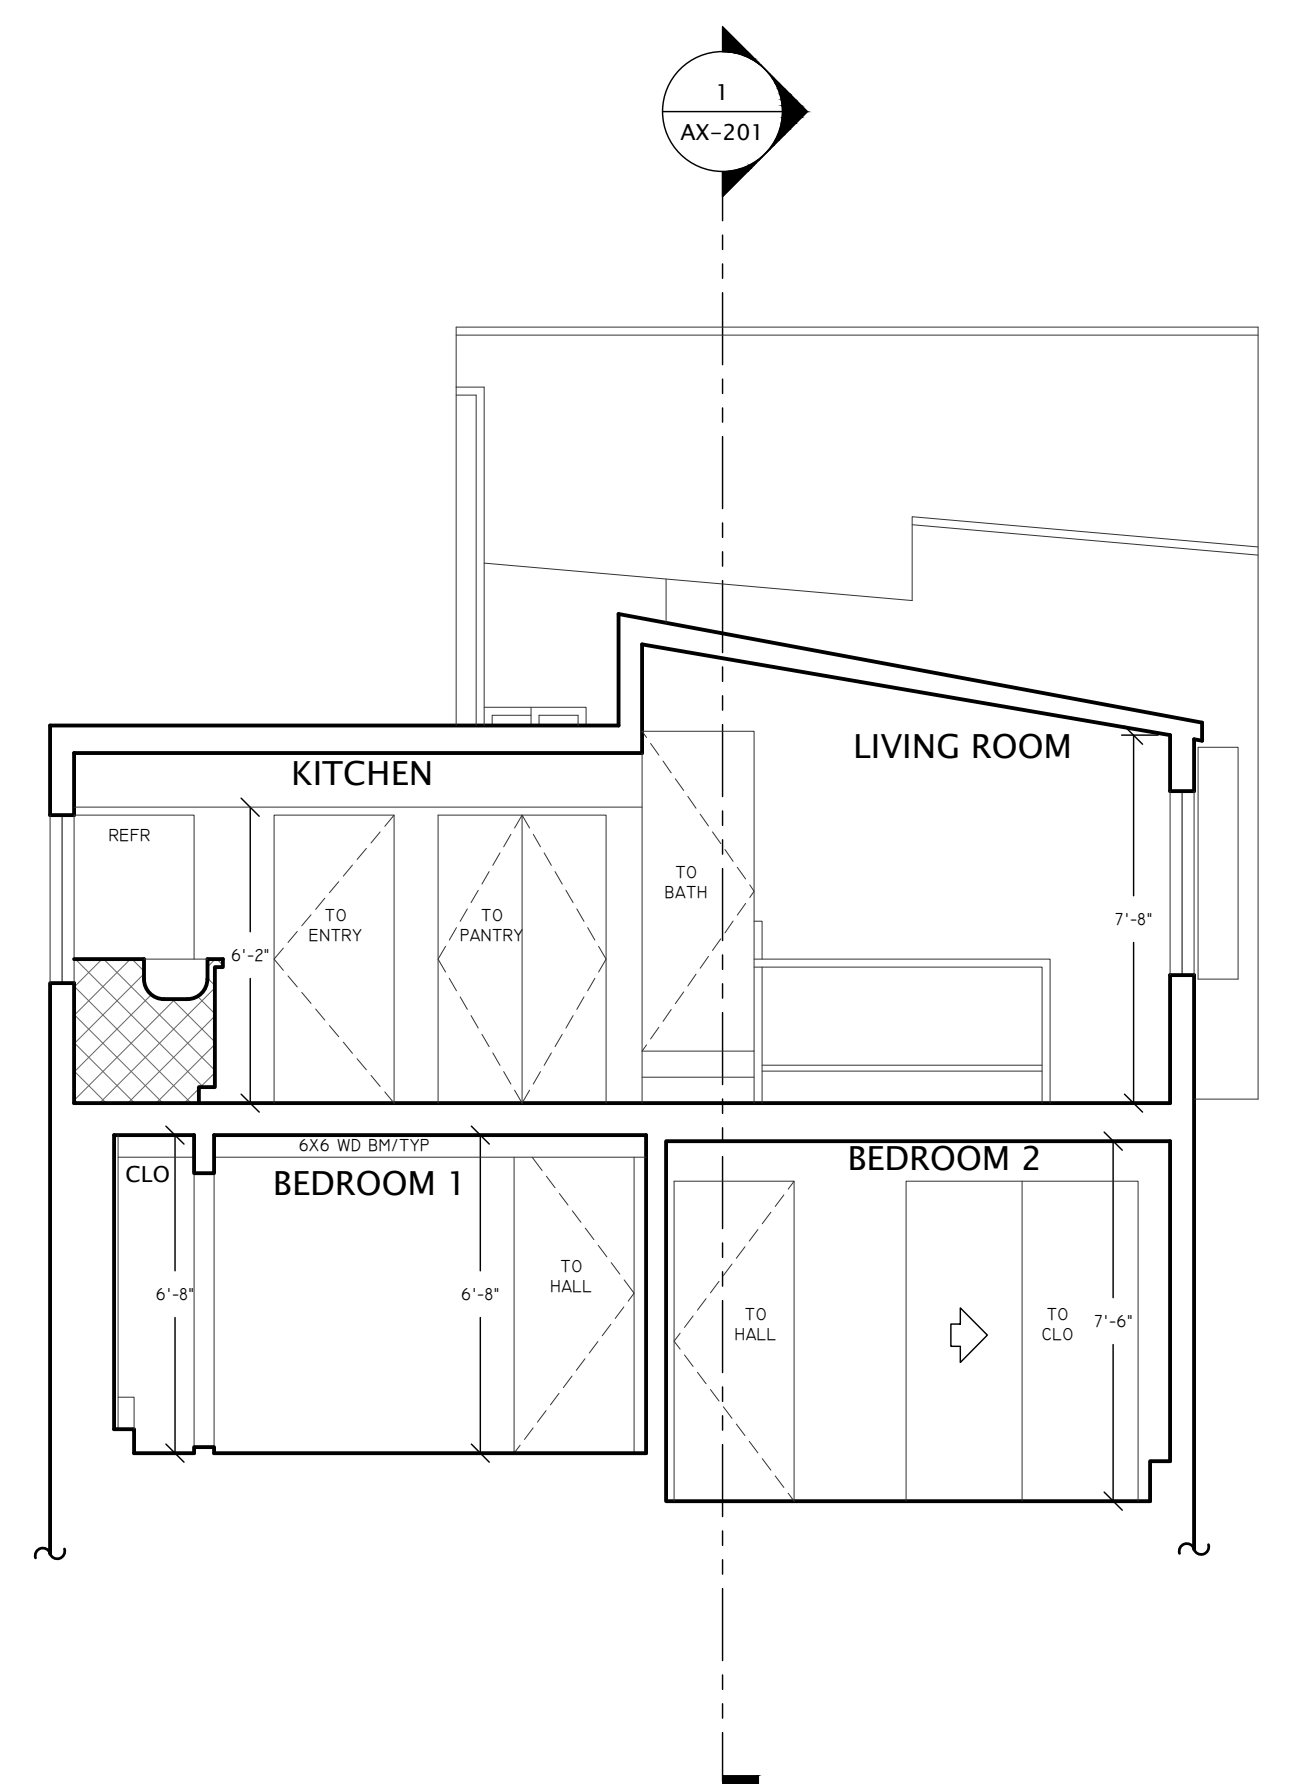

2 EXISTING CROSS SECTION



697 RHODE ISLAND STREET SAN FRANCISCO, CA 94107		
THIS DRAWING IS A RECORD OF REAL PROPERTY THAT IS GENERALLY ACCEPTED TO BE SUITABLE FOR USE IN PLANNING, DESIGN, LEASE, AND GENERAL ASSET MANAGEMENT. IT SHOULD NOT BE USED TO DETERMINE EXACT MEASUREMENTS OF SPACES OR ARTIFACTS FOUND HEREIN FOR ANY PURPOSE. EXTERIOR ELEMENTS HAVE BEEN MEASURED AND DRAFTED FOR REFERENCE ONLY - THIS IS NOT A SURVEY.	 RED BRIDGE DESIGN SAN FRANCISCO REDBRIDGEDESIGN.COM	
EXISTING BUILDING SECTIONS		
REF: 697sf_City_SFD REV: 0 DRAWN BY: MV AUDITED BY: JK	SHEET SIZE: 24x36 SCALE: 1/4"=1'-0" FIELD MEASURE: 4/10/20	AX-301 7 OF 7